
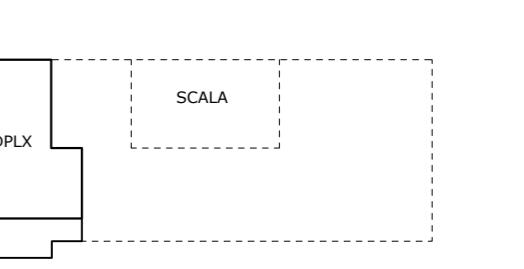
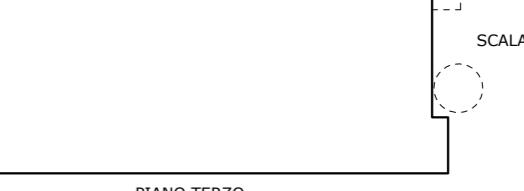
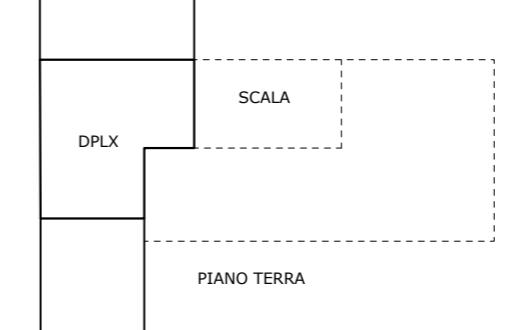
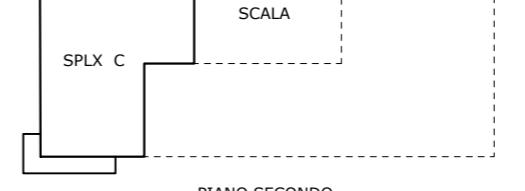
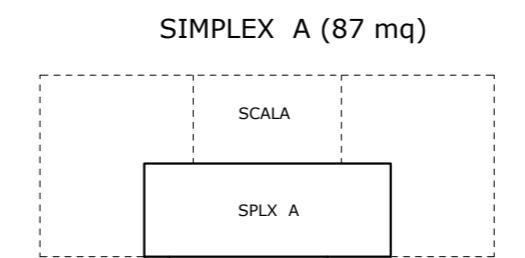
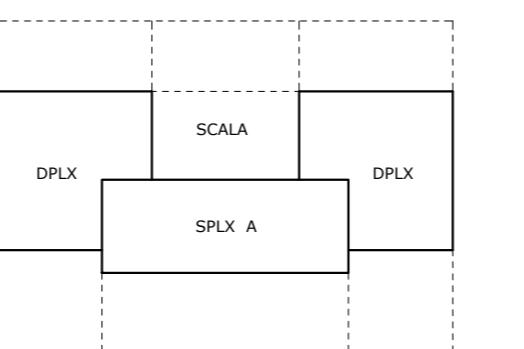
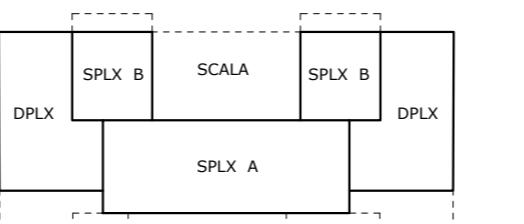
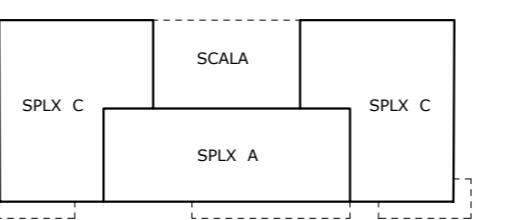
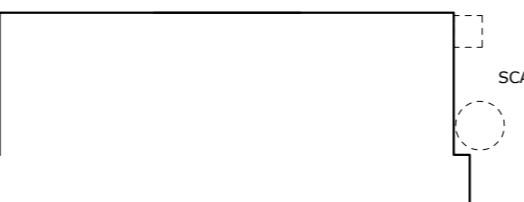


PIANTE TIPO
TAVOLA 1



Scala 1:500


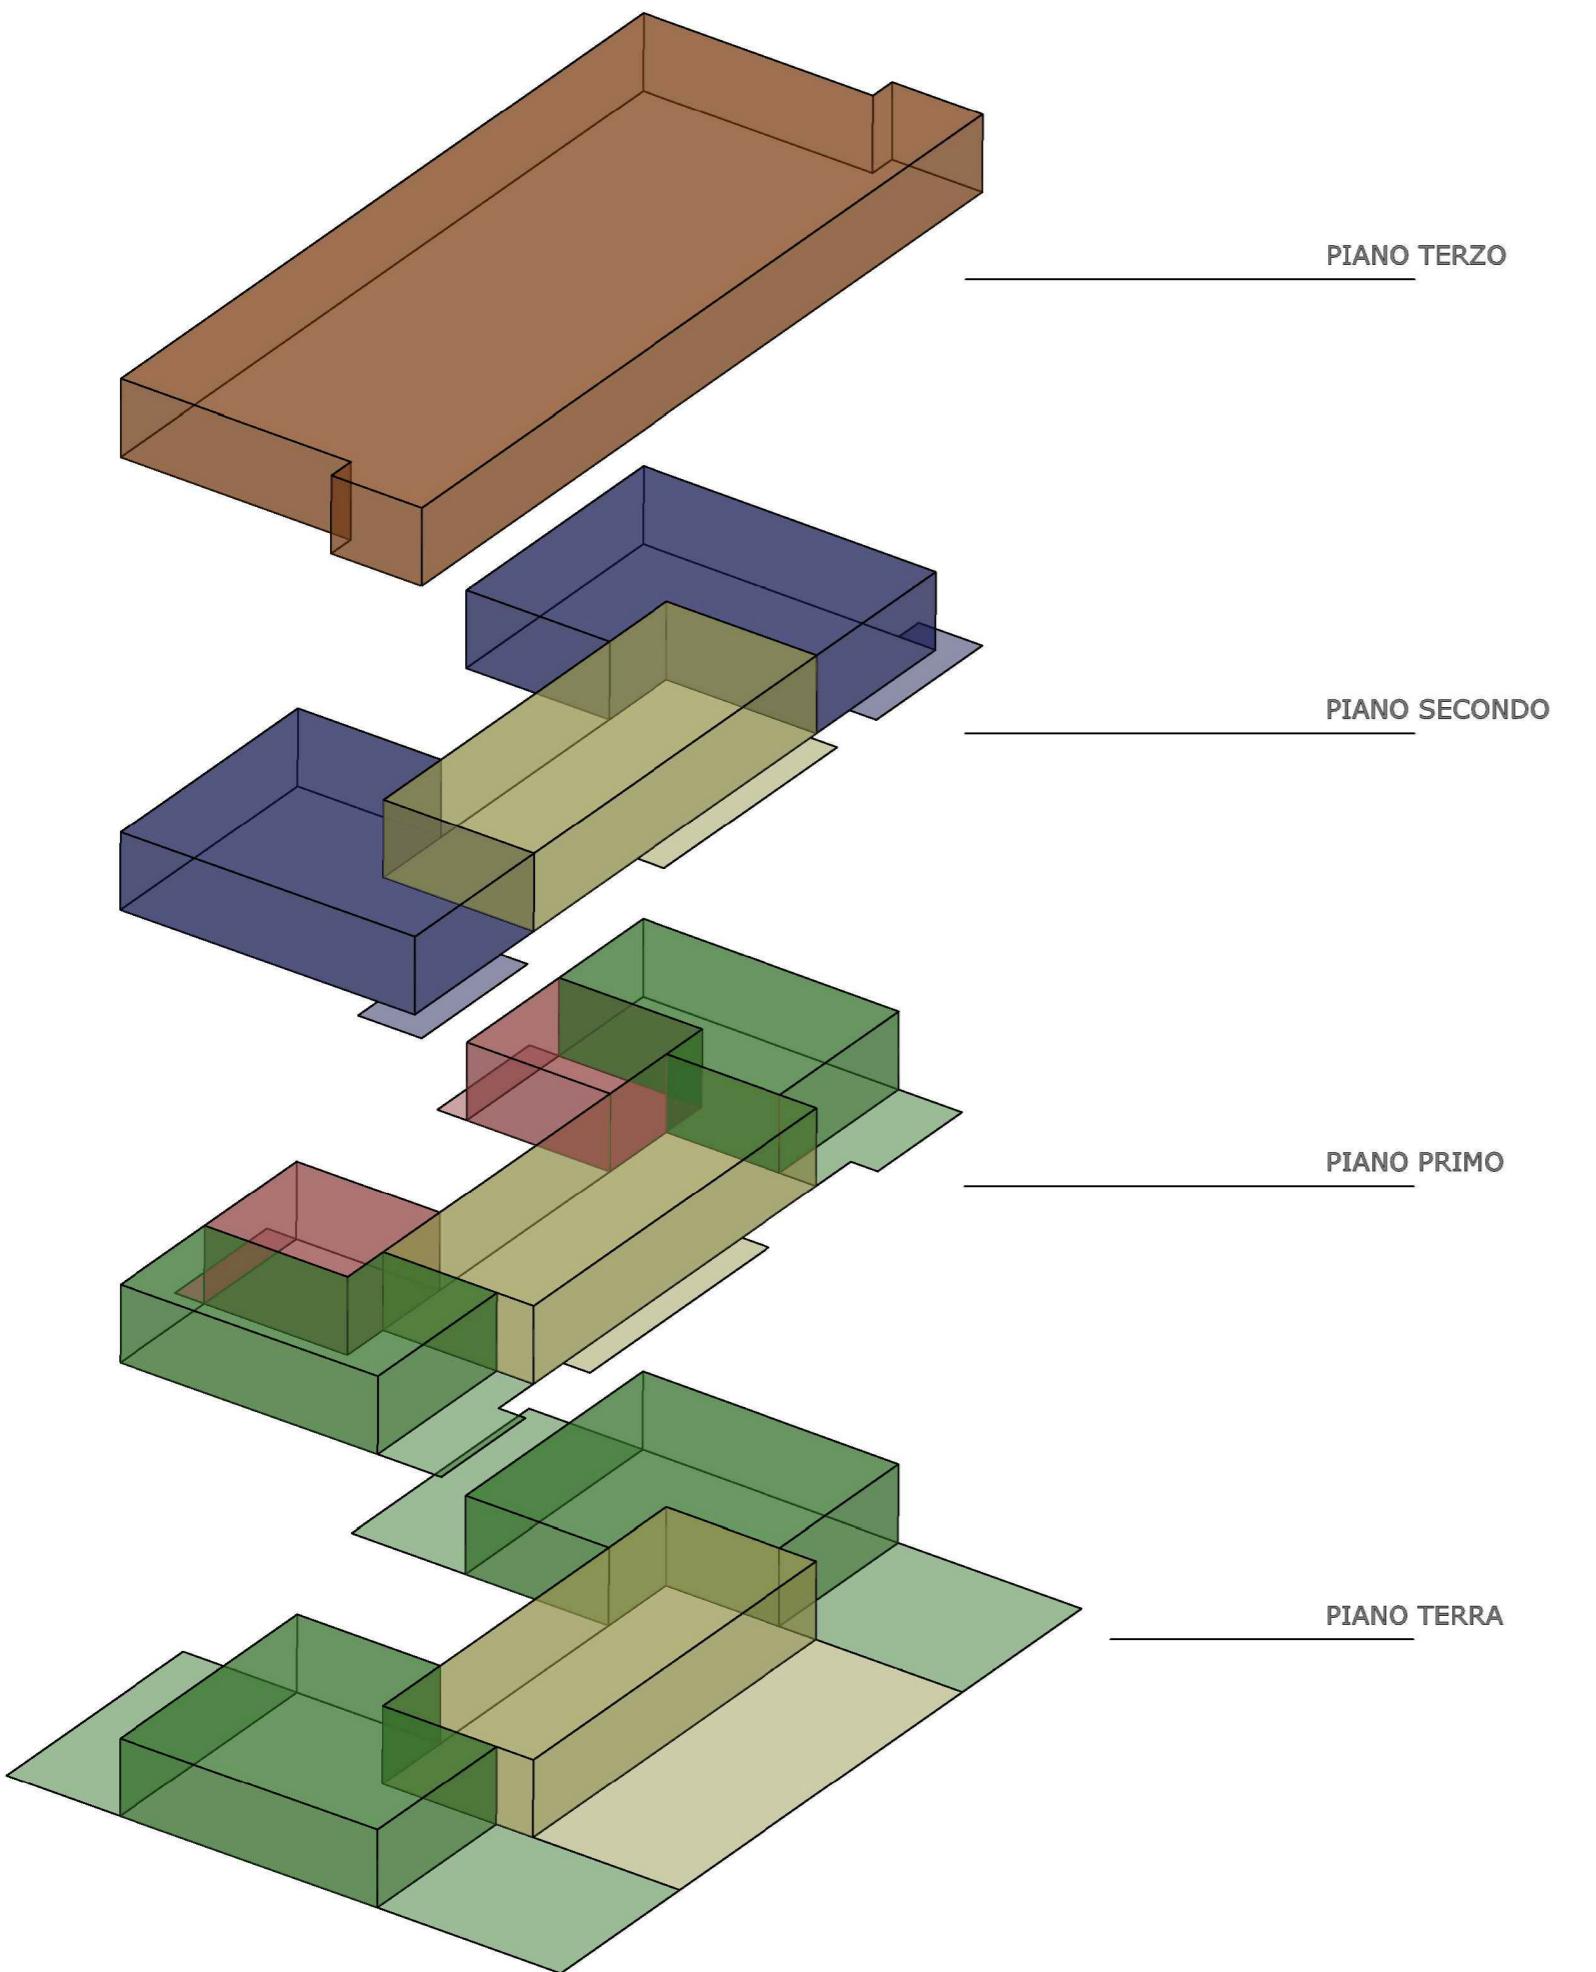


PLANIMETRIA

TAVOLA 2

Scala 1:100

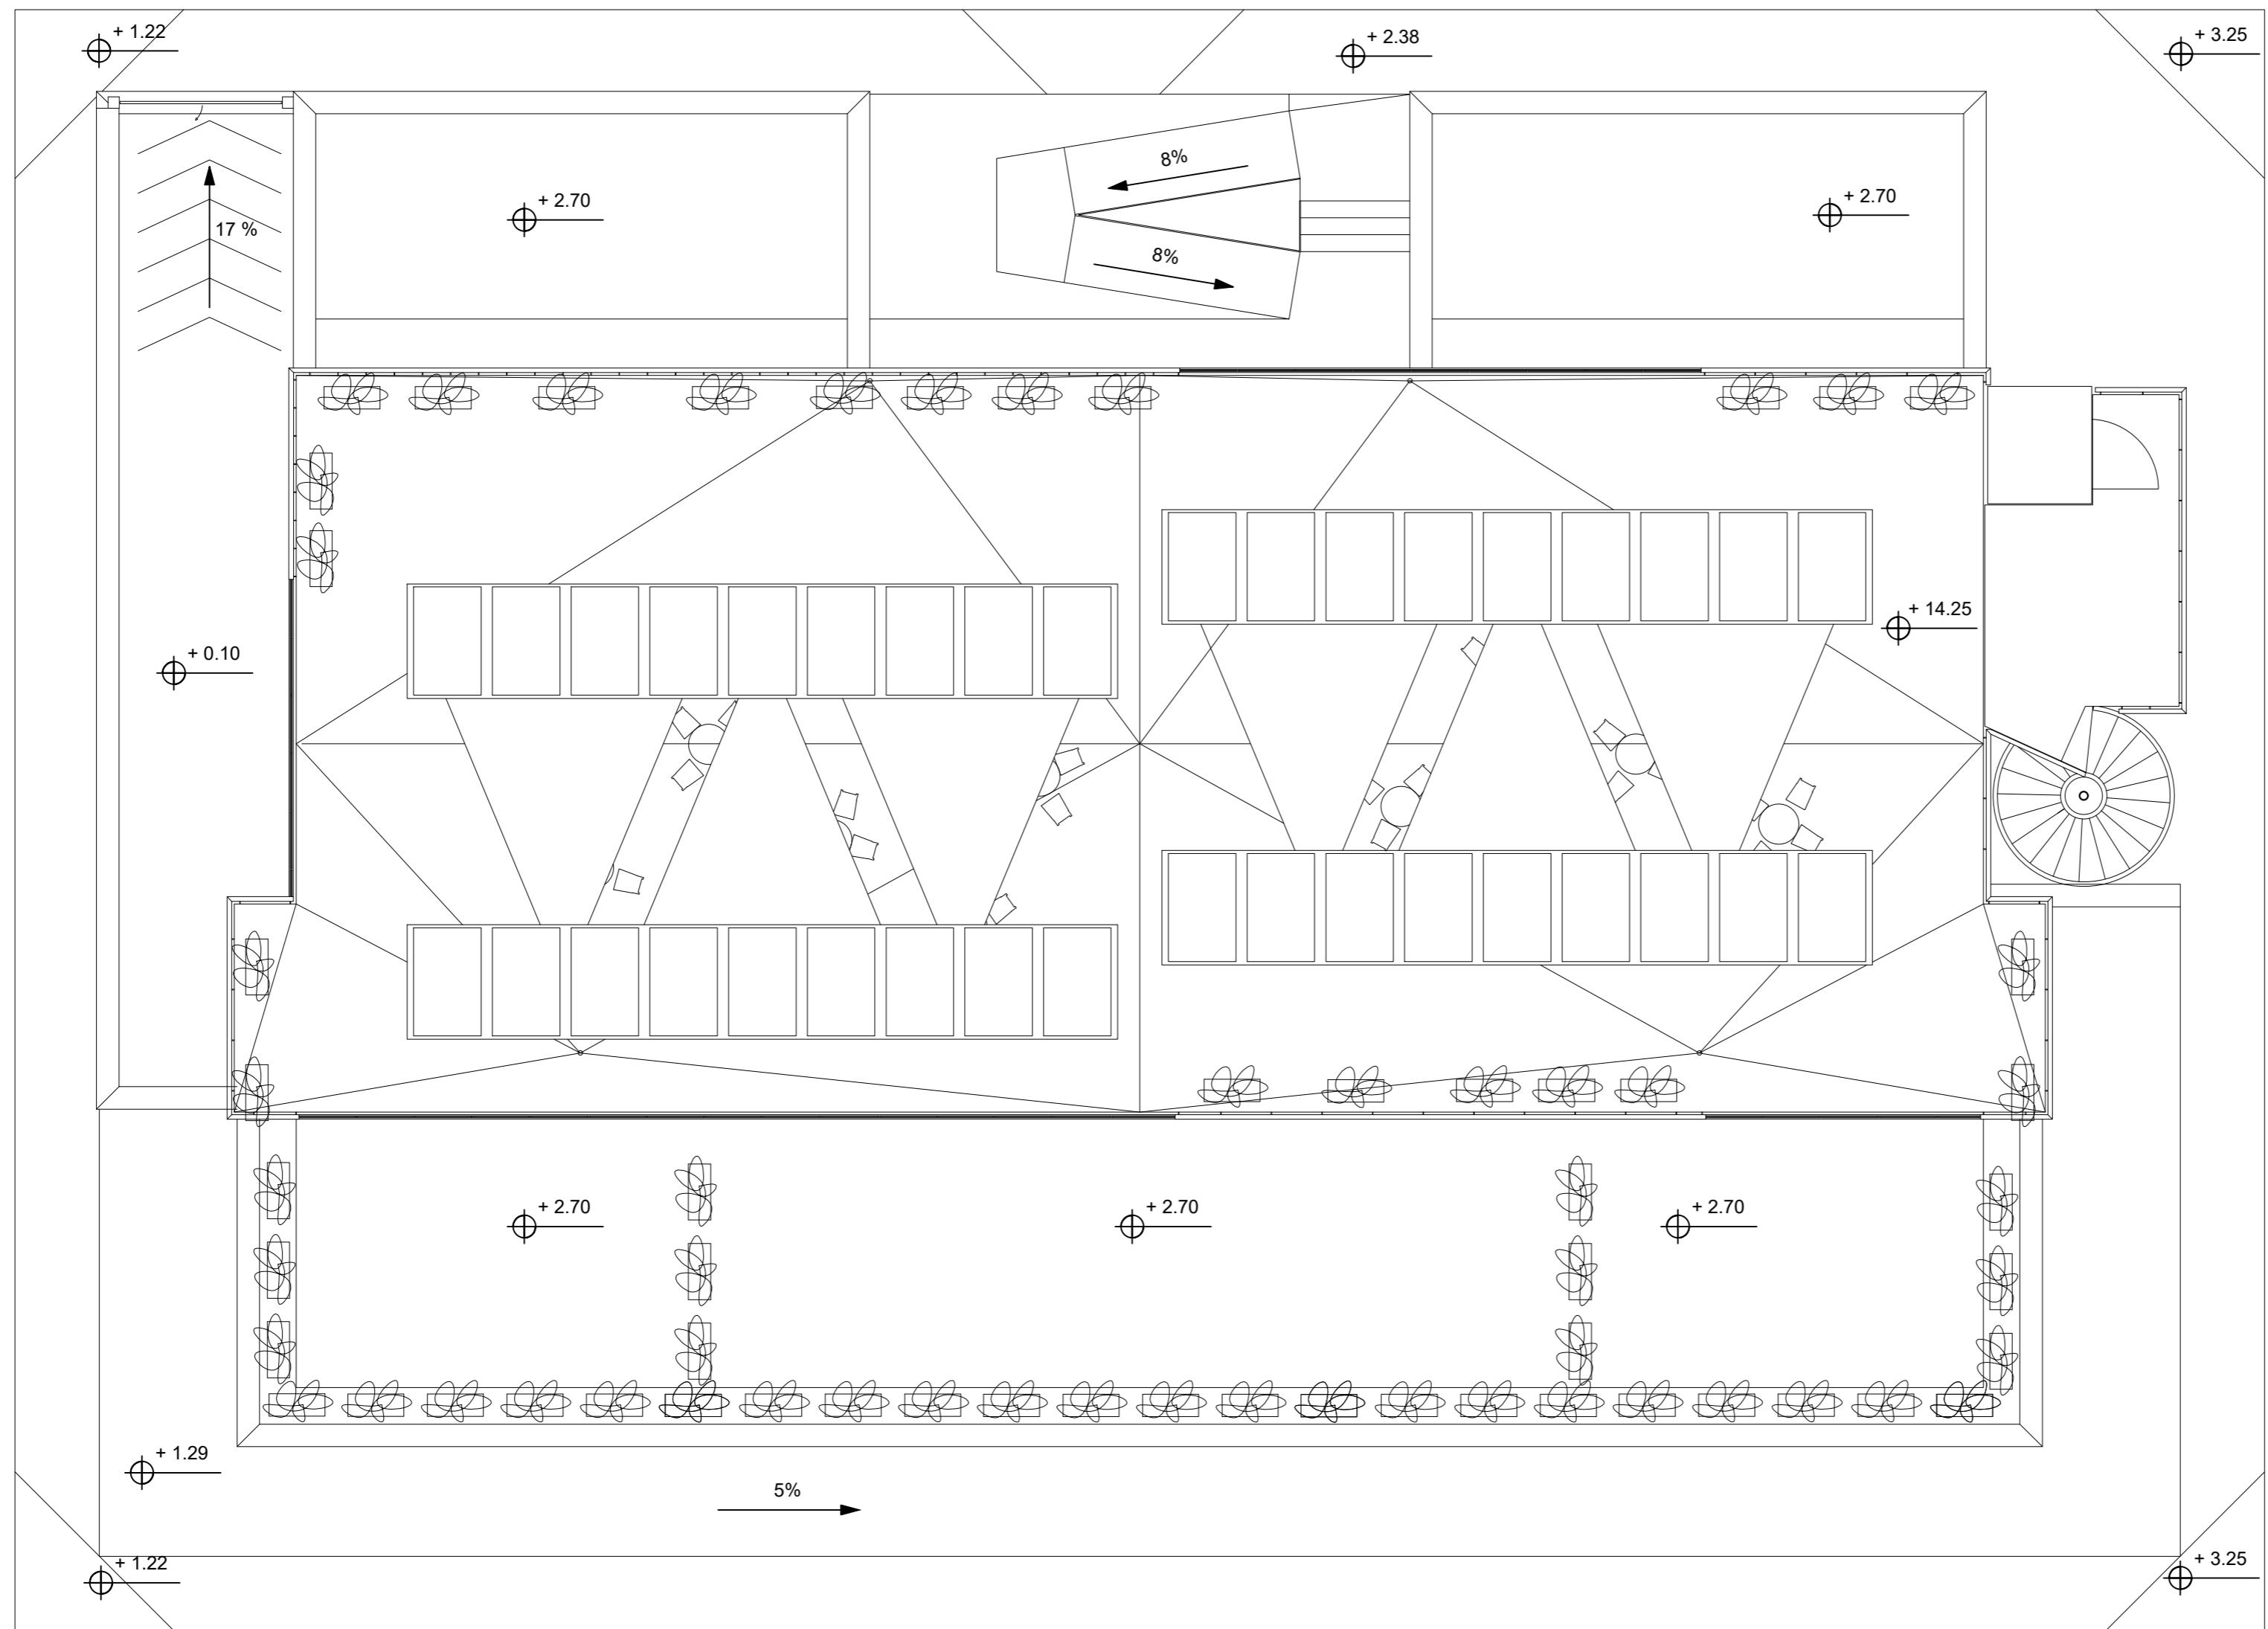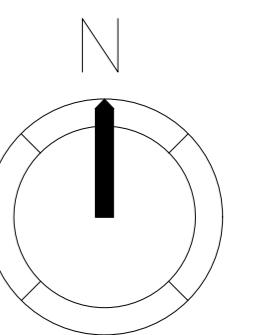

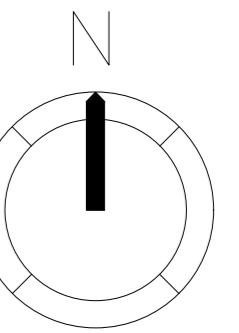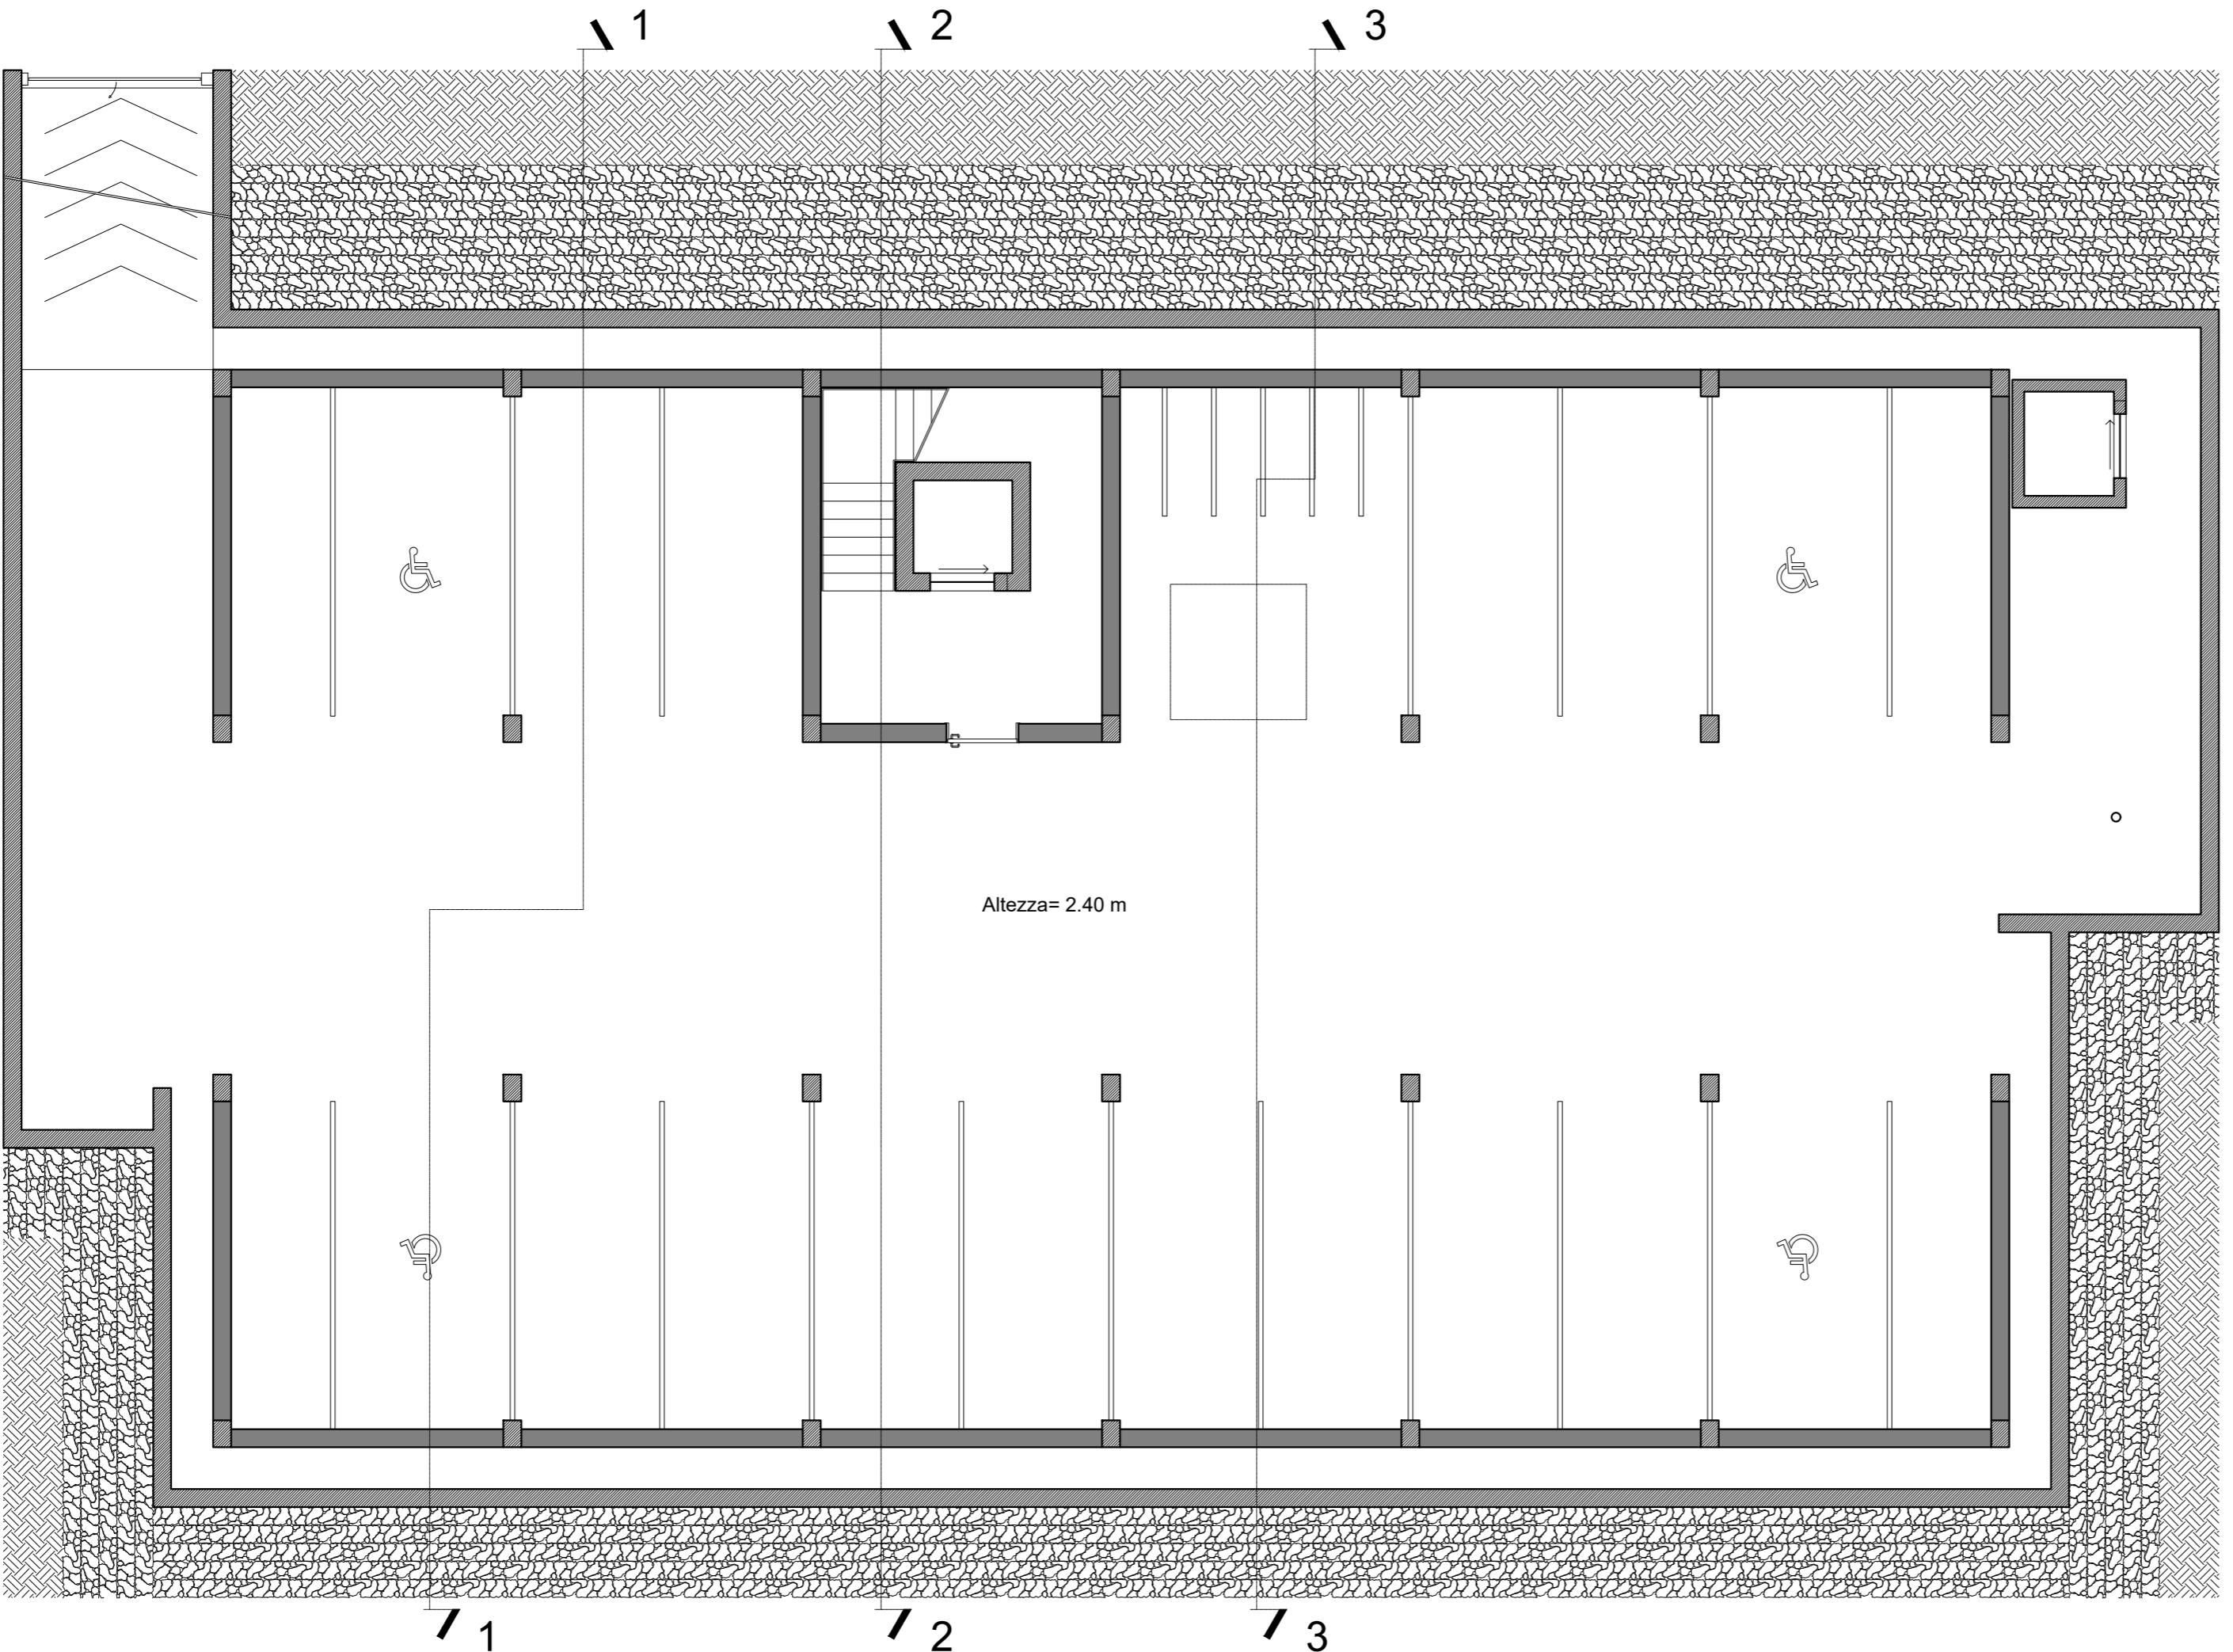



Università degli Studi di Catania

Dipartimento di Ingegneria Civile e Architettura

Corso di Laurea in Ingegneria Edile e Architettura

ARCHITETTURA TECNICA II E LABORATORIO
PROGETTUALE a.a. 2019-2020



Docenti: Vincenzo Sapienza, Gaetano Sciuto
Gruppo: Andrea Longhitano, Francesco Lomeo,
Giovanni Terranova

Progetto di un edificio a destinazione
residenziale e commerciale

PIANTA PIANO TERRA

TAVOLA 4


Scala 1:100

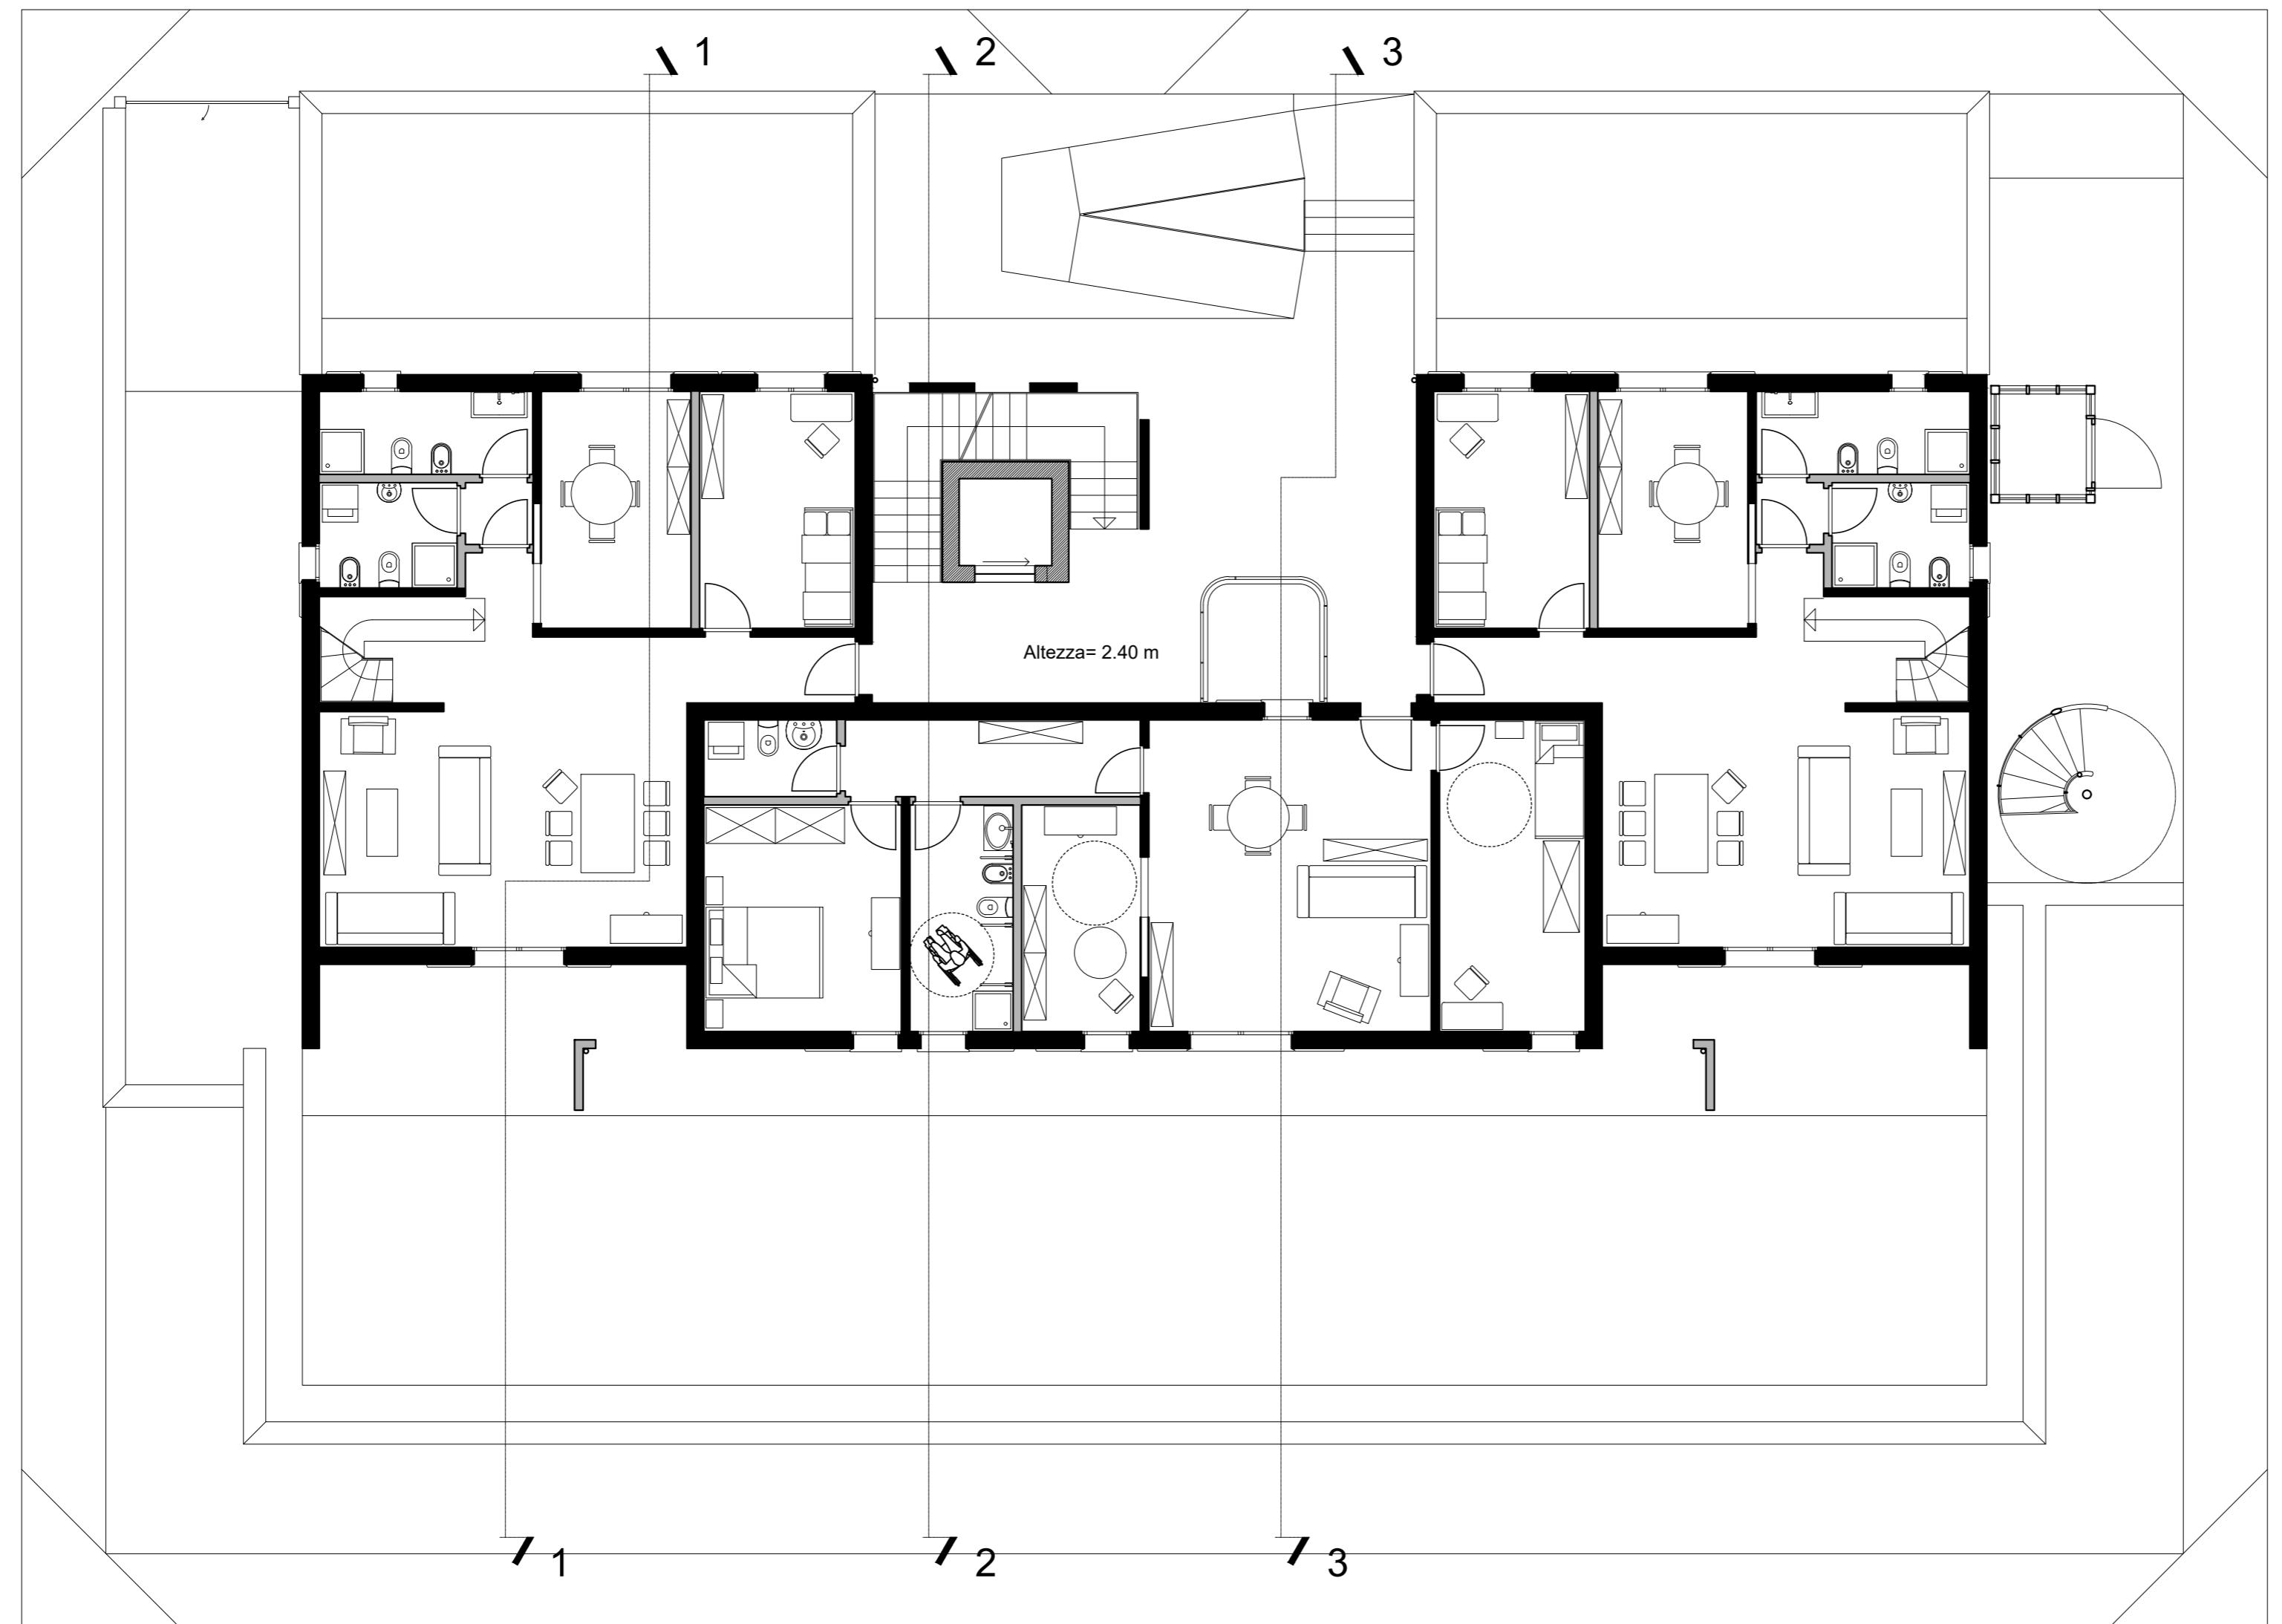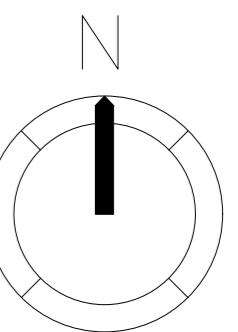

PIANTA PIANO PRIMO

TAVOLA 5



Scala 1:100

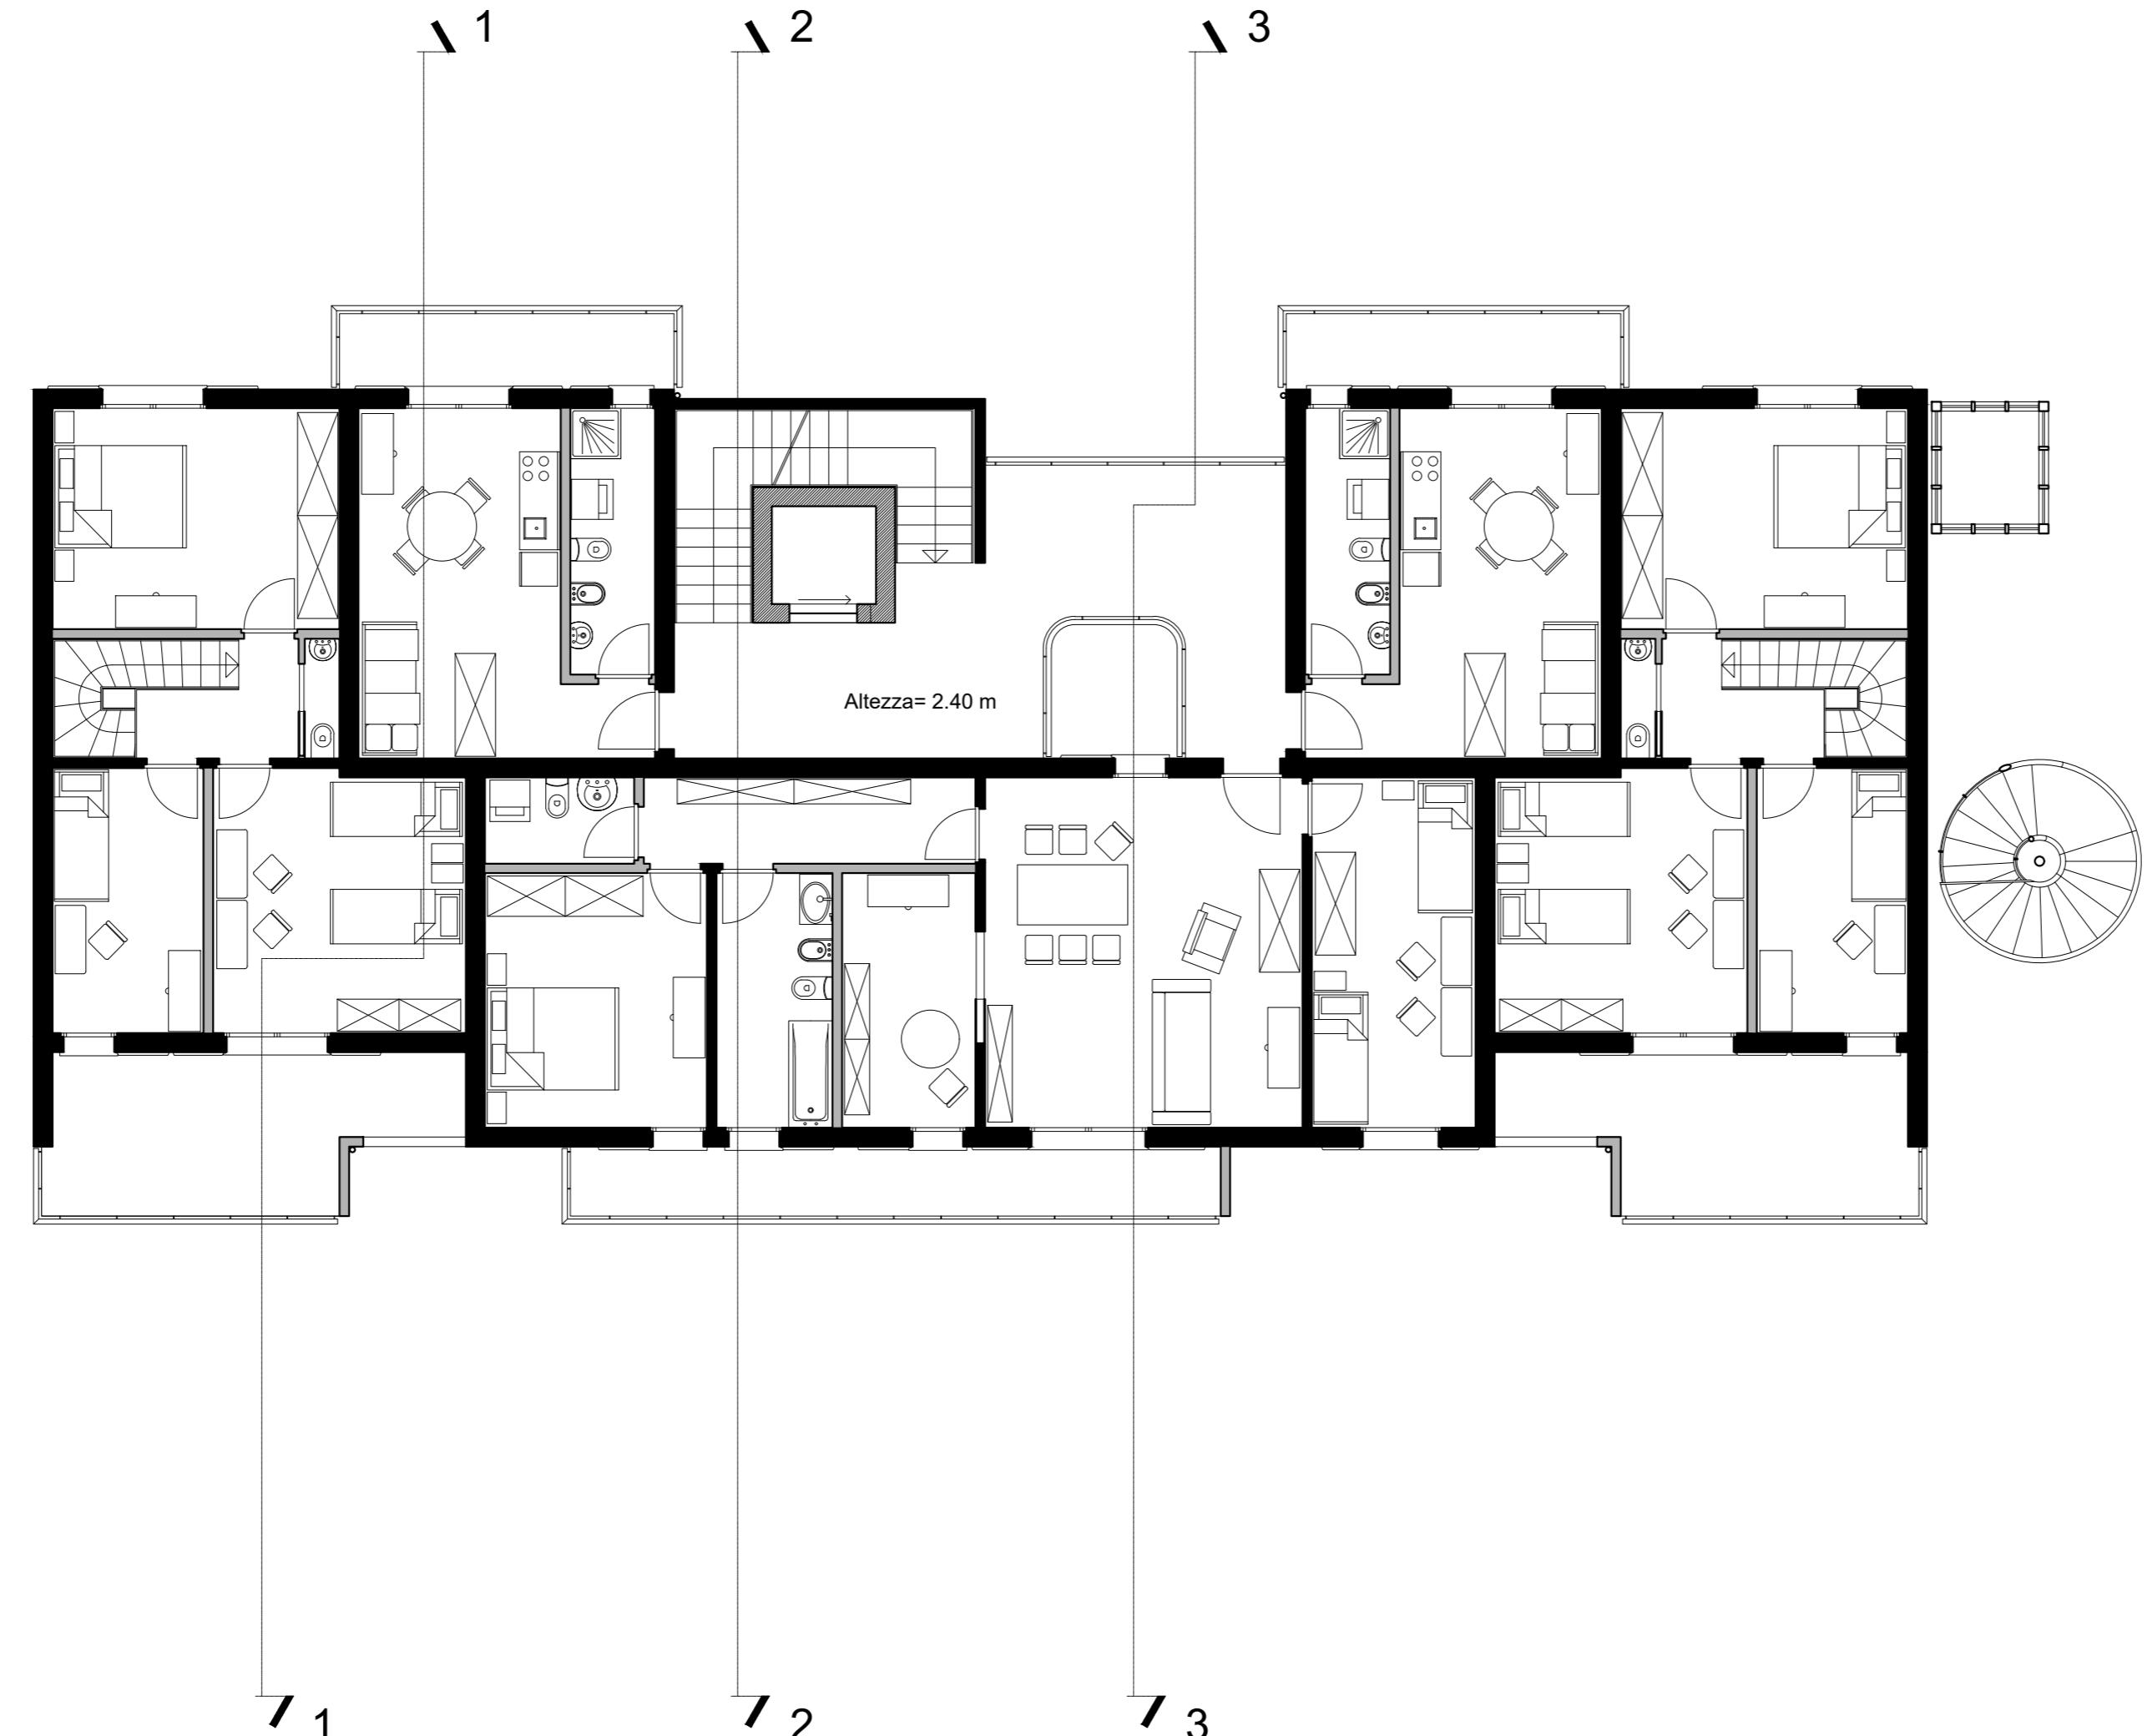

PIANTA PIANO SECONDO

TAVOLA 6



Scala 1:100

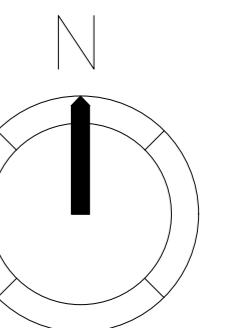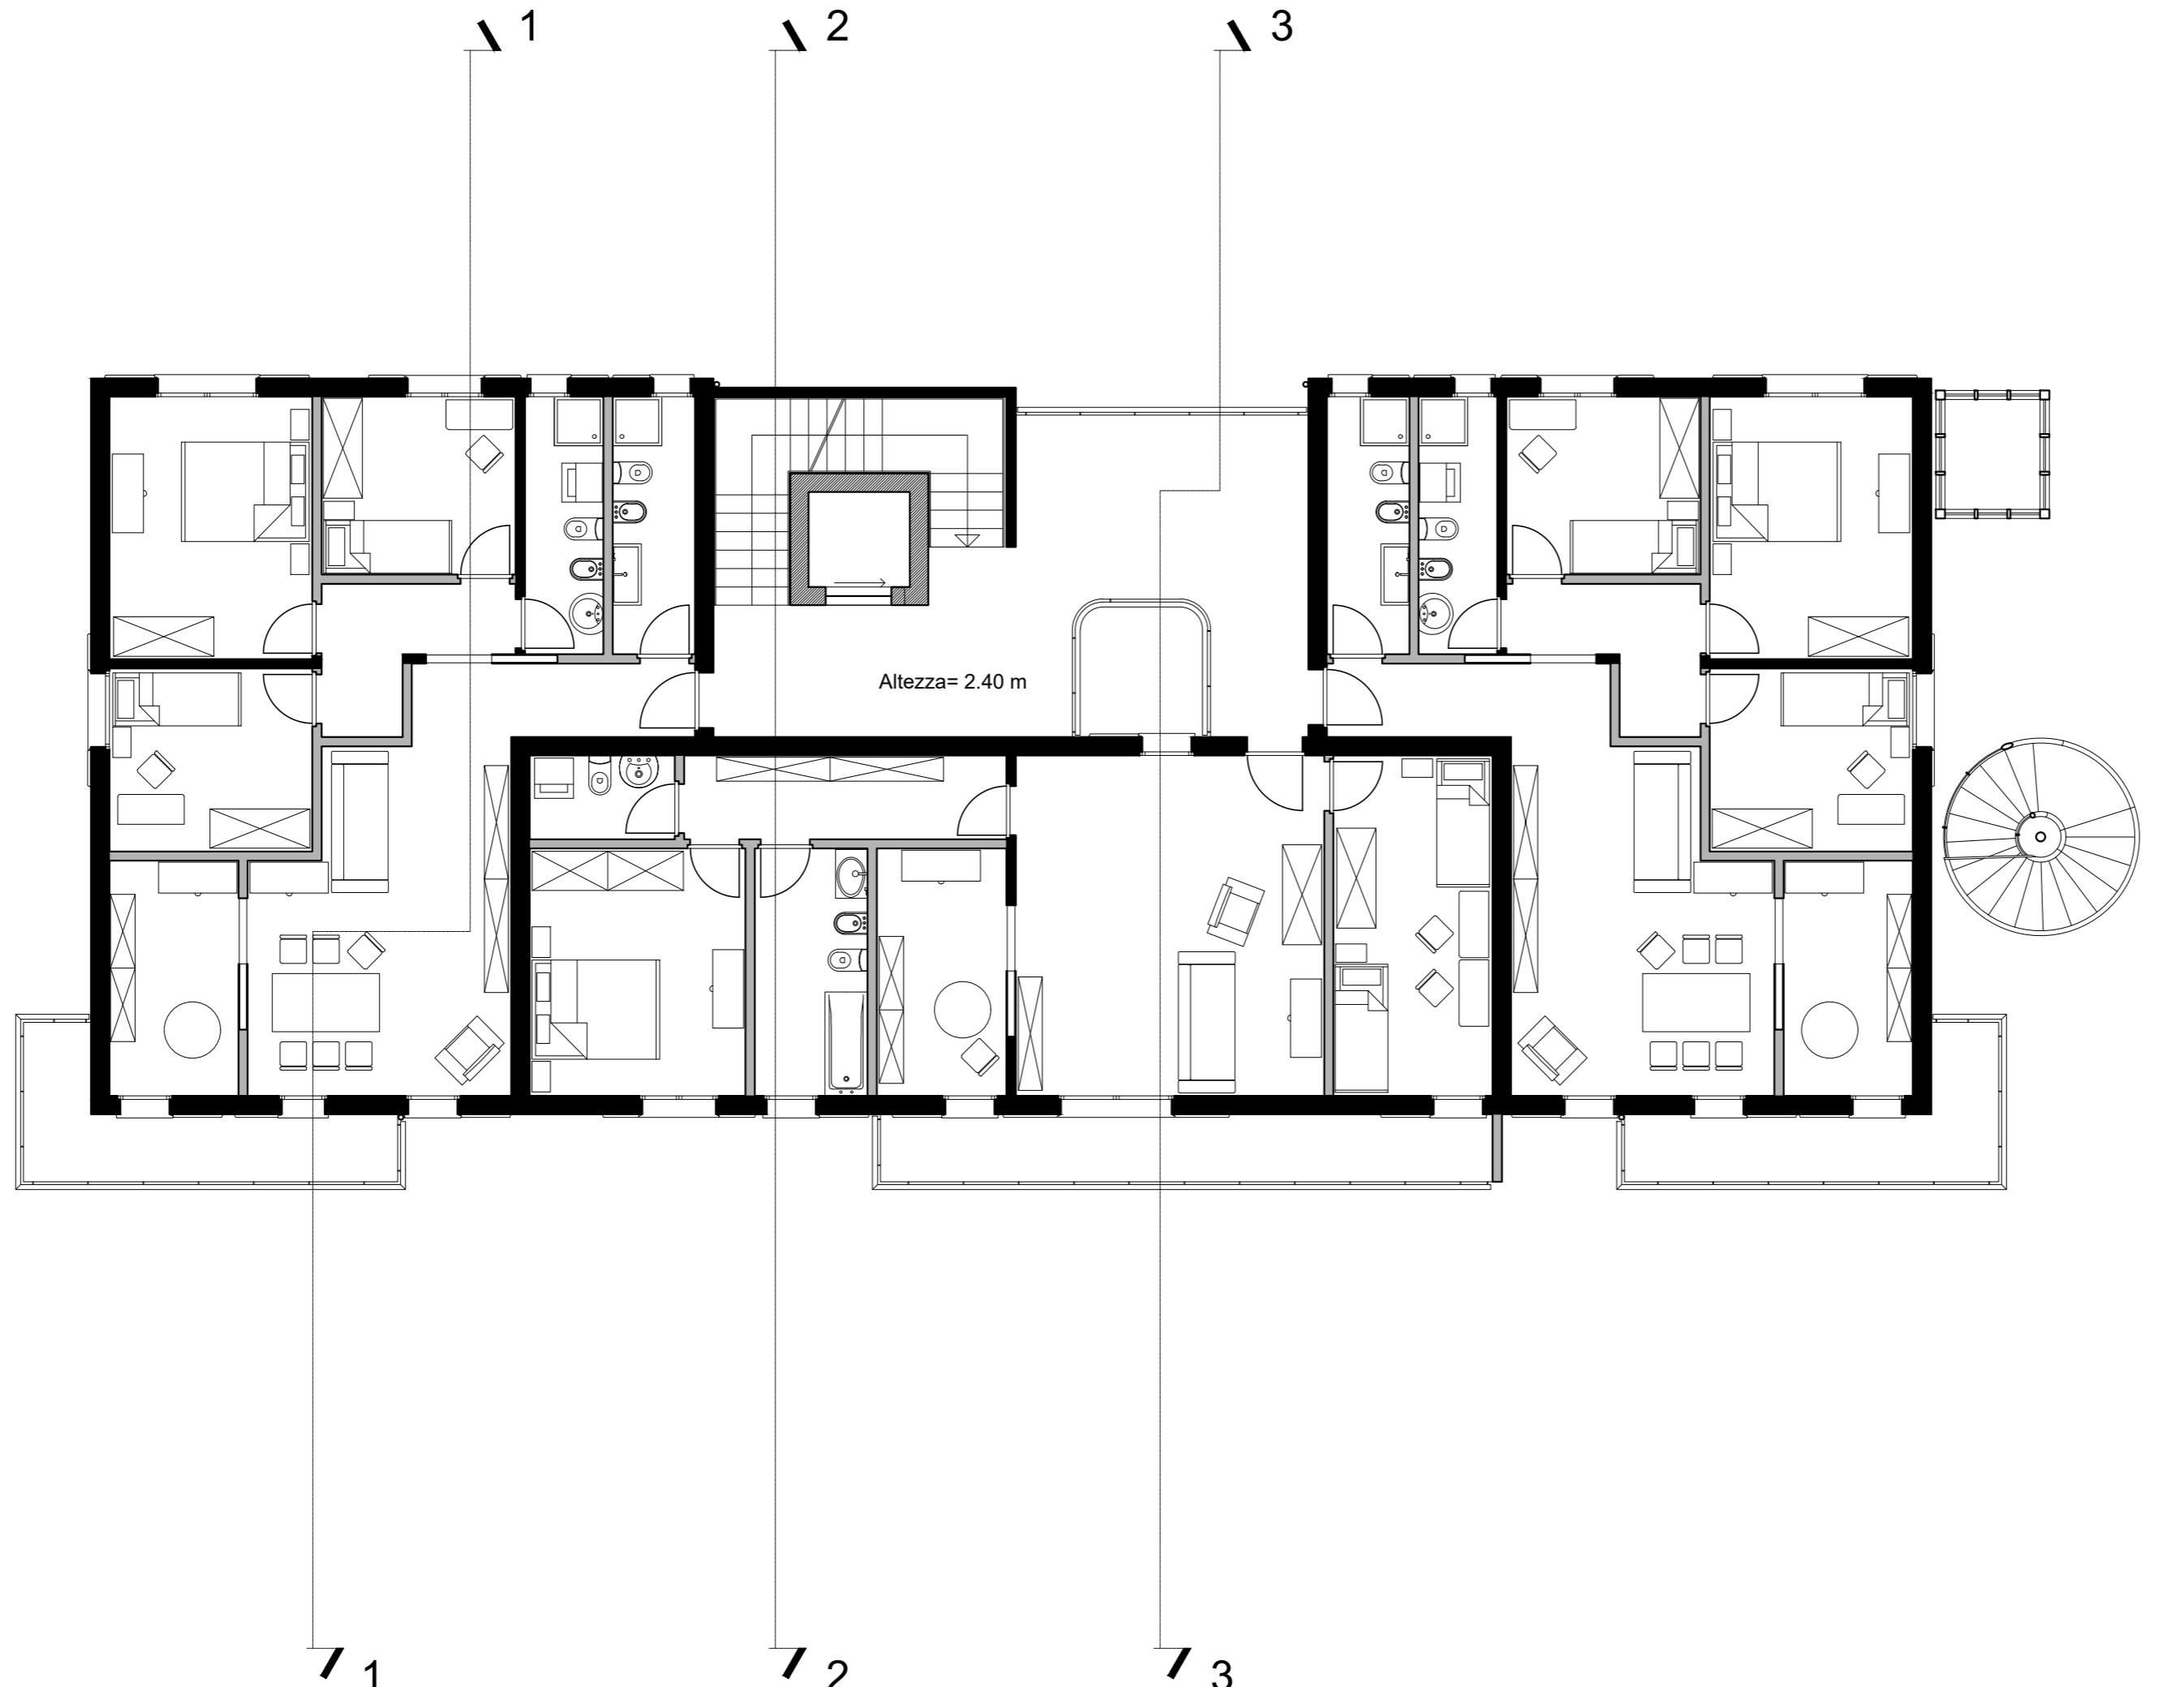

PIANTA PIANO TERZO

TAVOLA 7



Scala 1:100

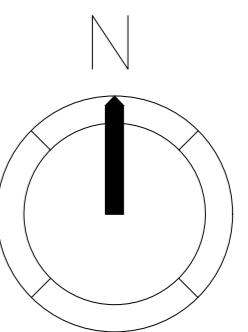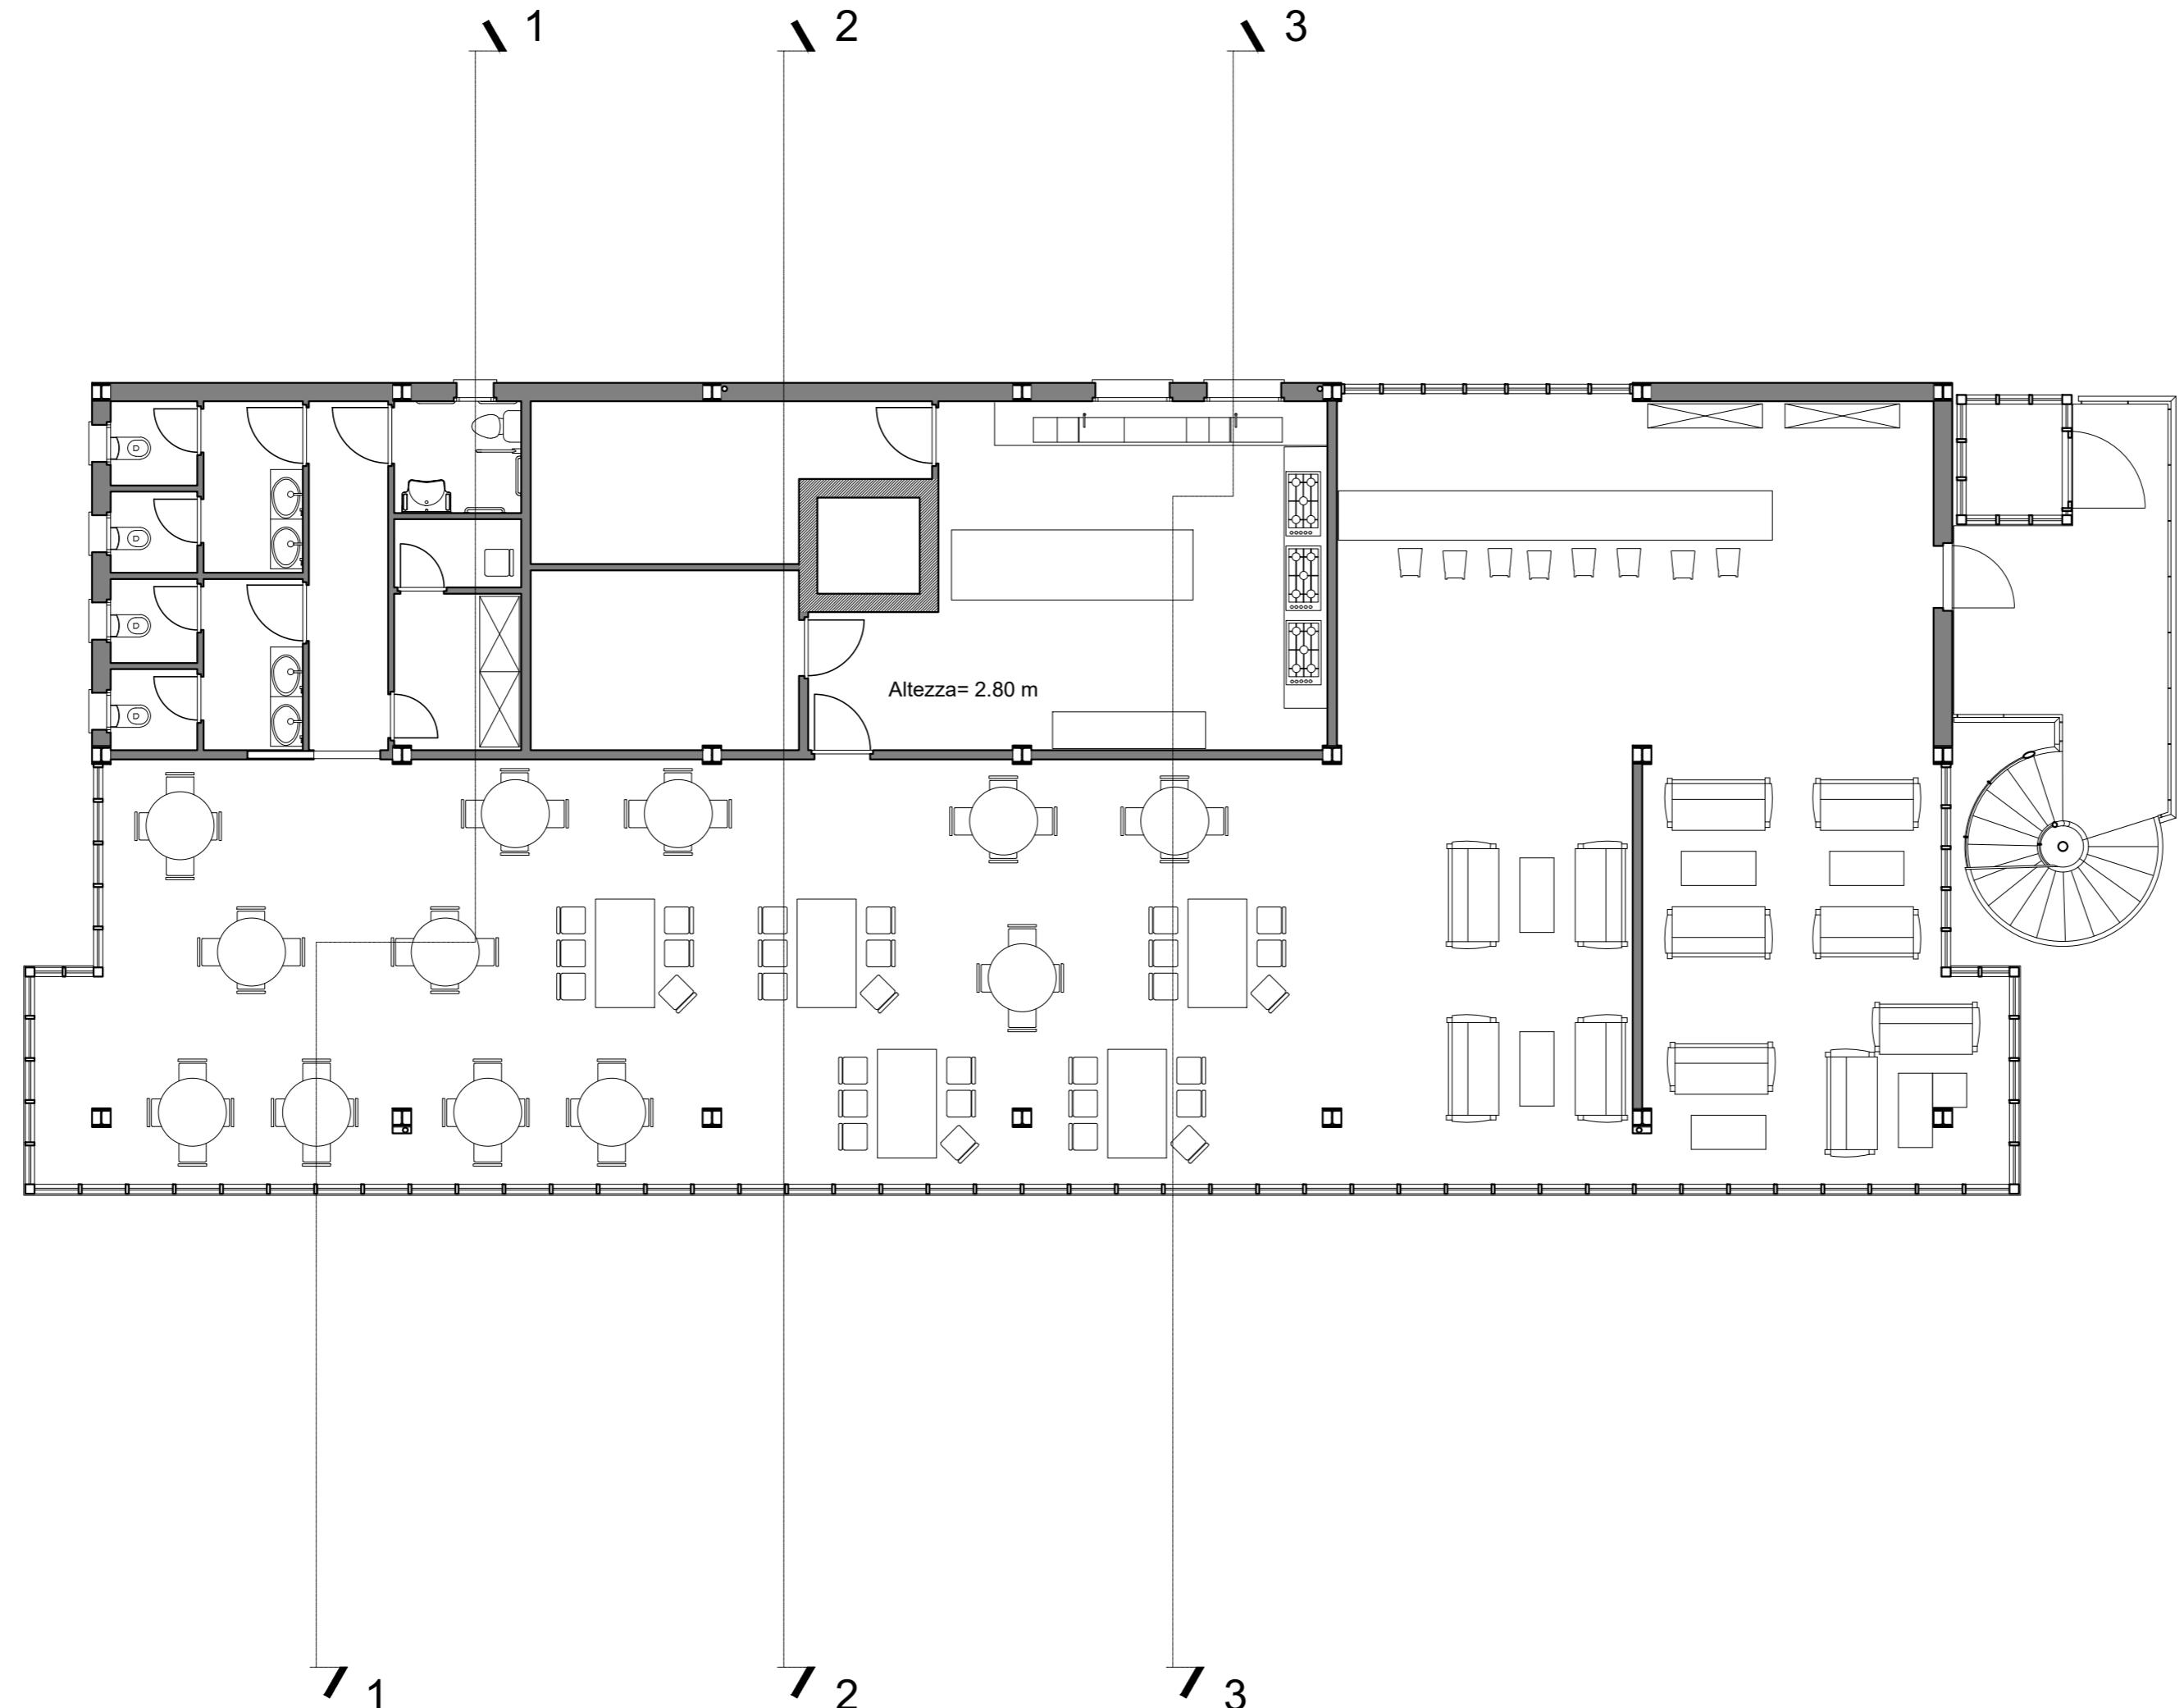

PIANTA TERRAZZO

TAVOLA 8



Scala 1:100

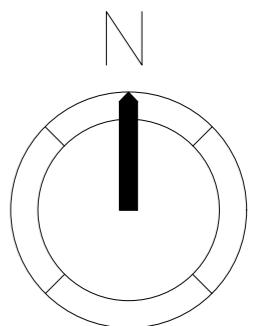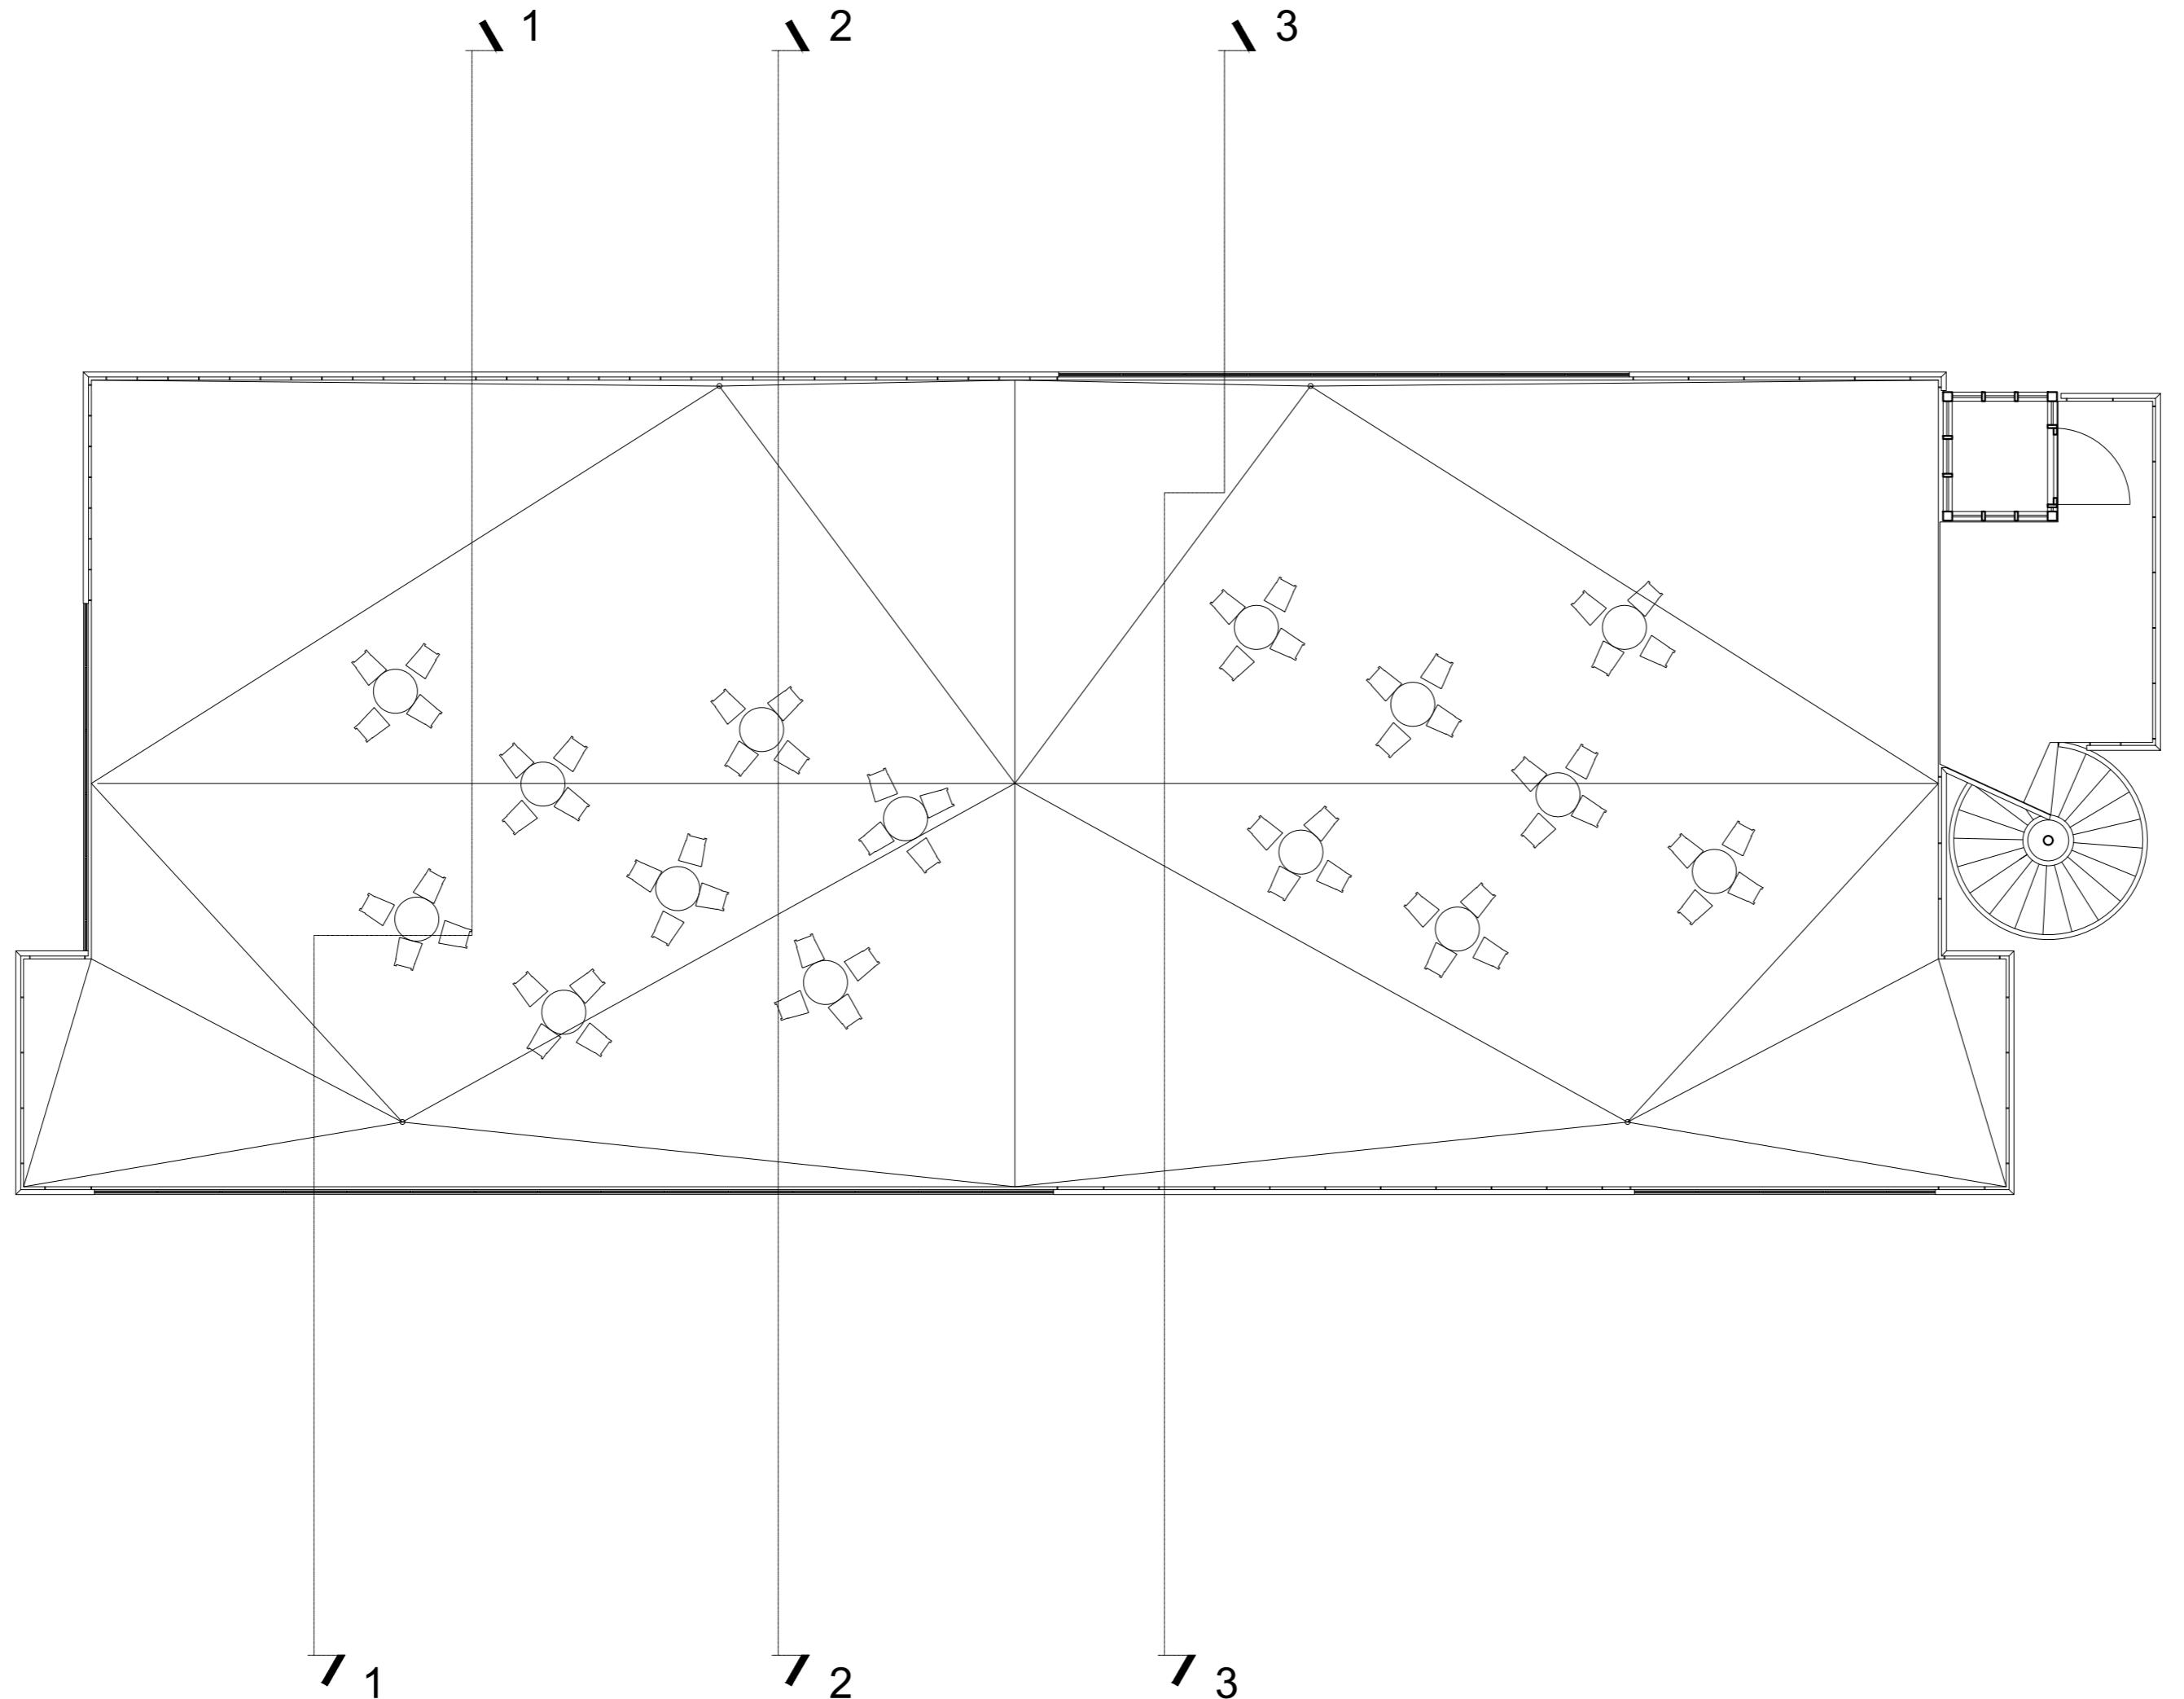

PIANTA COPERTURE

TAVOLA 9

Scala 1:100

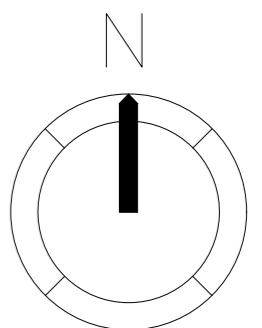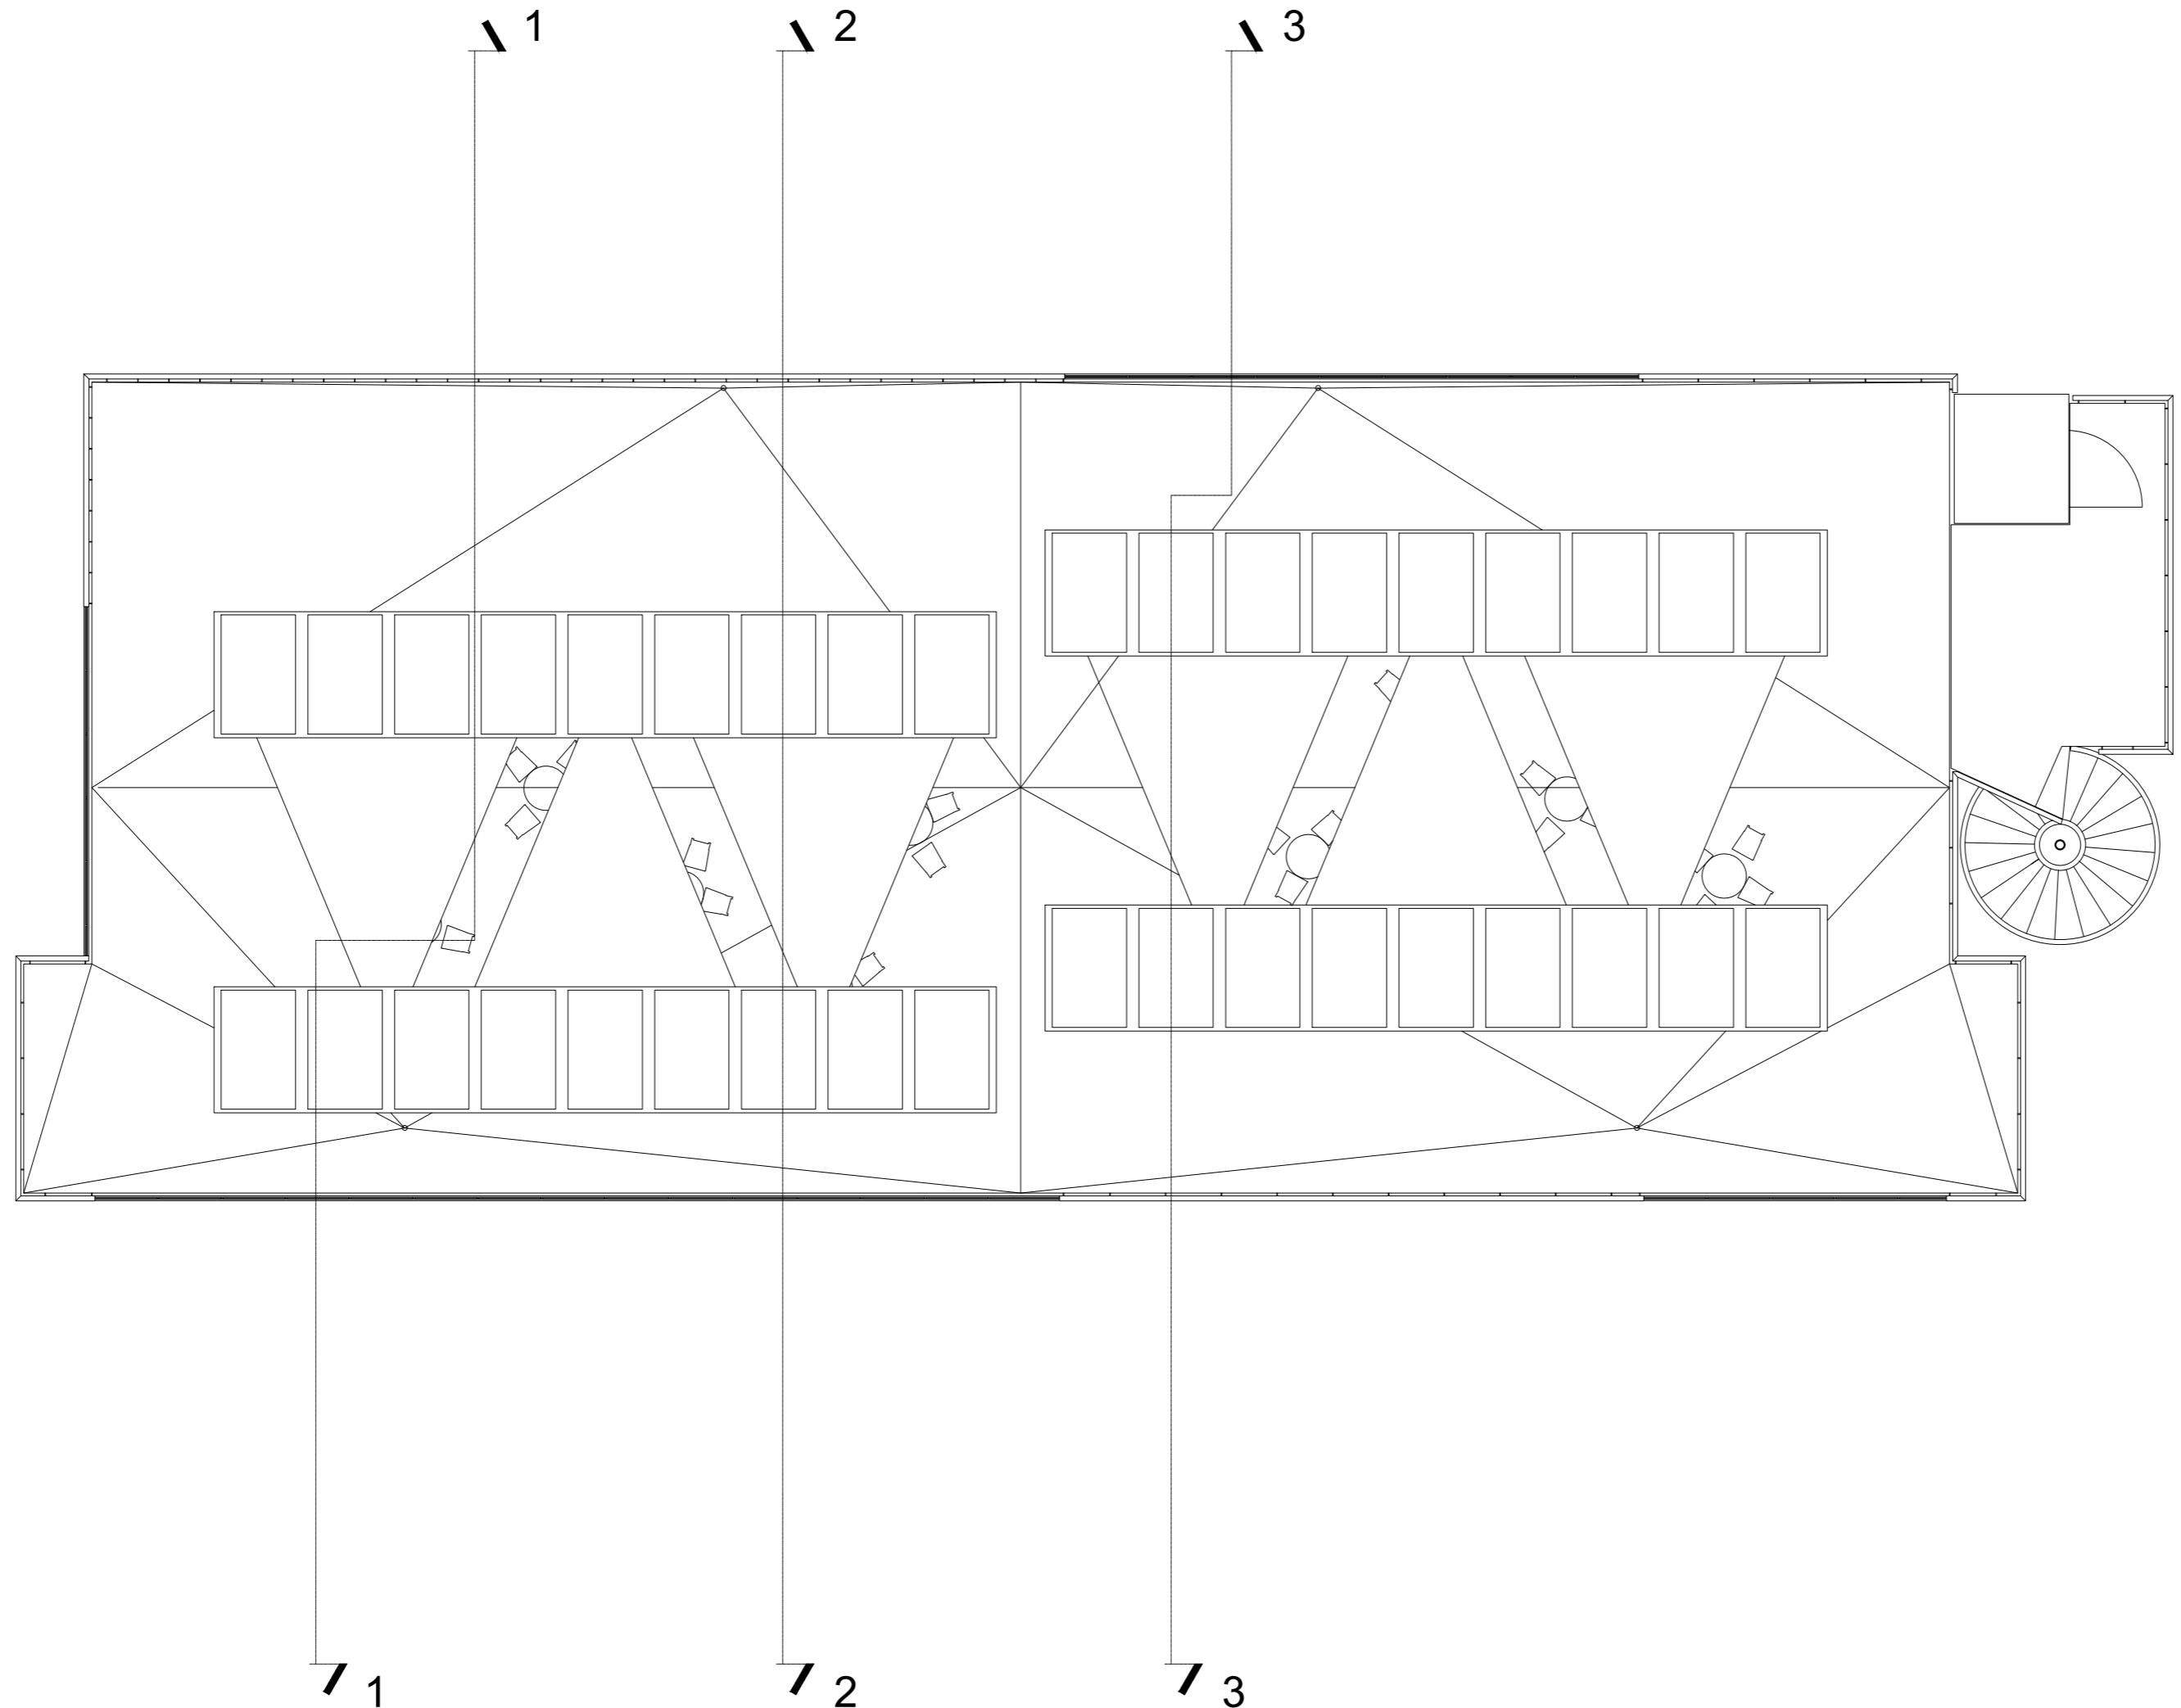



Università degli Studi di Catania

Dipartimento di Ingegneria Civile e Architettura
Corso di Laurea in Ingegneria Edile e Architettura

ARCHITETTURA TECNICA II E LABORATORIO
PROGETTUALE a.a. 2019-2020


Docenti: Vincenzo Sapienza, Gaetano Sciuto
Gruppo: Andrea Longhitano, Frenacesco Lomeo,
Giovanni Terranova

Progetto di un edificio a destinazione
residenziale e commerciale

PROSPETTO EST

TAVOLA 10



Scala 1:100

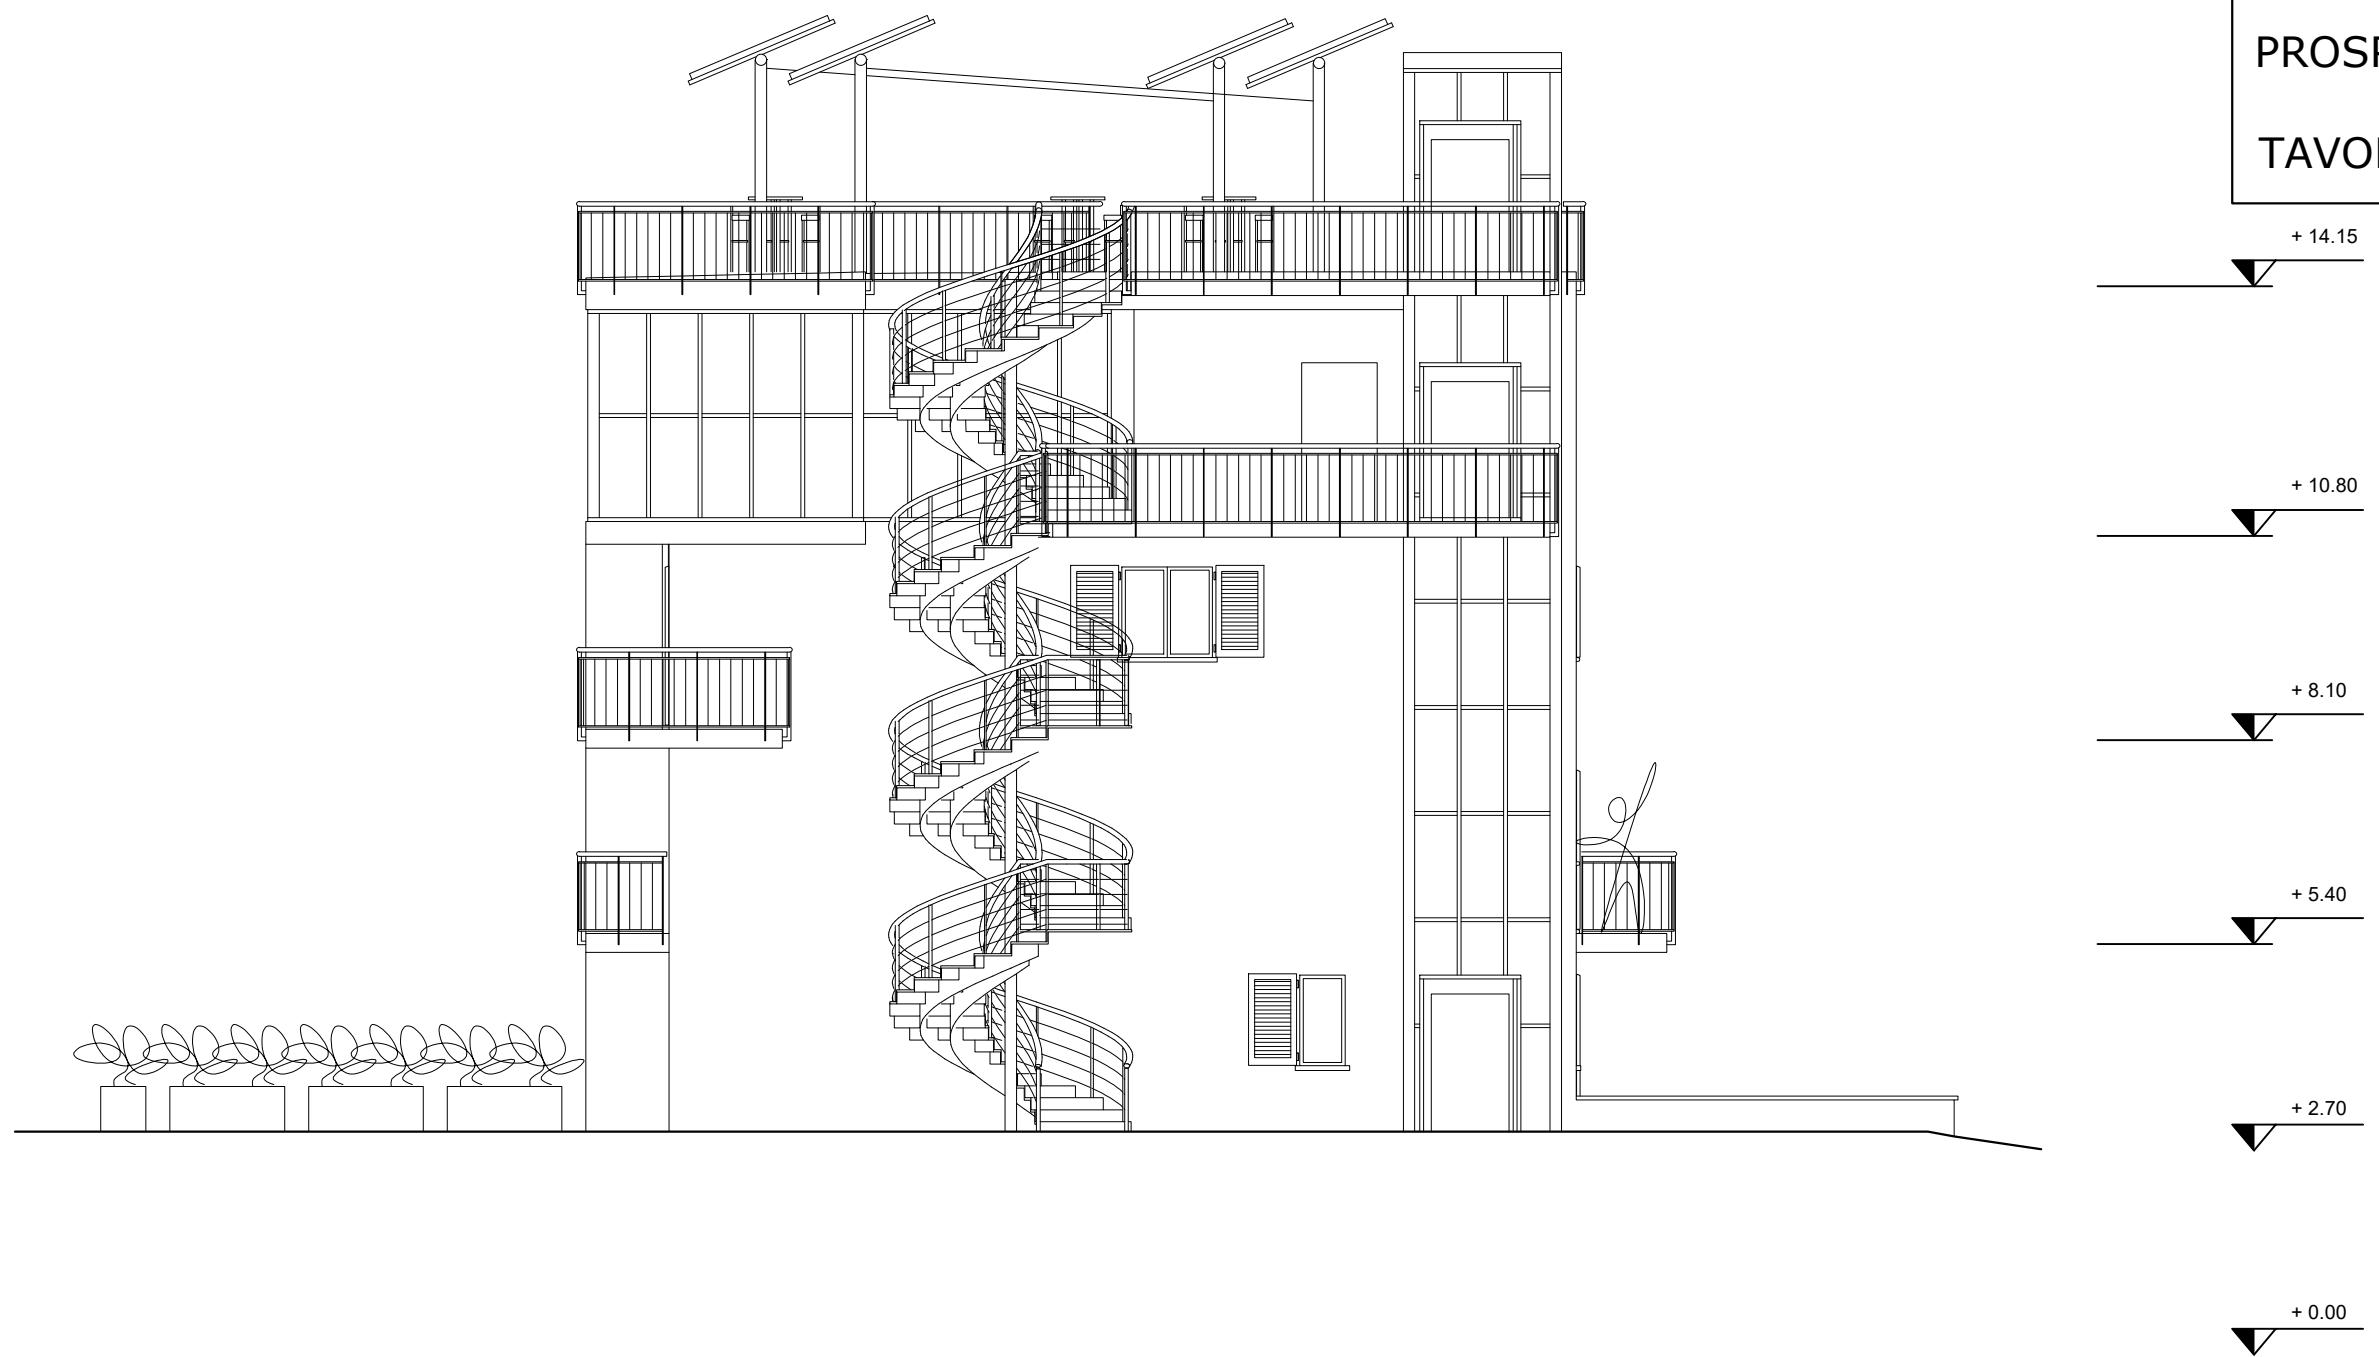

PROSPETTO NORD

TAVOLA 11

Scala 1:100

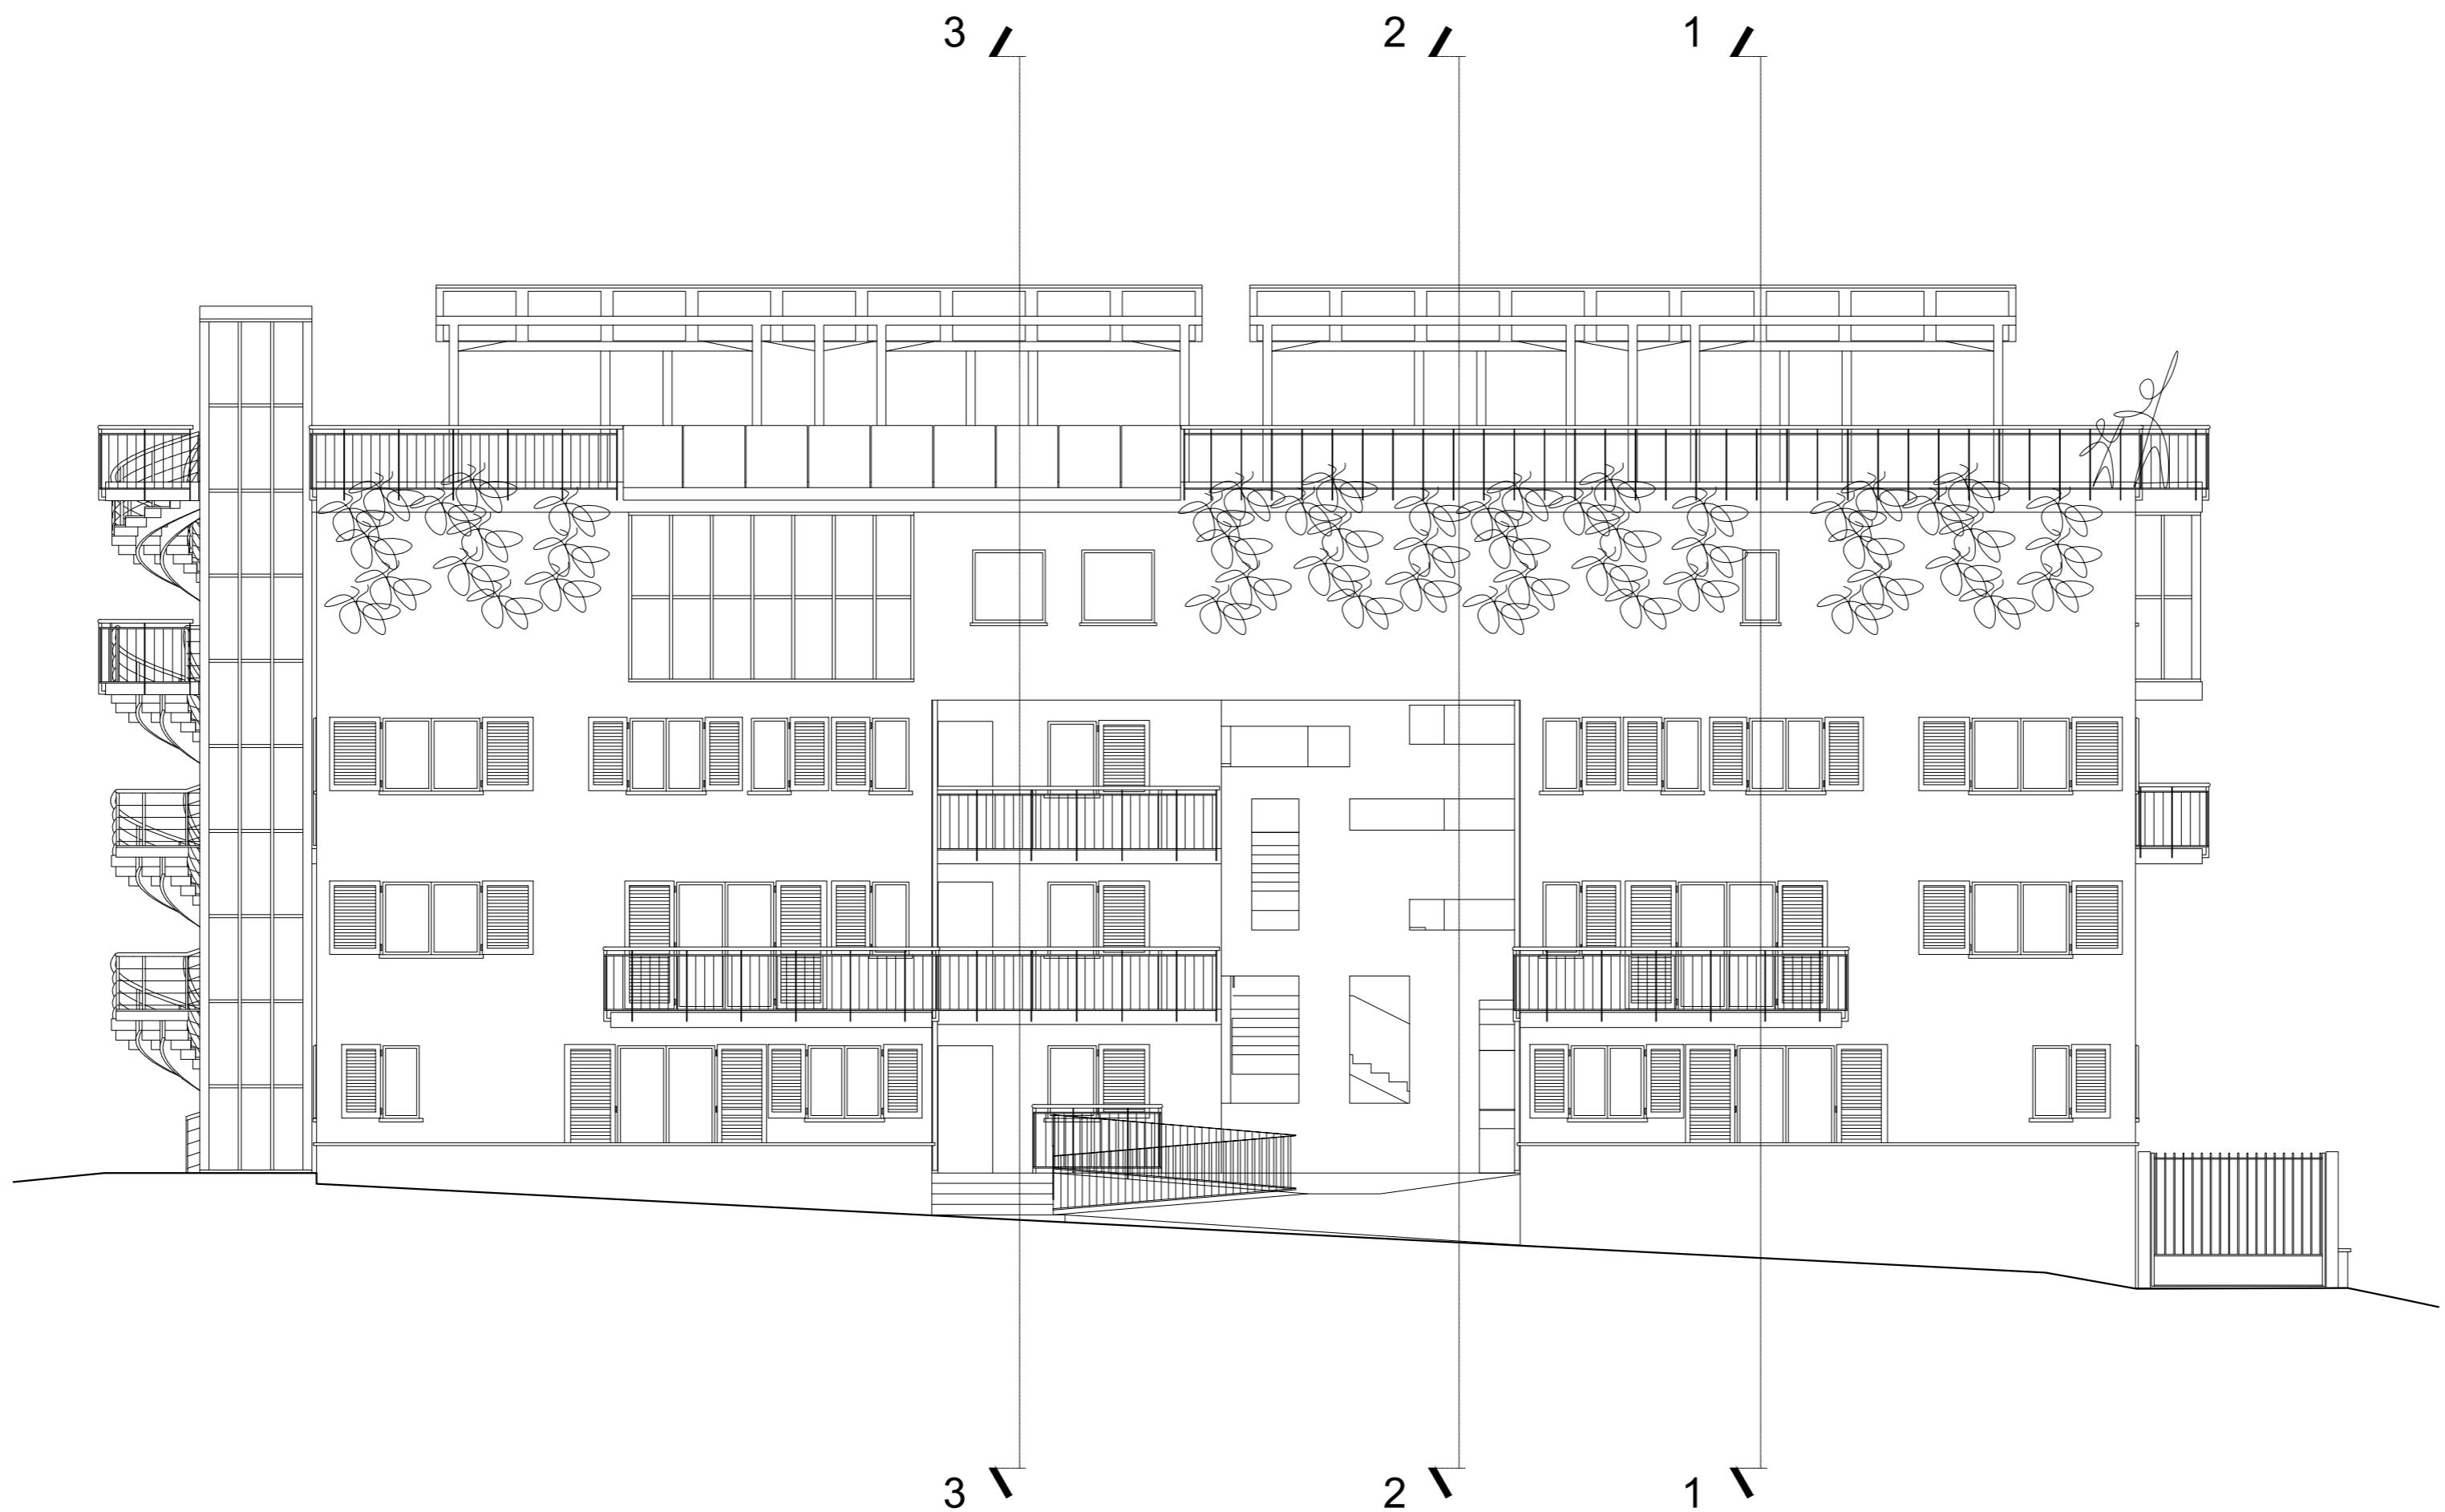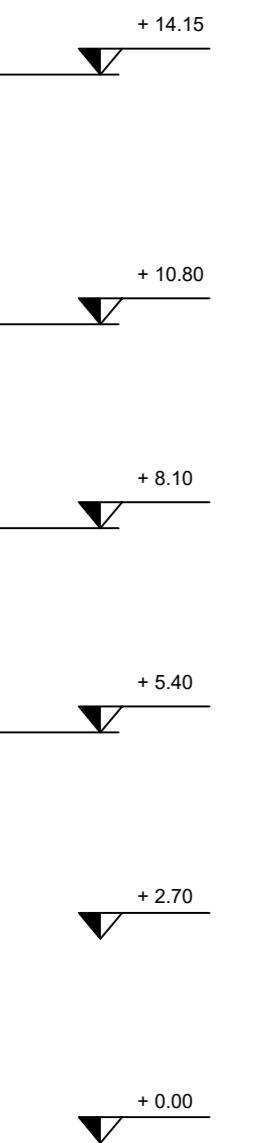



Università degli Studi di Catania

Dipartimento di Ingegneria Civile e Architettura
Corso di Laurea in Ingegneria Edile e Architettura

ARCHITETTURA TECNICA II E LABORATORIO
PROGETTUALE a.a. 2019-2020


Docenti: Vincenzo Sapienza, Gaetano Sciuto
Gruppo: Andrea Longhitano, Frenacesco Lomeo,
Giovanni Terranova

Progetto di un edificio a destinazione
residenziale e commerciale

PROSPETTO OVEST

TAVOLA 12


Scala 1:100

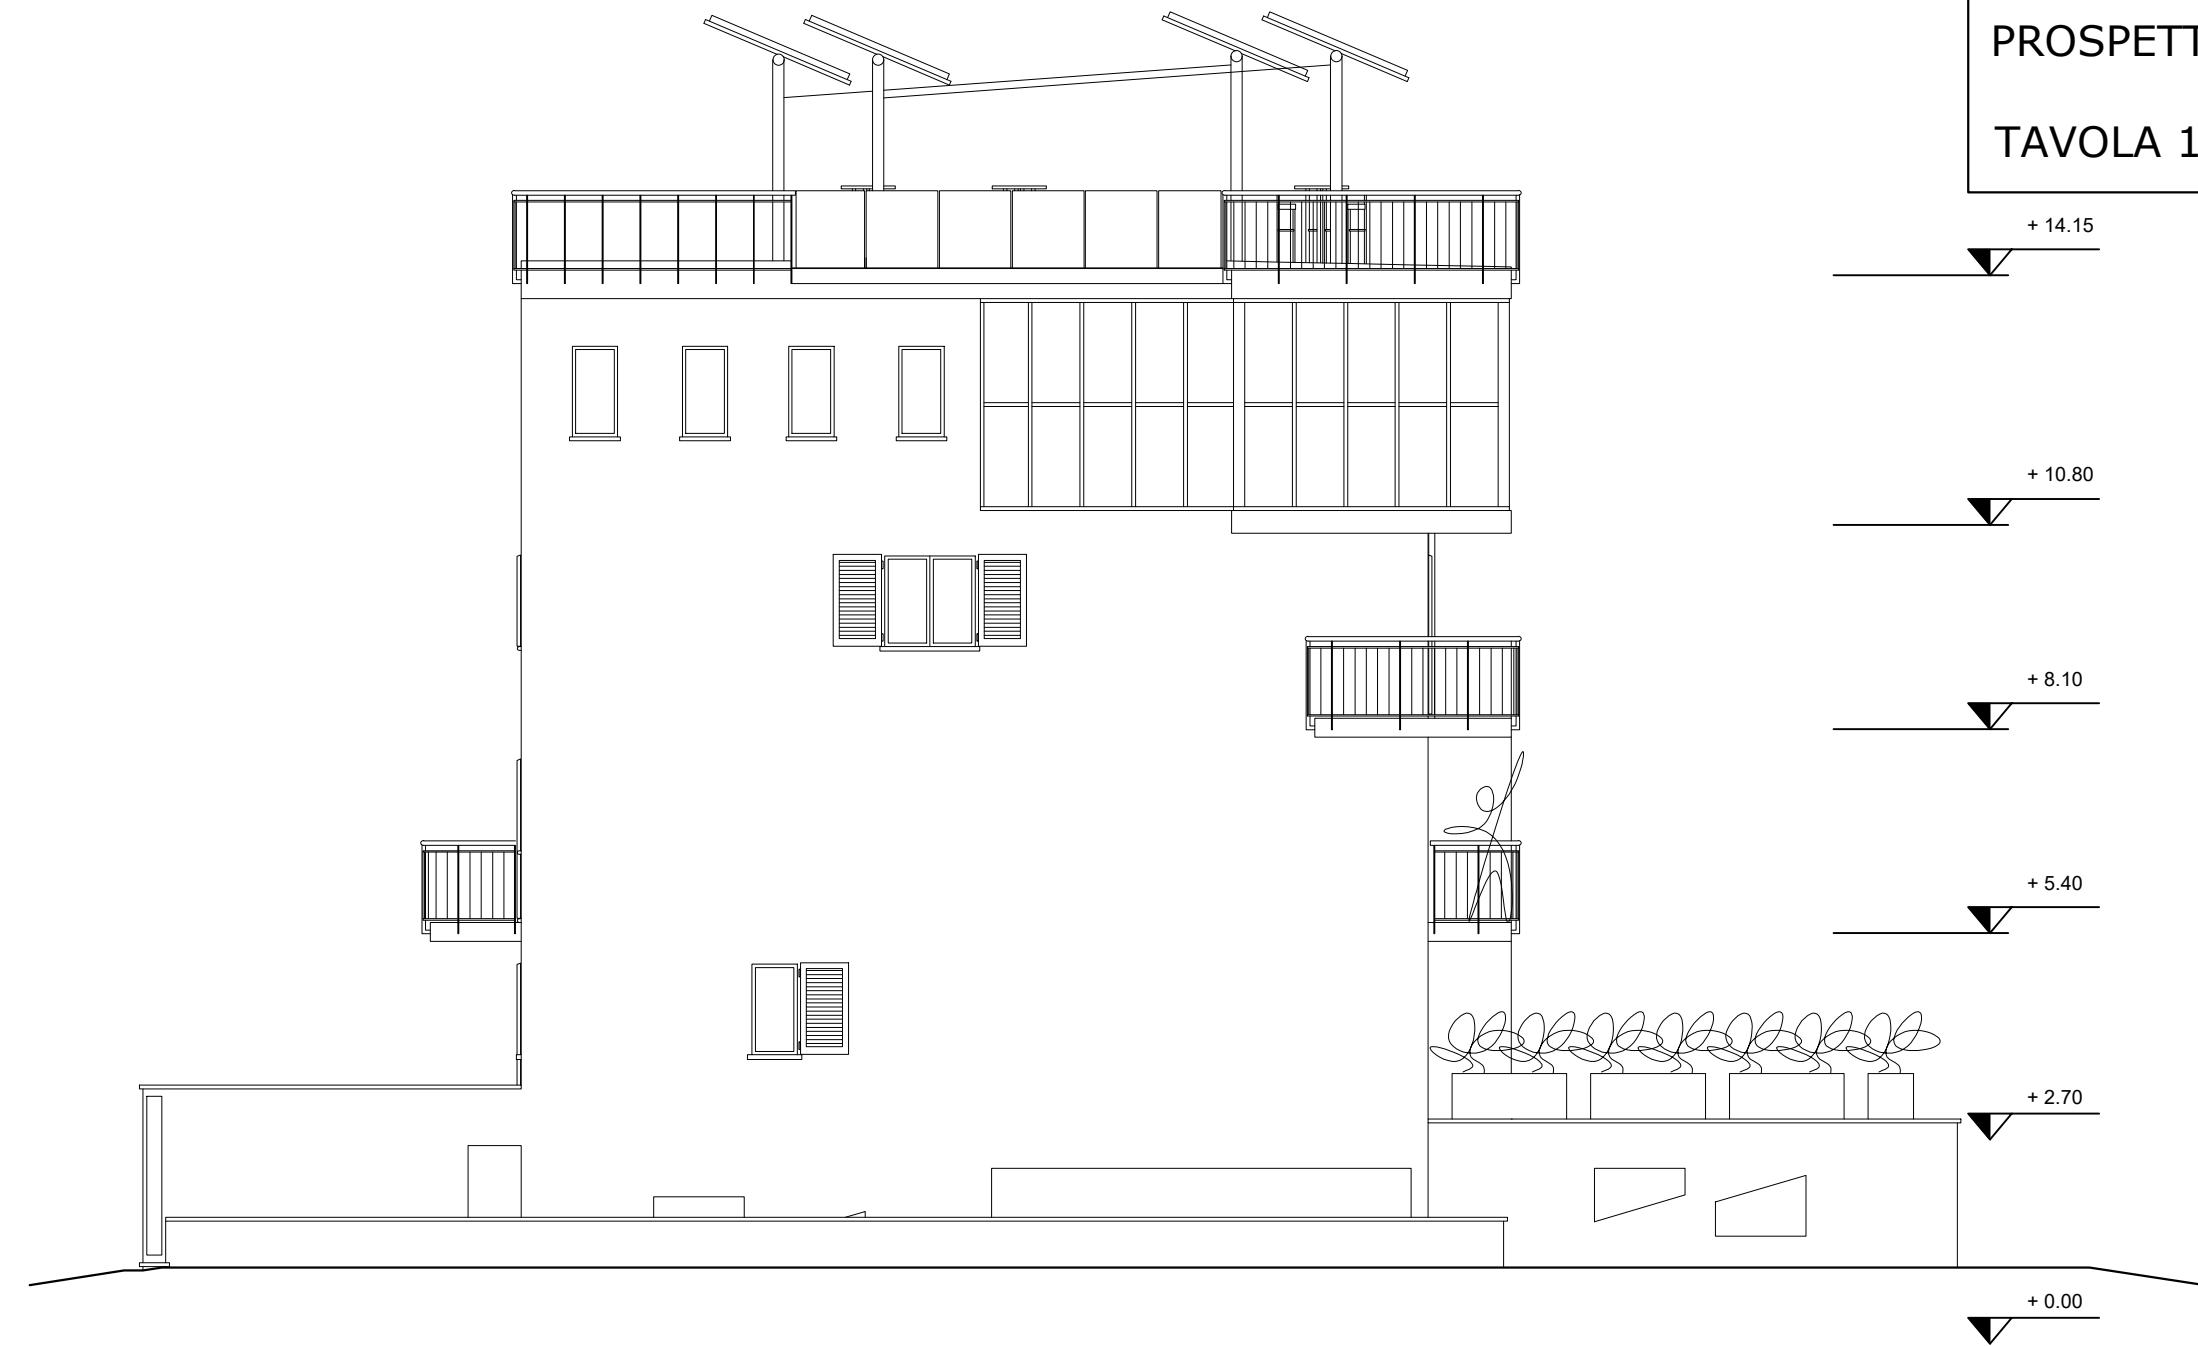

PROSPETTO SUD

TAVOLA 13

Scala 1:100

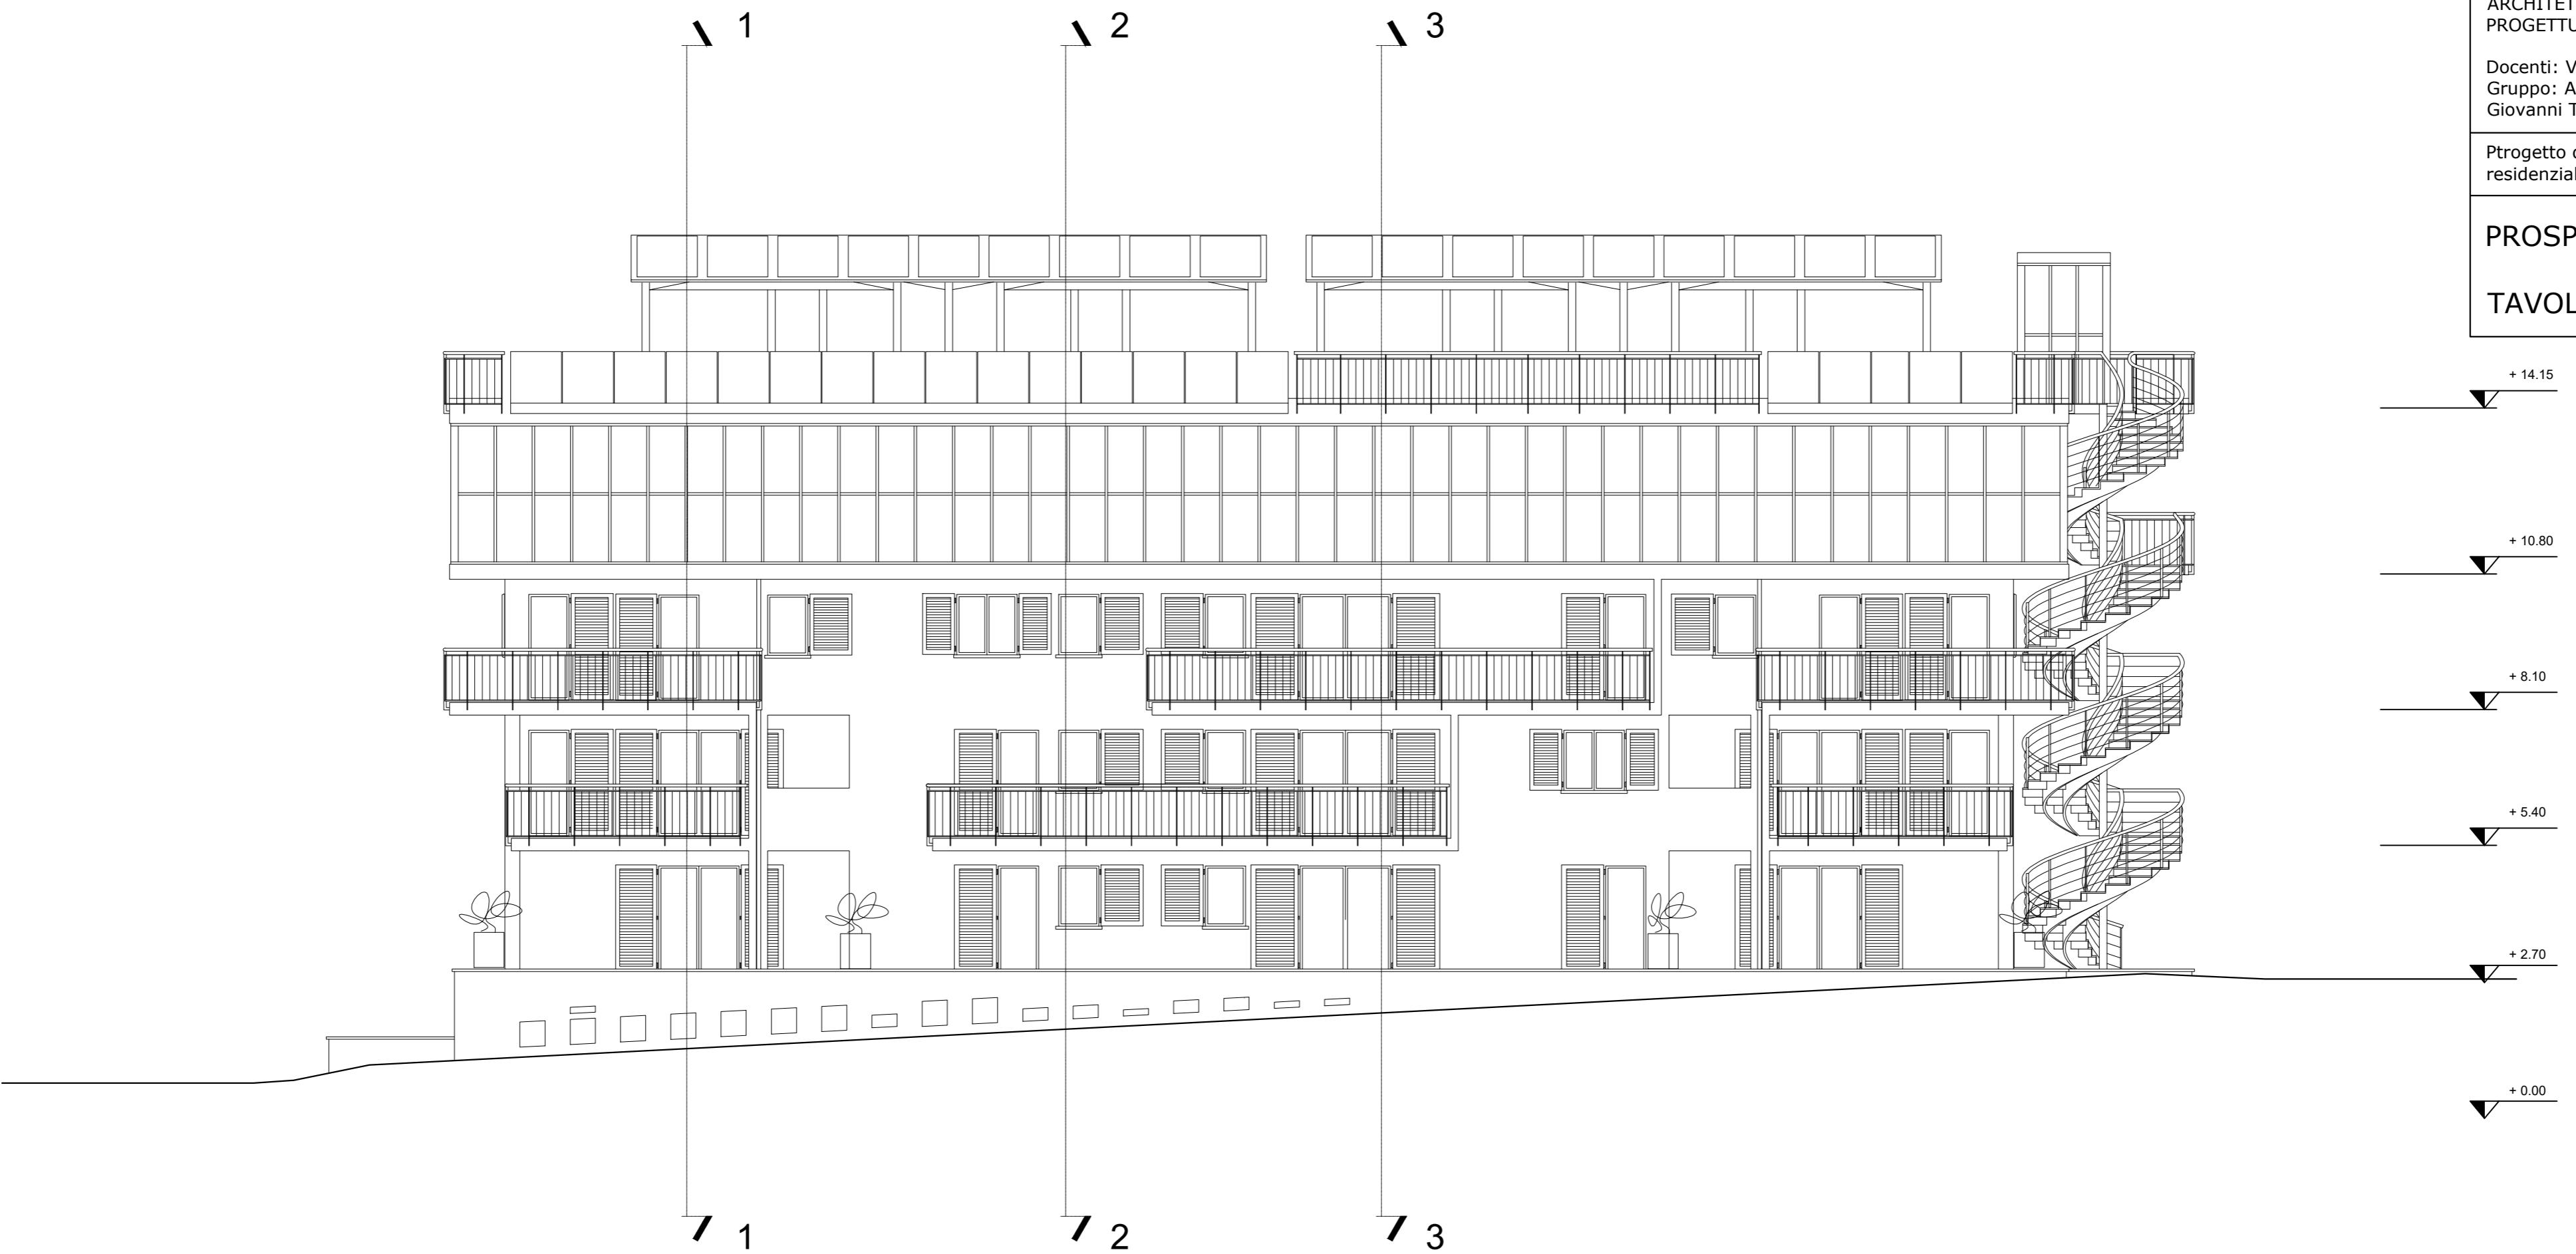



Università degli Studi di Catania

Dipartimento di Ingegneria Civile e Architettura
Corso di Laurea in Ingegneria Edile e Architettura

ARCHITETTURA TECNICA II E LABORATORIO
PROGETTUALE a.a. 2019-2020


Docenti: Vincenzo Sapienza, Gaetano Sciuto
Gruppo: Andrea Longhitano, Frenacesco Lomeo,
Giovanni Terranova

Progetto di un edificio a destinazione
residenziale e commerciale

SEZIONE 1 di 3

TAVOLA 14

Scala 1:100

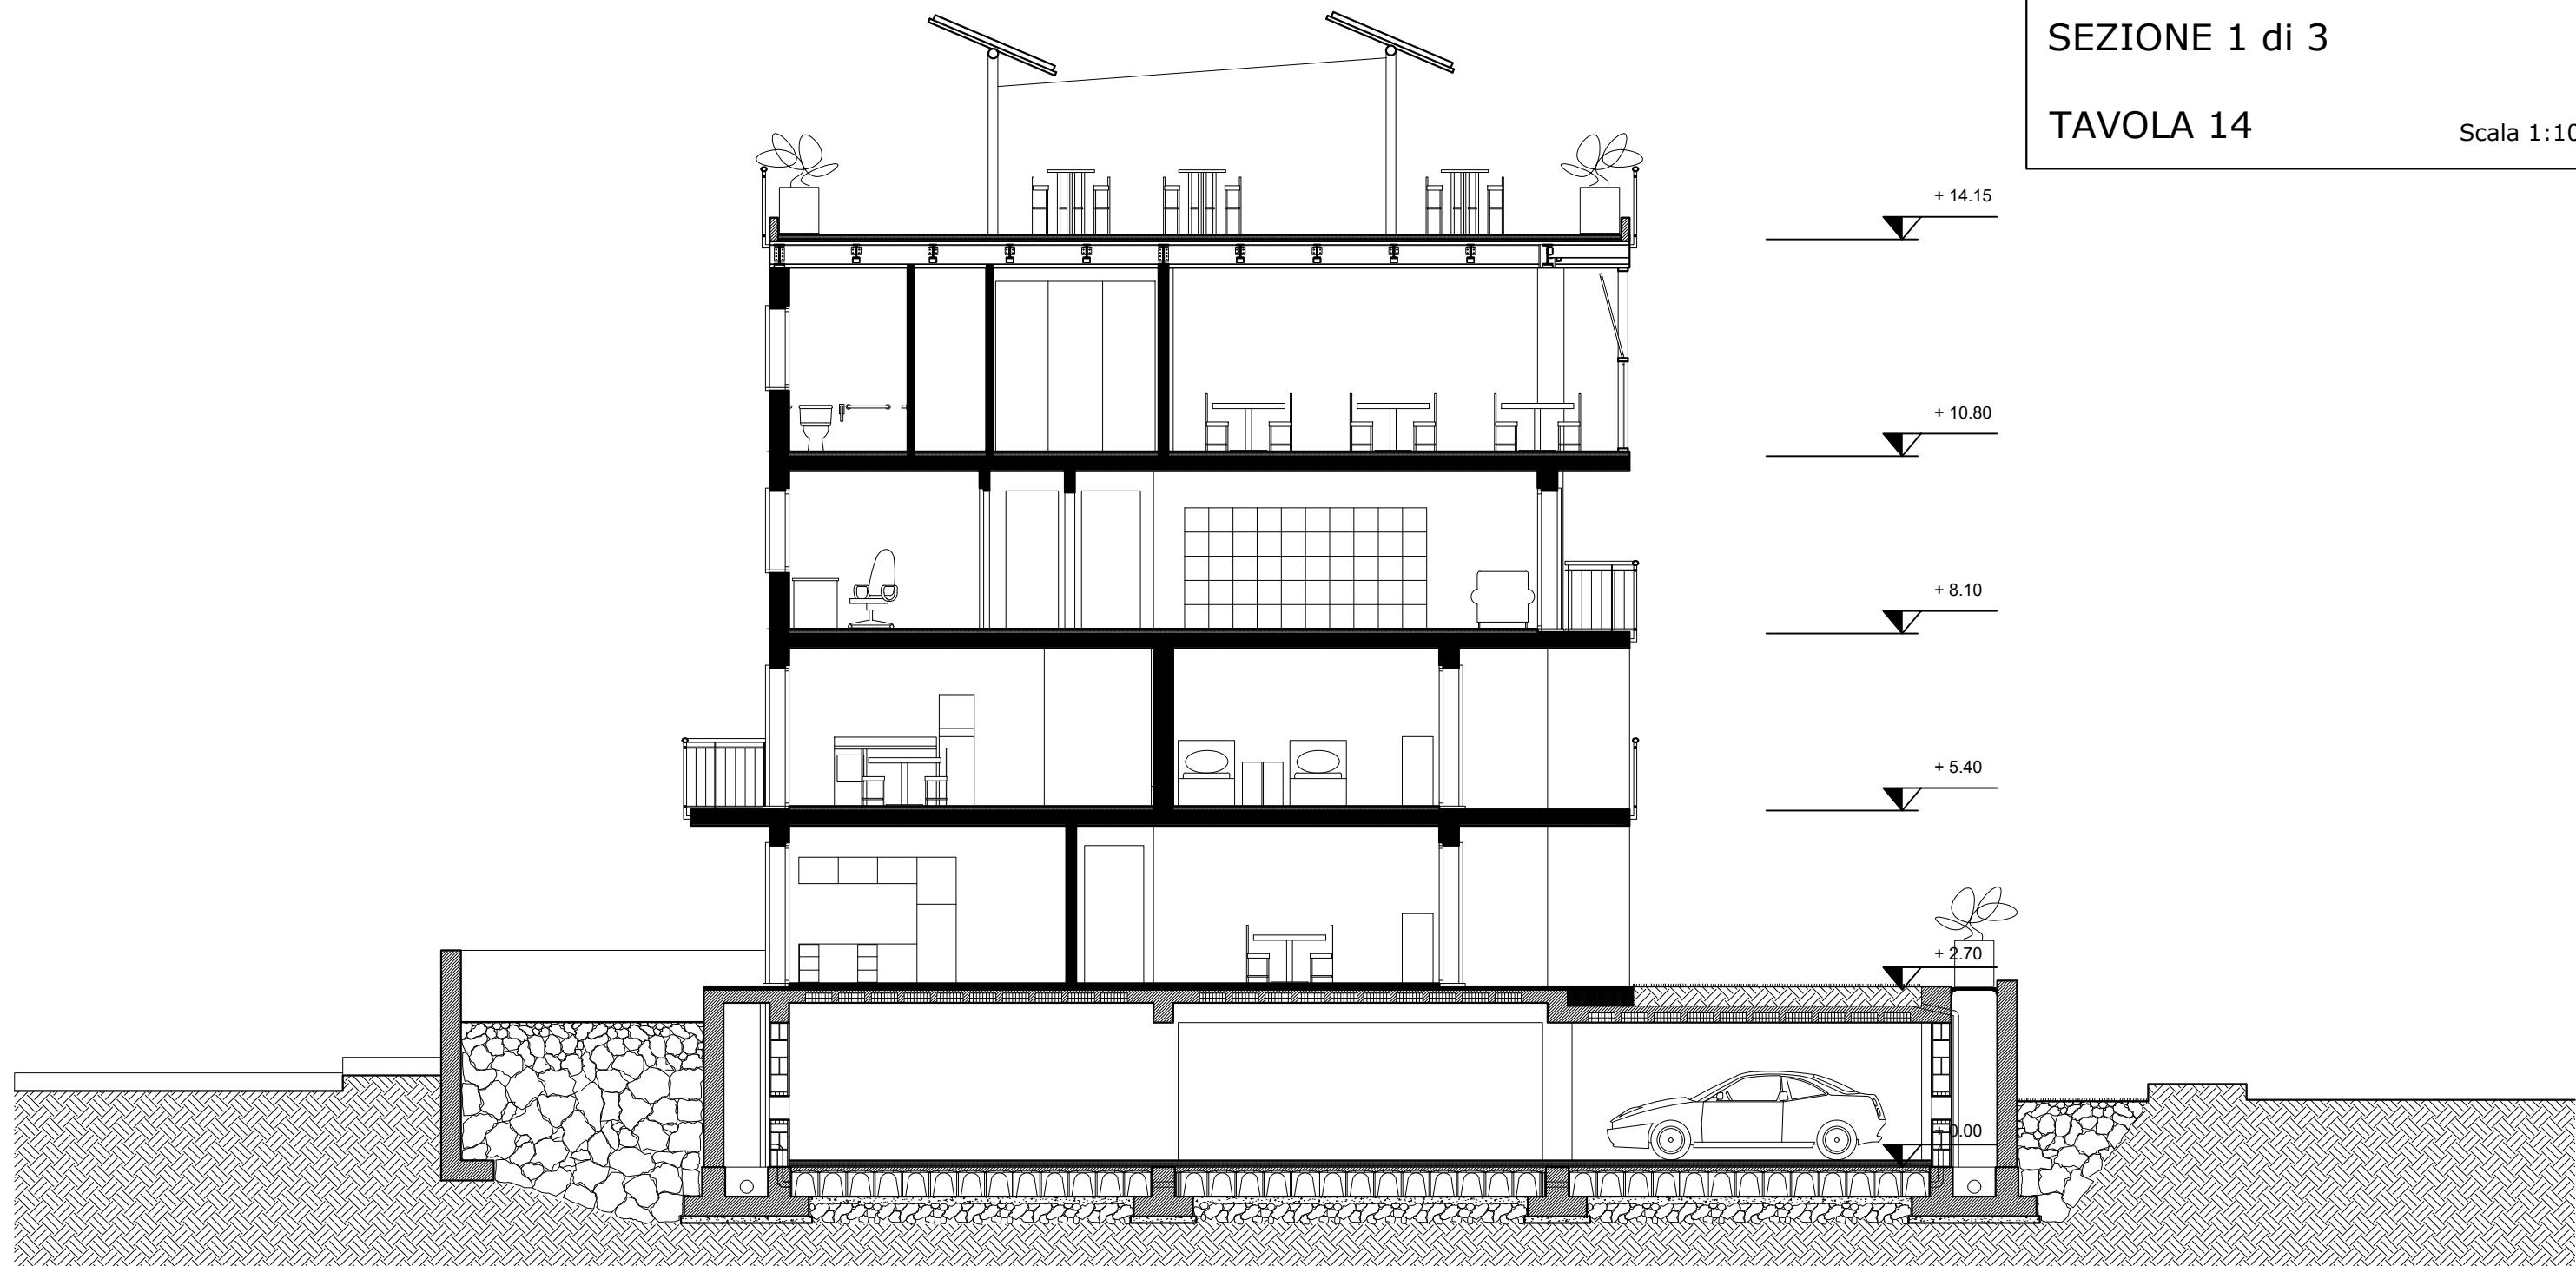



Università degli Studi di Catania

Dipartimento di Ingegneria Civile e Architettura
Corso di Laurea in Ingegneria Edile e Architettura

ARCHITETTURA TECNICA II E LABORATORIO
PROGETTUALE a.a. 2019-2020


Docenti: Vincenzo Sapienza, Gaetano Sciuto
Gruppo: Andrea Longhitano, Frenacesco Lomeo,
Giovanni Terranova

Progetto di un edificio a destinazione
residenziale e commerciale

SEZIONE 2 di 3

TAVOLA 15

Scala 1:100

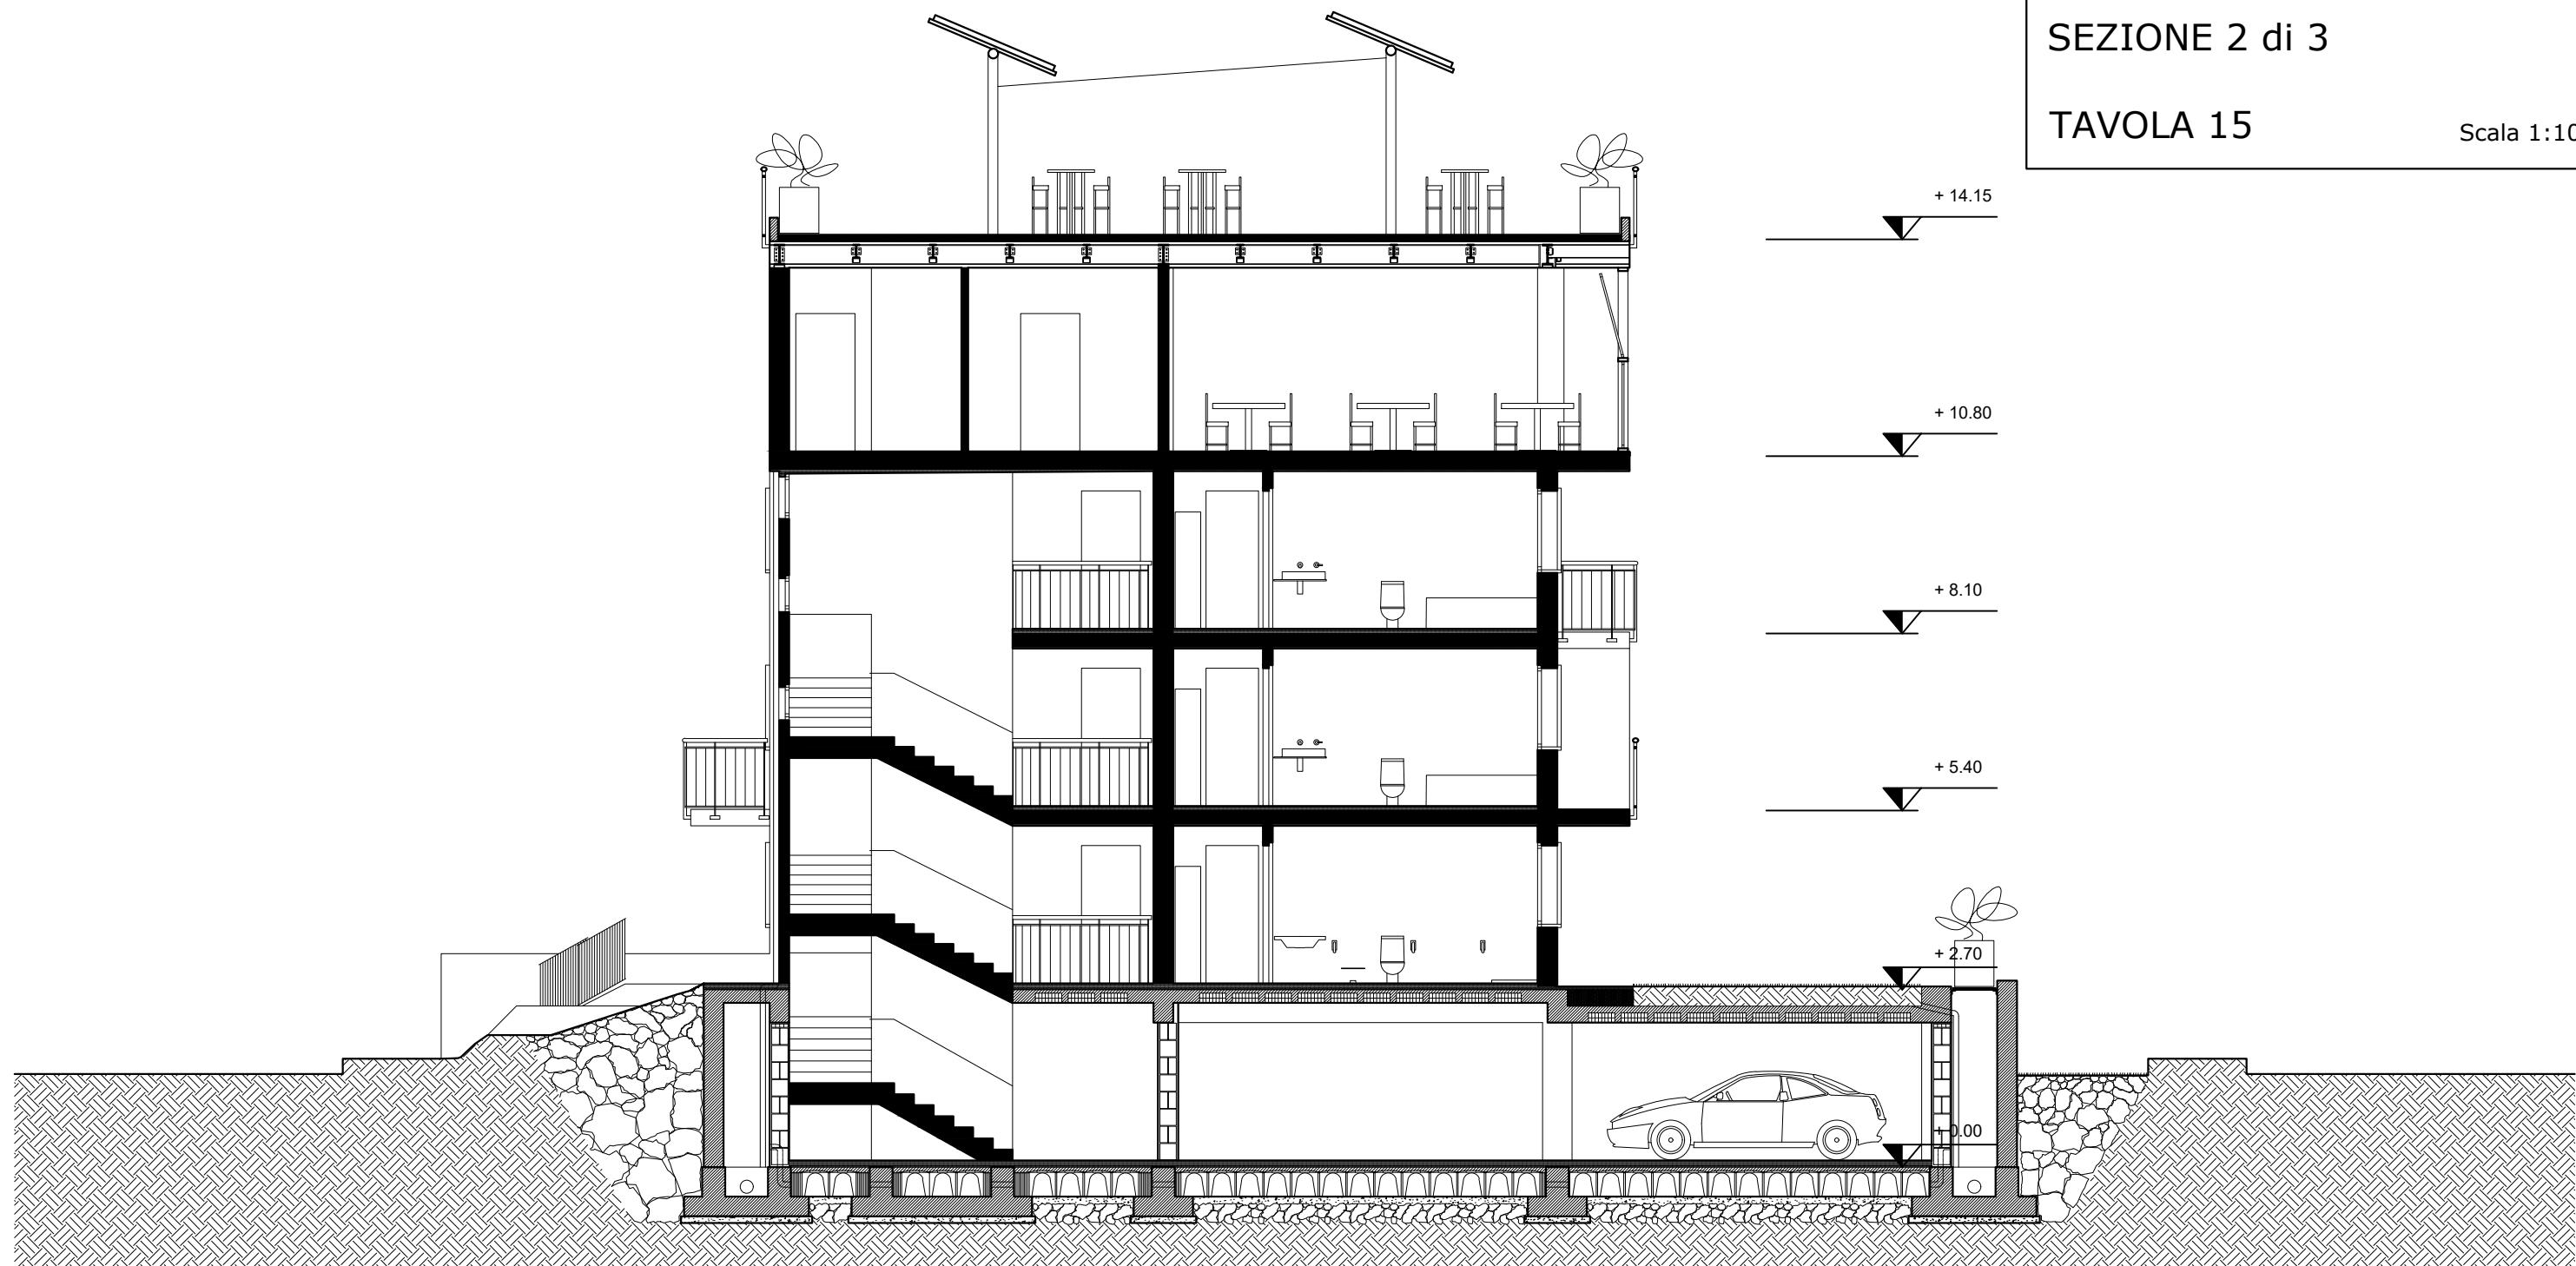



Università degli Studi di Catania

Dipartimento di Ingegneria Civile e Architettura
Corso di Laurea in Ingegneria Edile e Architettura

ARCHITETTURA TECNICA II E LABORATORIO
PROGETTUALE a.a. 2019-2020


Docenti: Vincenzo Sapienza, Gaetano Sciuto
Gruppo: Andrea Longhitano, Frenacesco Lomeo,
Giovanni Terranova


Progetto di un edificio a destinazione
residenziale e commerciale

SEZIONE 3 di 3

TAVOLA 16

Scala 1:100

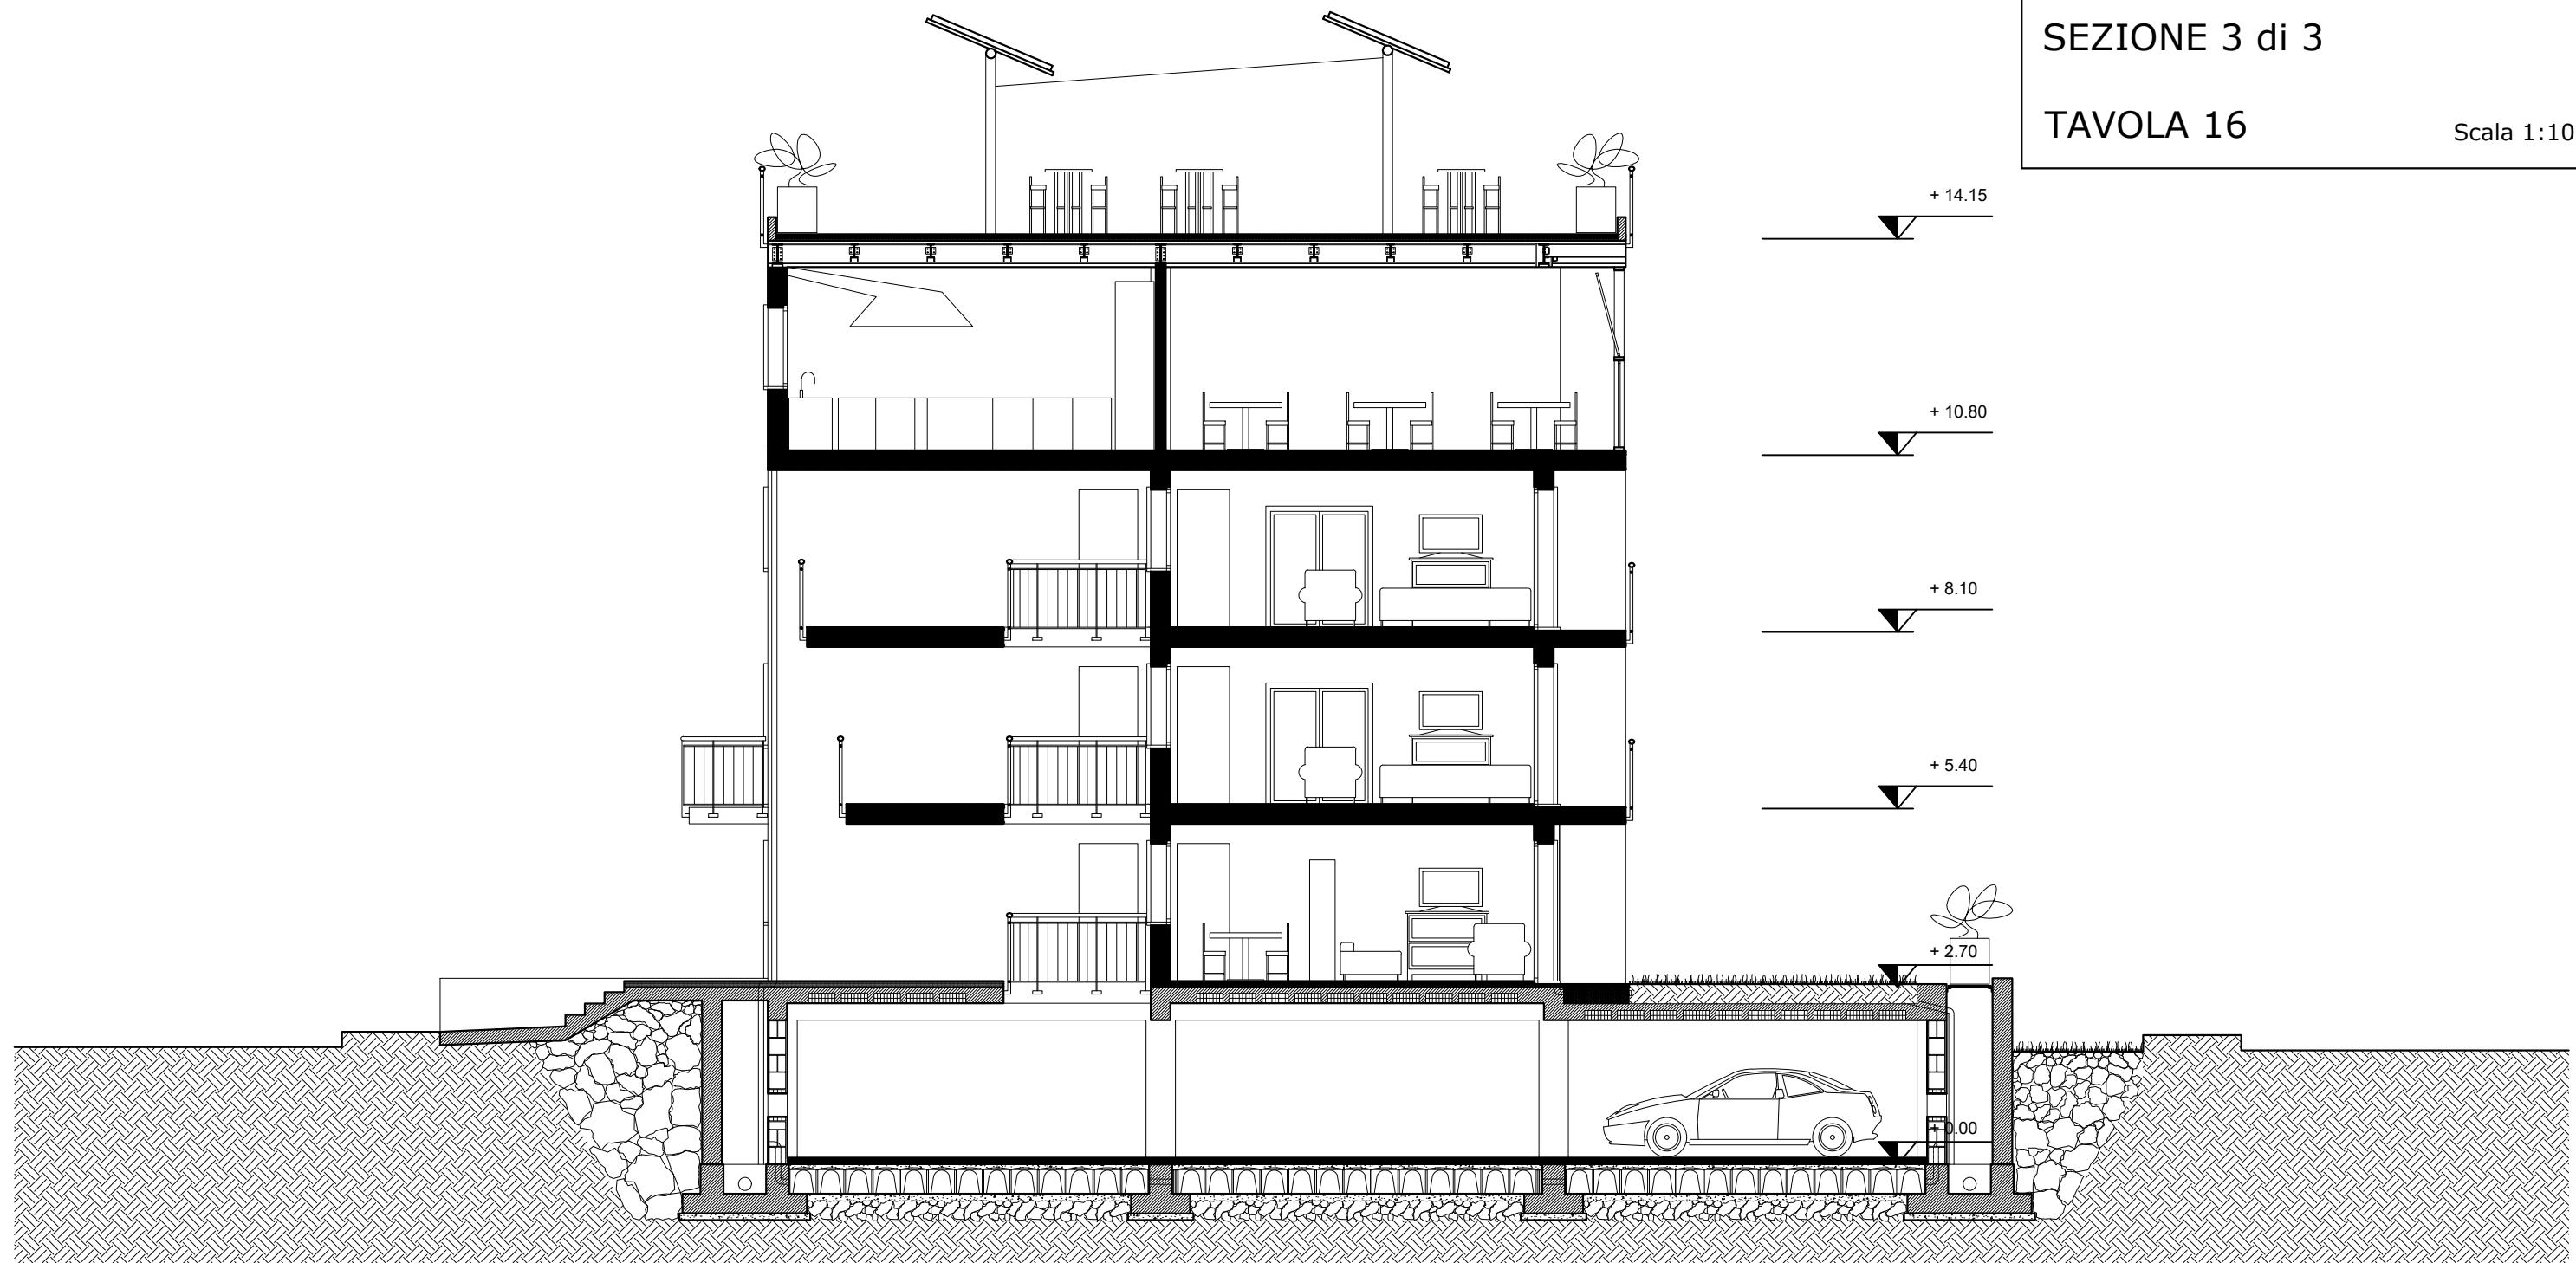

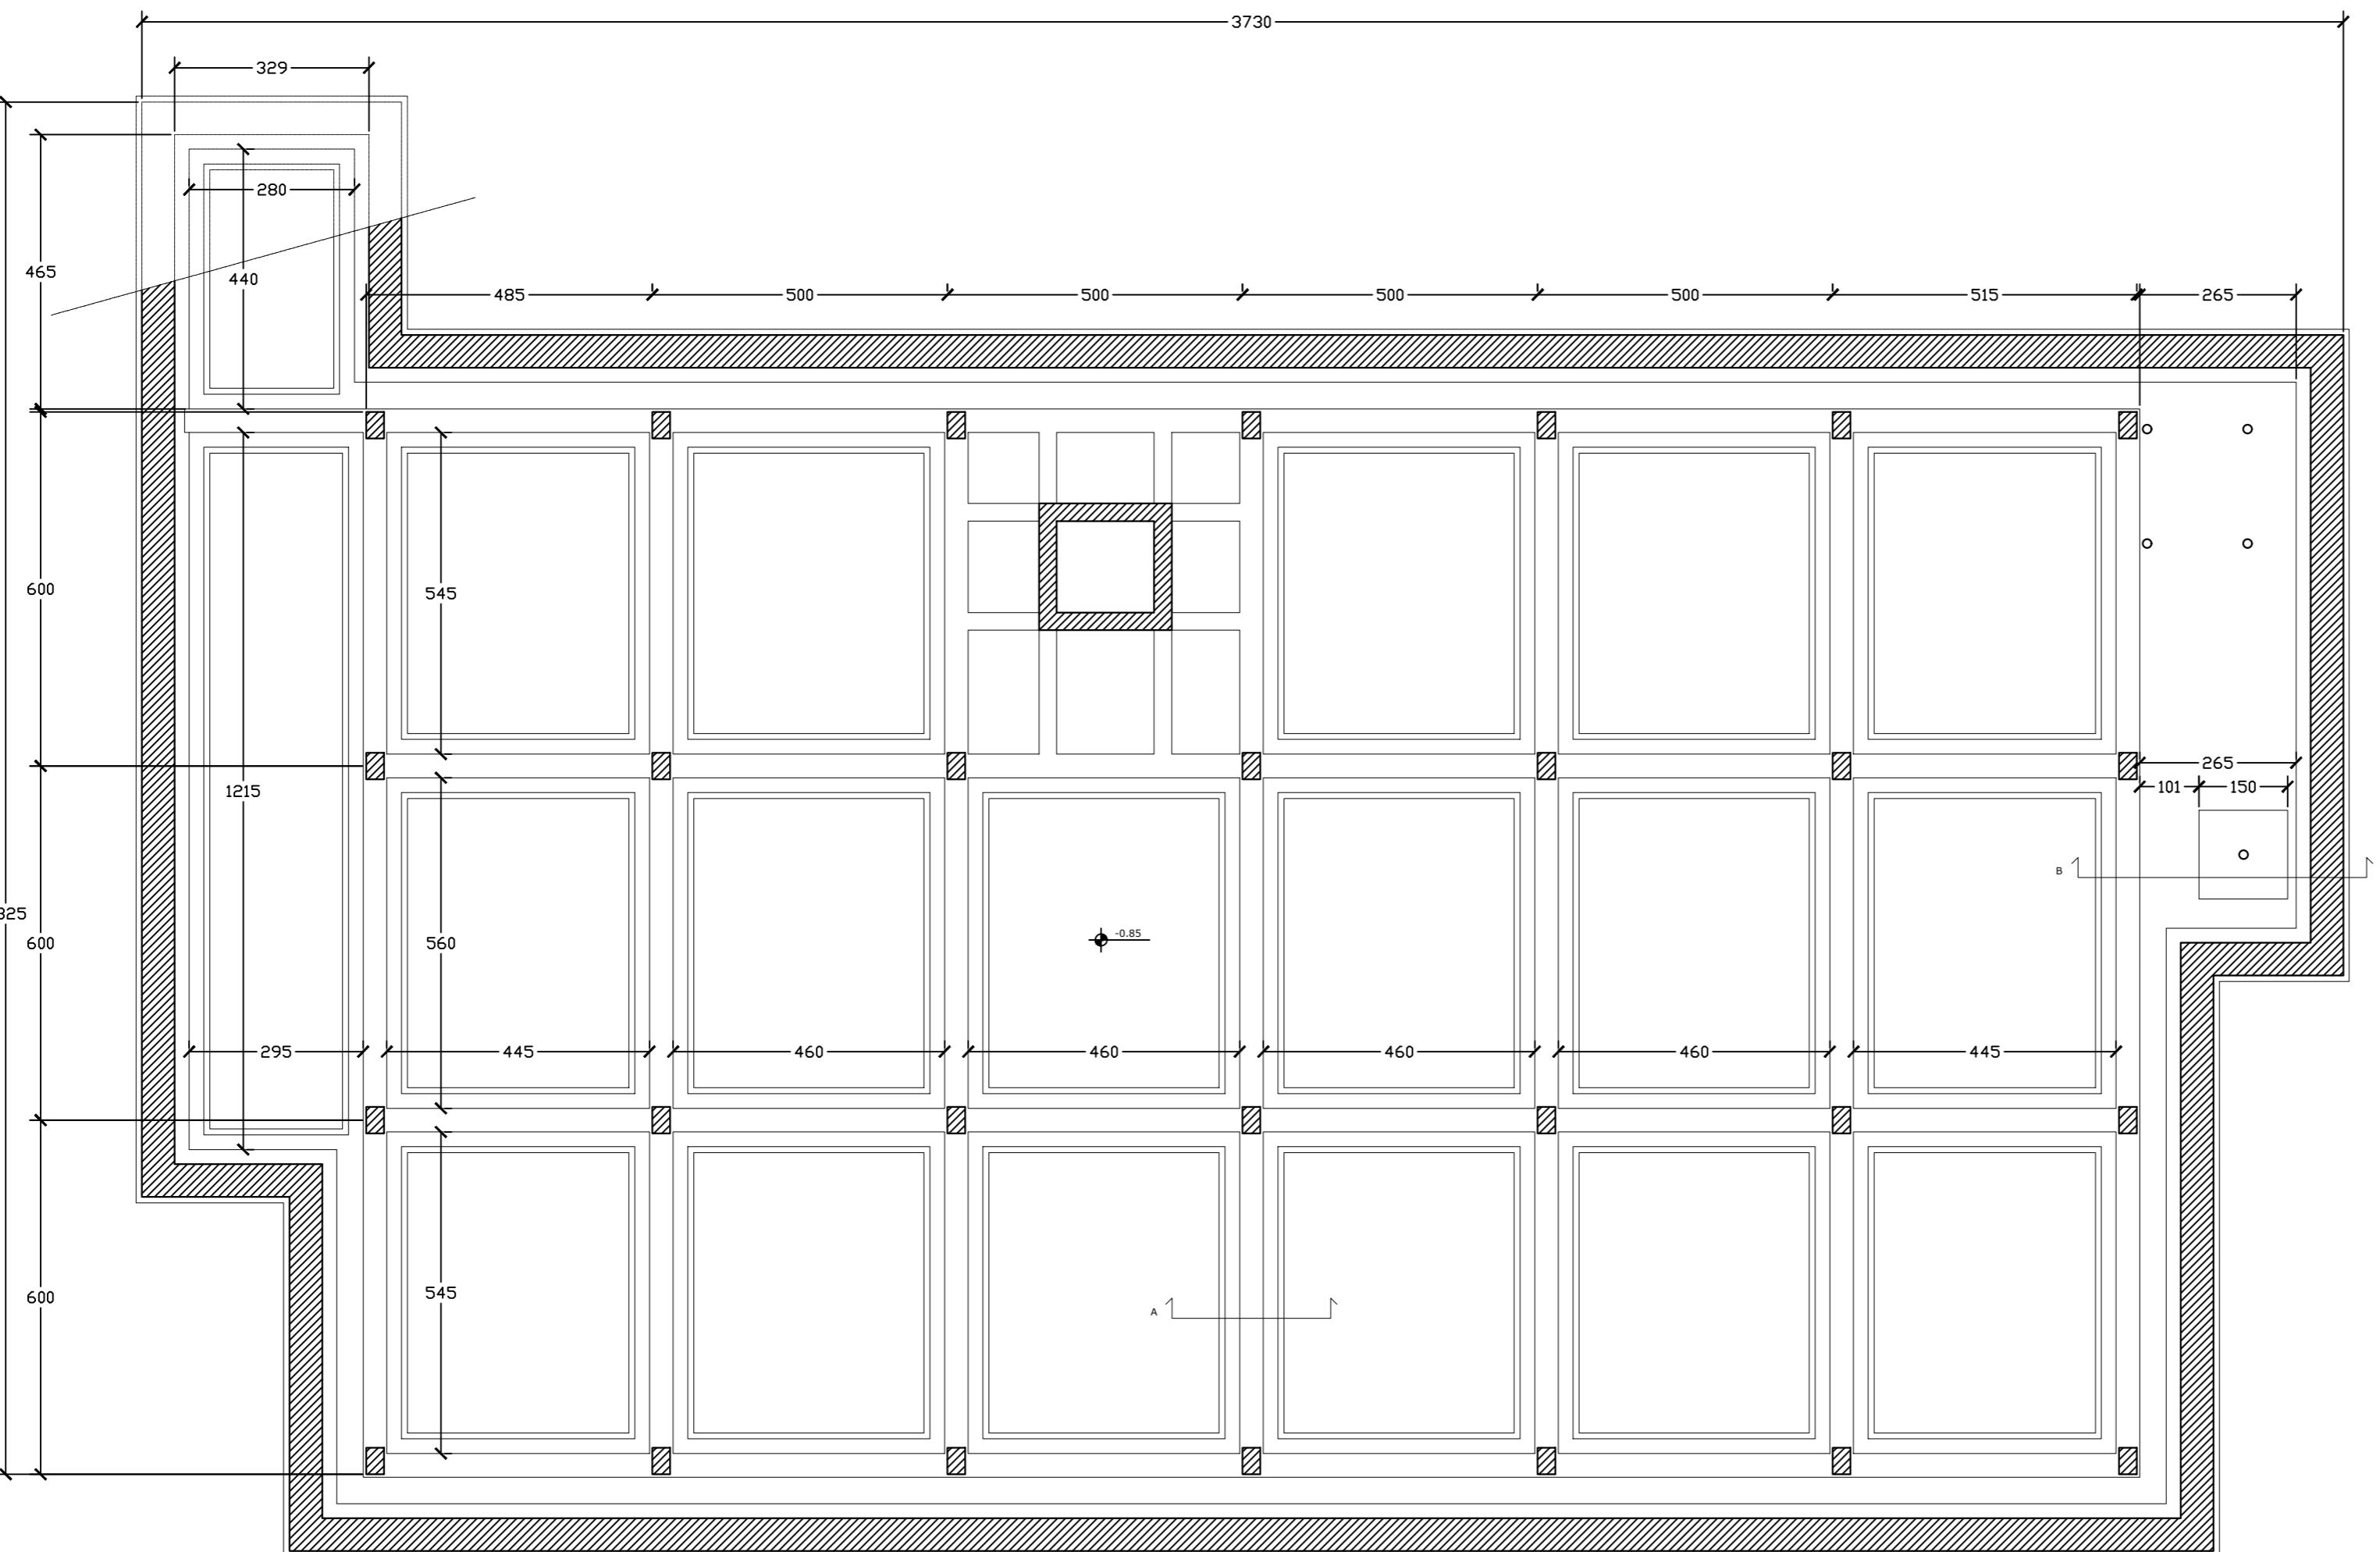



Università degli Studi di Catania

Dipartimento di Ingegneria Civile e Architettura
Corso di Laurea in Ingegneria Edile e Architettura



ARCHITETTURA TECNICA II E LABORATORIO
PROGETTUALE a.a. 2019-2020


Docenti: Vincenzo Sapienza, Gaetano Sciuto
Gruppo: Andrea Longhitano, Frenacesco Lomeo,
Giovanni Terranova


Progetto di un edificio a destinazione
residenziale e commerciale

DETTAGLIO CARPENTERIA
1 di 2
TAVOLA 17a

Scala 1:20

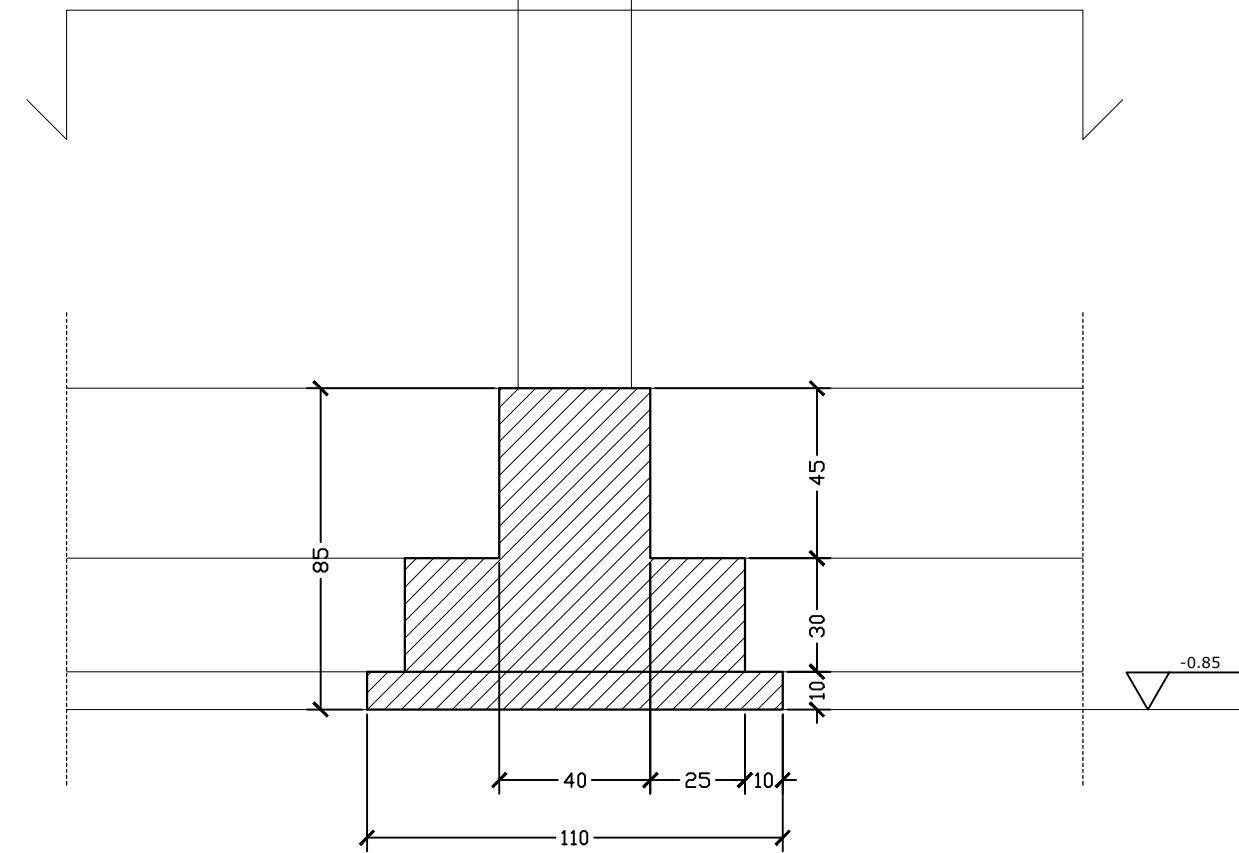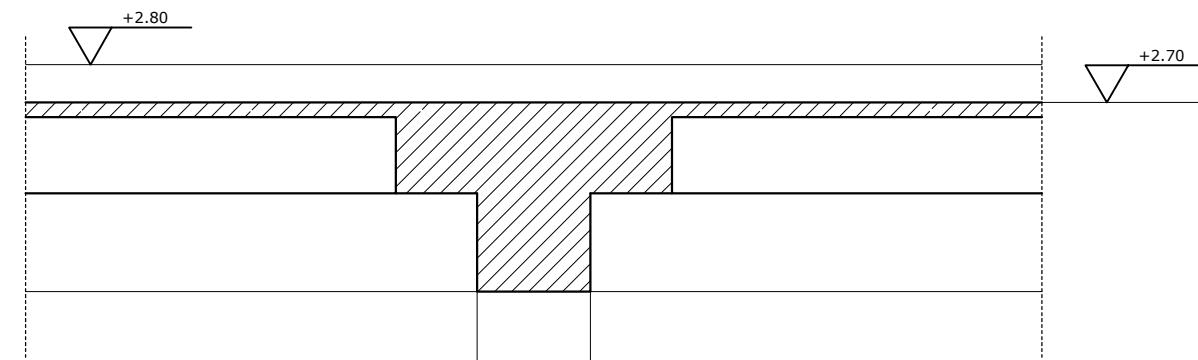

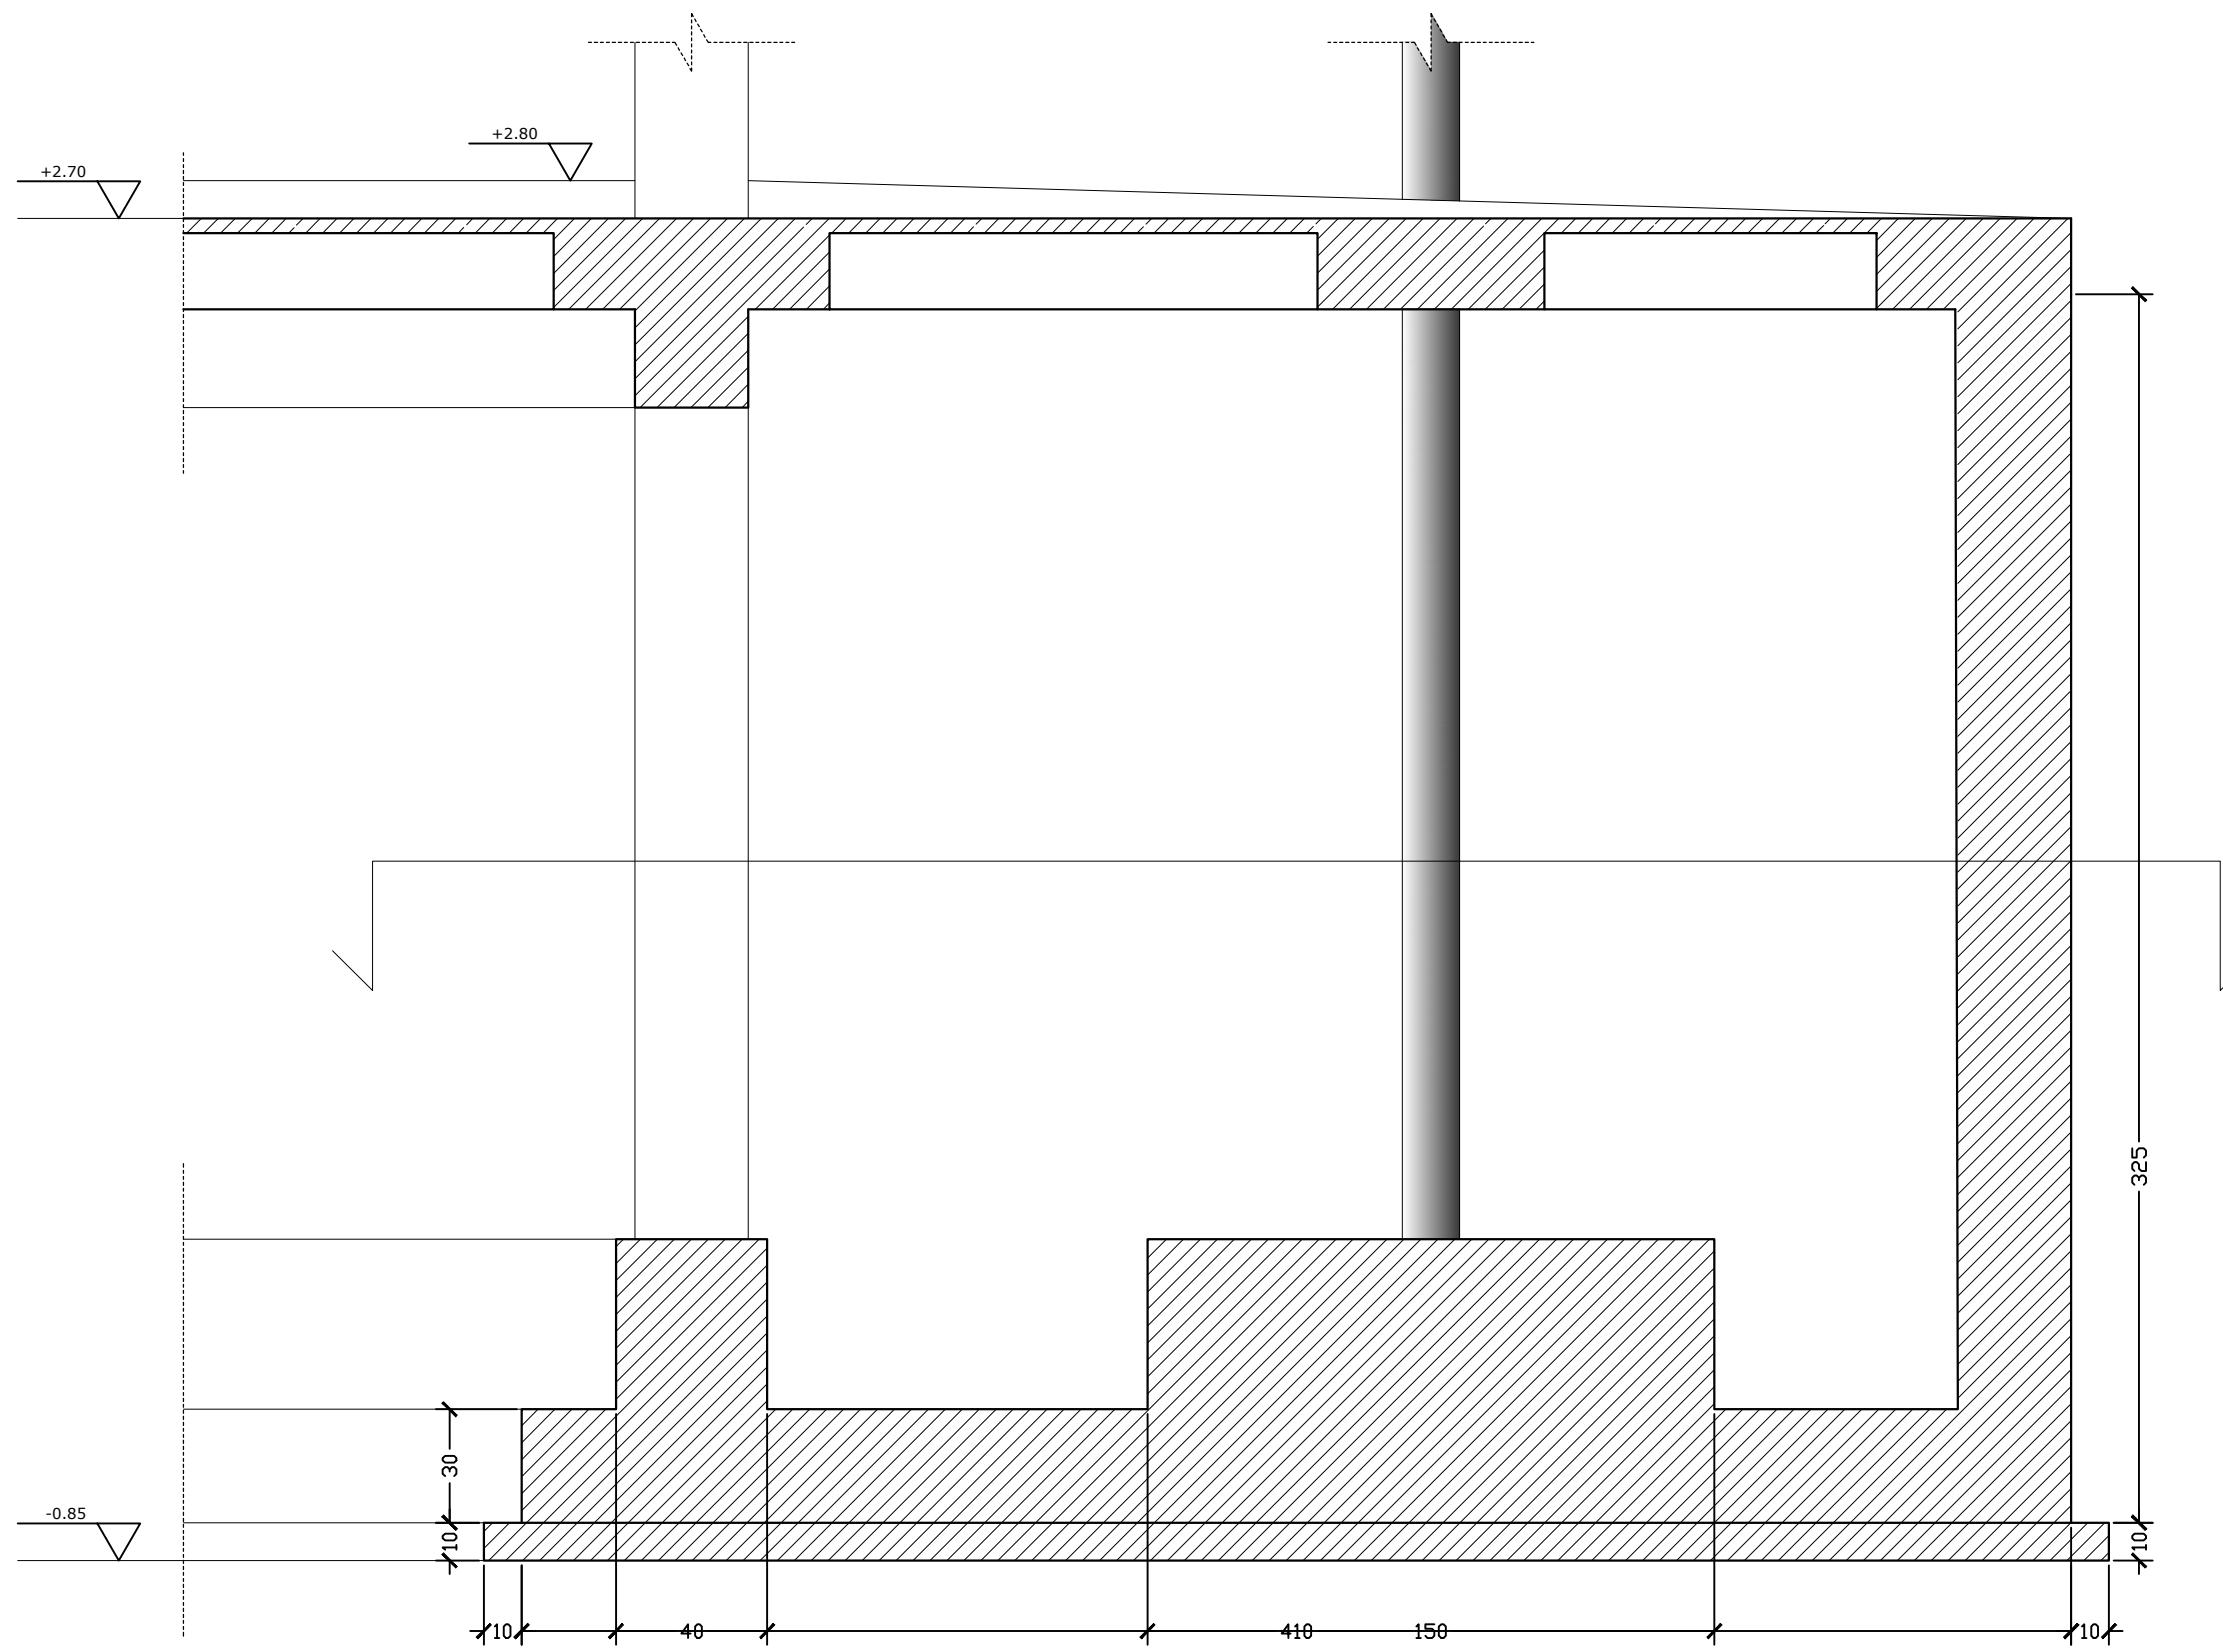

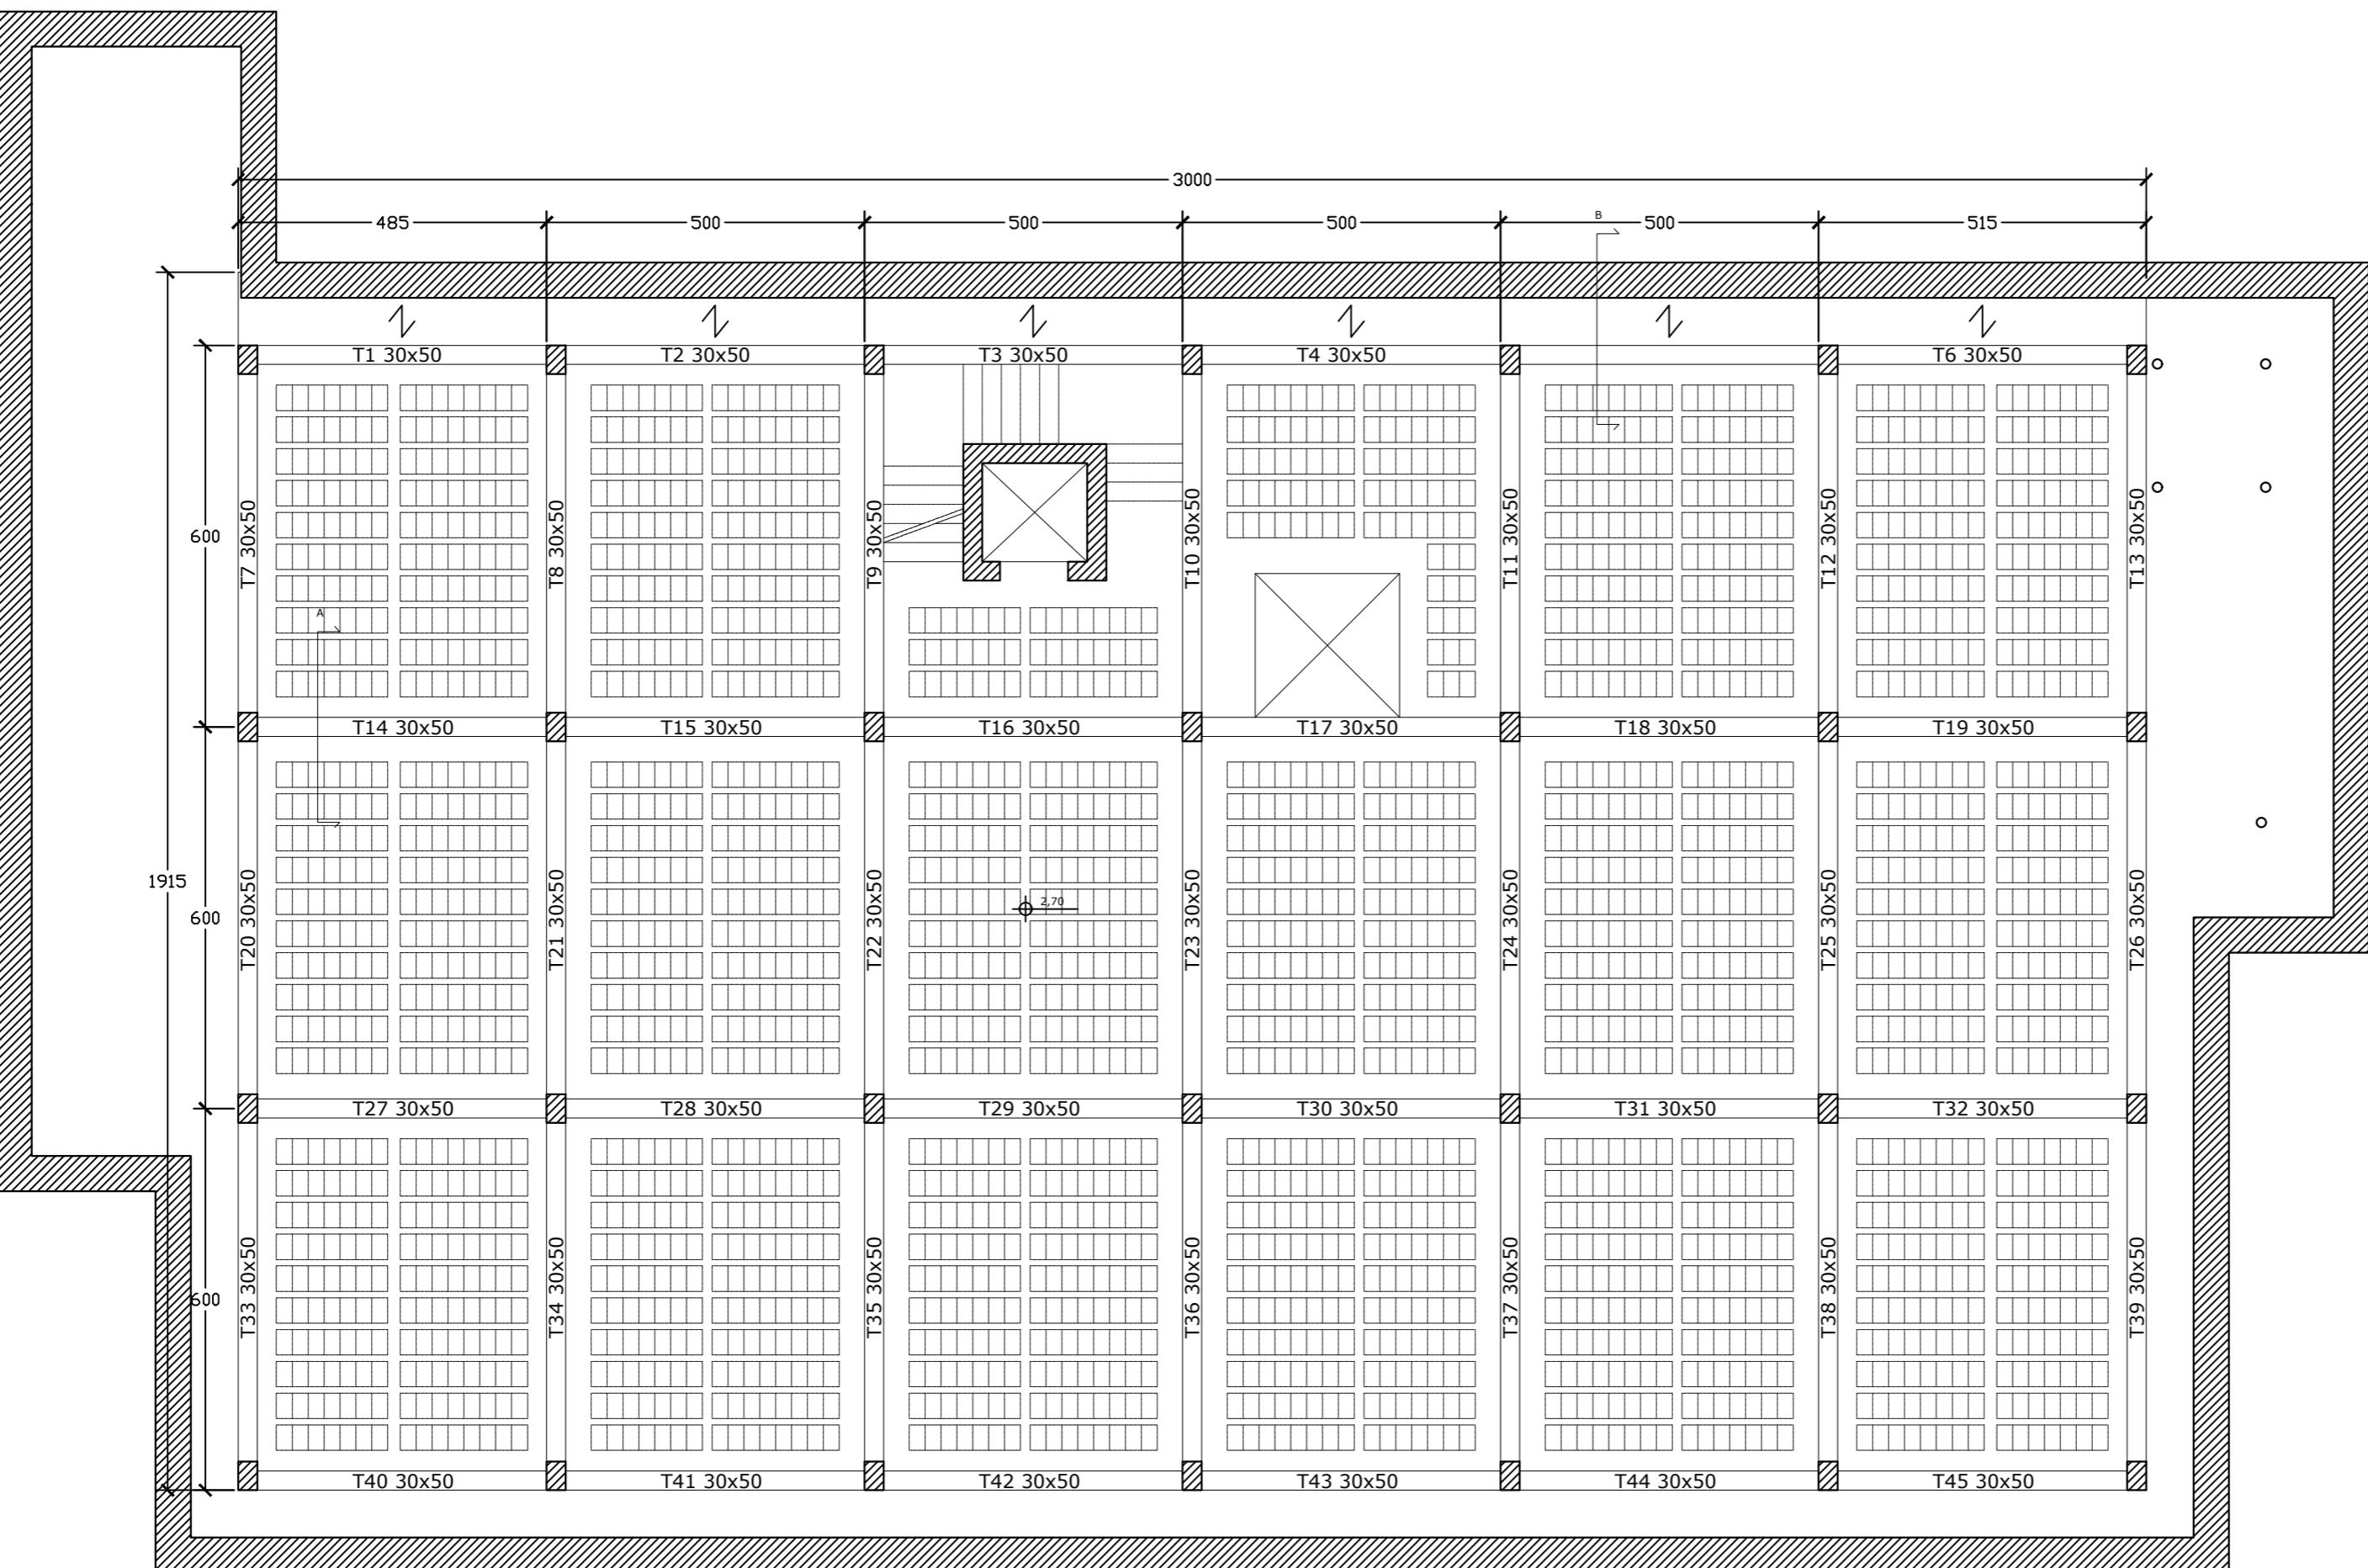



Università degli Studi di Catania

Dipartimento di Ingegneria Civile e Architettura
Corso di Laurea in Ingegneria Edile e Architettura



ARCHITETTURA TECNICA II E LABORATORIO
PROGETTUALE a.a. 2019-2020

Docenti: Vincenzo Sapienza, Gaetano Sciuto
Gruppo: Andrea Longhitano, Frenacesco Lomeo,
Giovanni Terranova

Progetto di un edificio a destinazione
residenziale e commerciale

DETTAGLIO CARPENTERIA
1 di 2
TAVOLA 18a

Scala 1:20

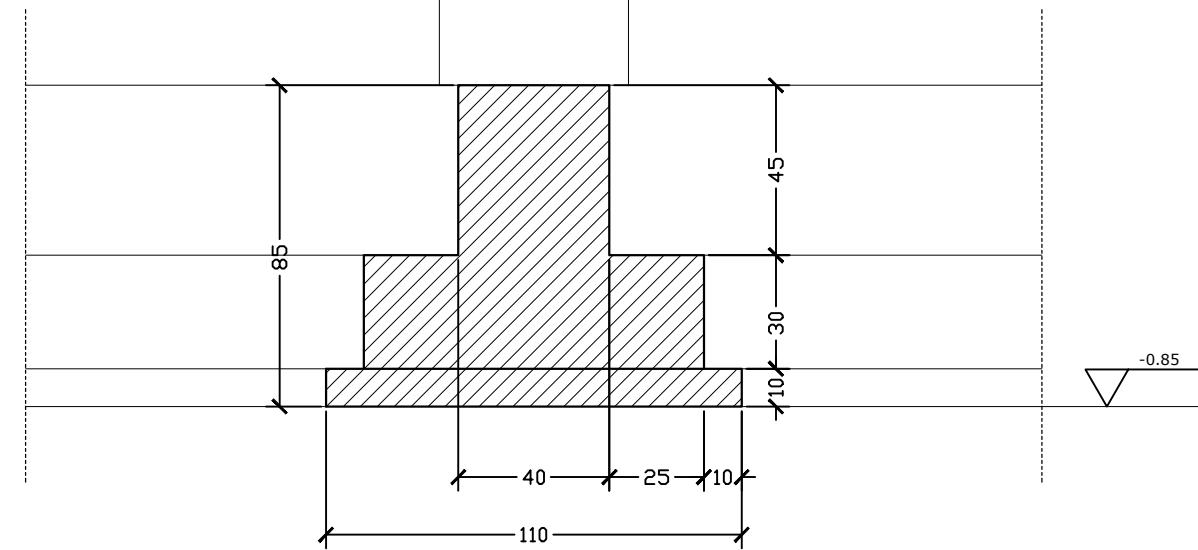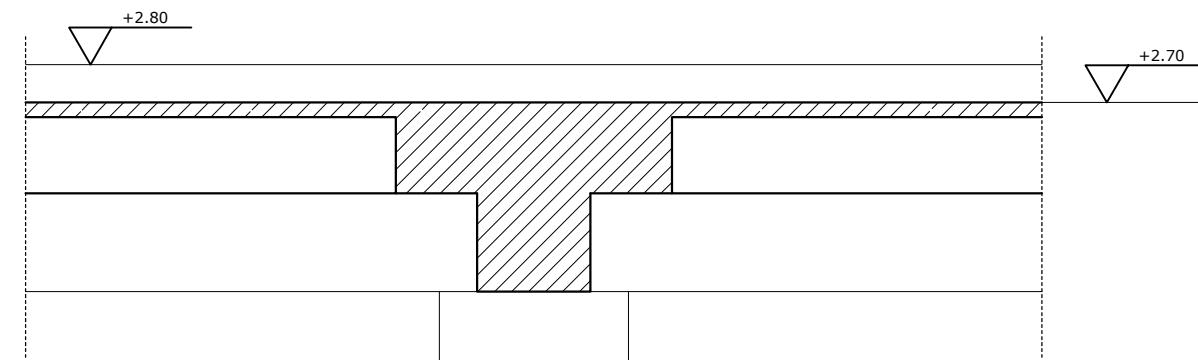



Università degli Studi di Catania

Dipartimento di Ingegneria Civile e Architettura
Corso di Laurea in Ingegneria Edile e Architettura


ARCHITETTURA TECNICA II E LABORATORIO
PROGETTUALE a.a. 2019-2020



Docenti: Vincenzo Sapienza, Gaetano Sciuto
Gruppo: Andrea Longhitano, Frenacesco Lomeo,
Giovanni Terranova

Progetto di un edificio a destinazione
residenziale e commerciale

DETTAGLIO CARPENTERIA
2 di 2
TAVOLA 18b


Scala 1:20

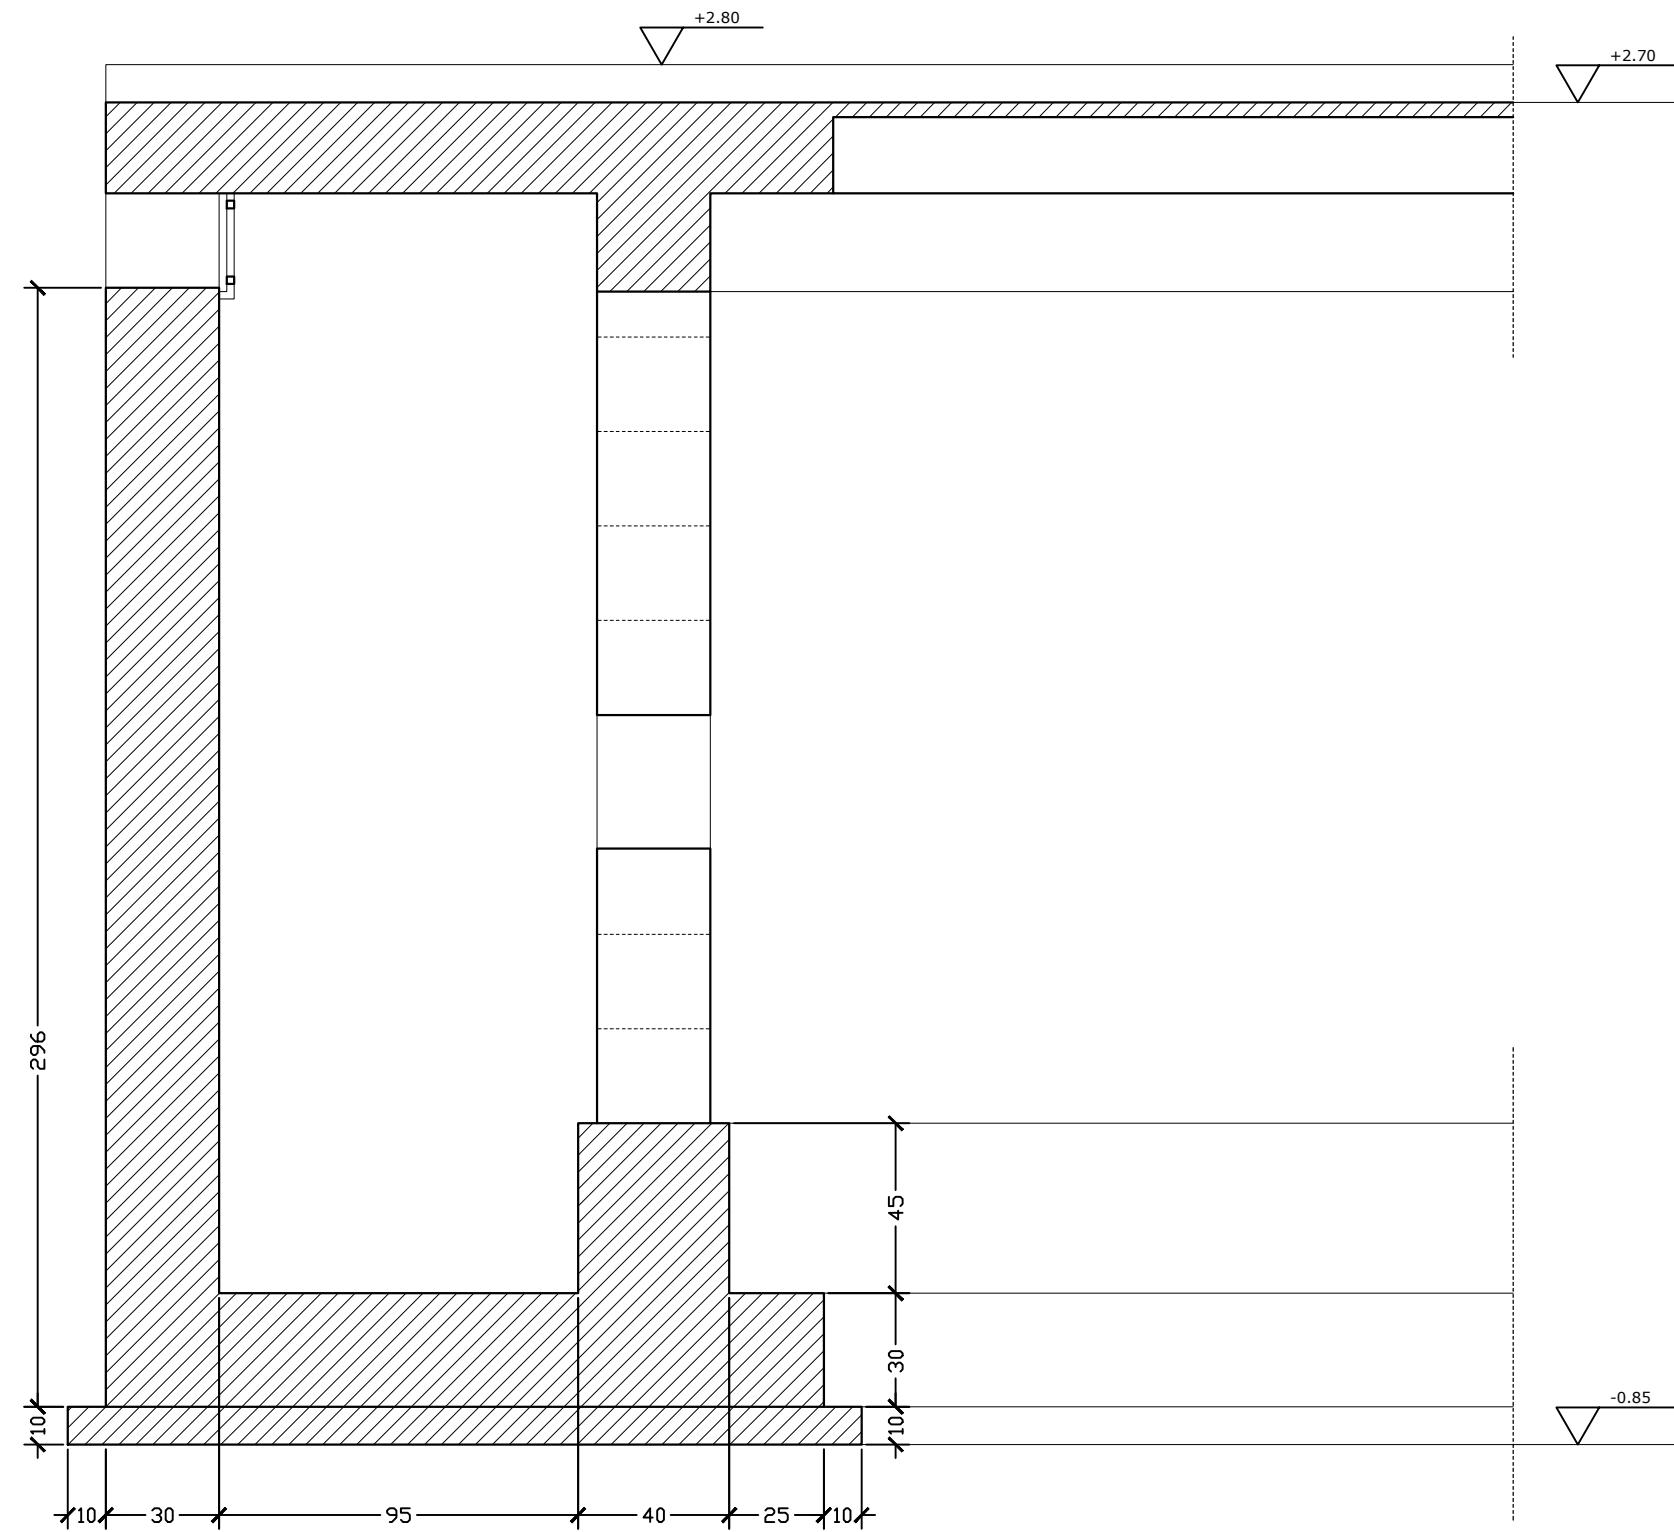

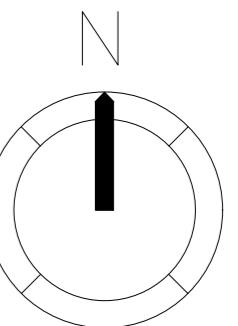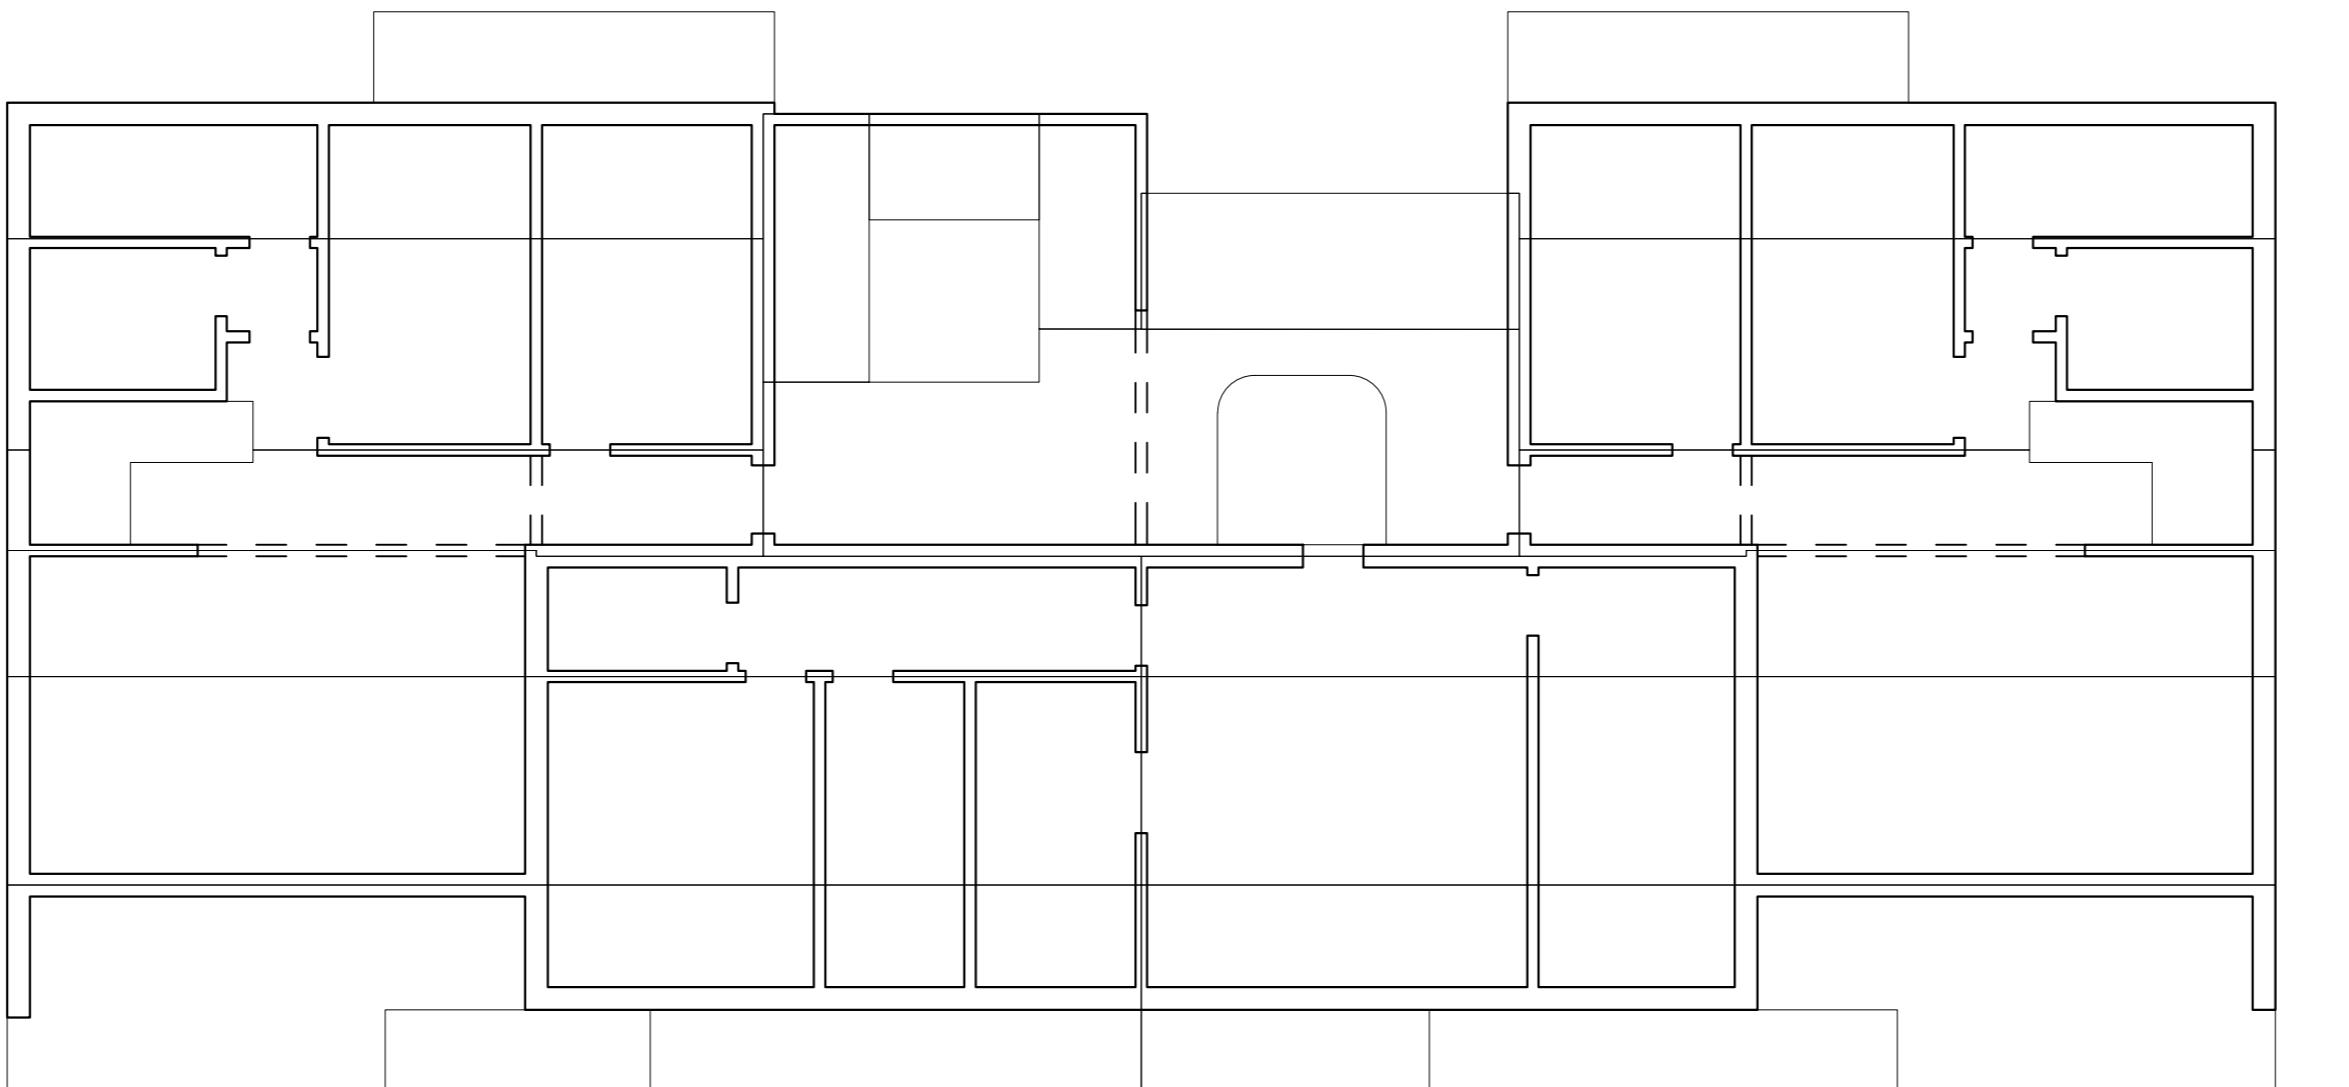


ABACO PANNELLI XLAM
TAVOLA 19a


Scala 1:200

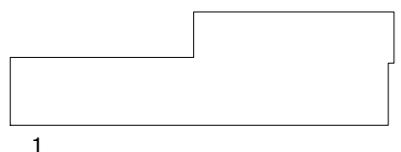

1

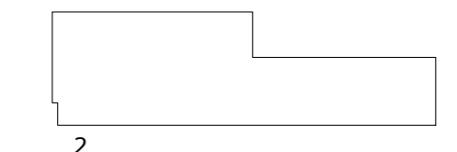


2

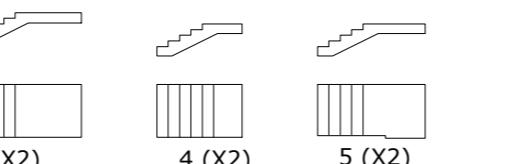


3 (X2)

4 (X2)


5 (X2)

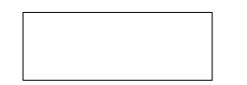


6

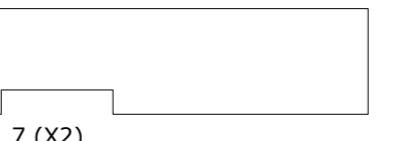


7 (X2)

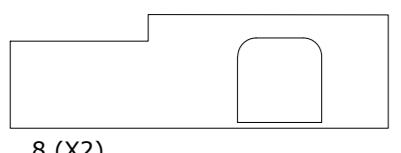


8 (X2)

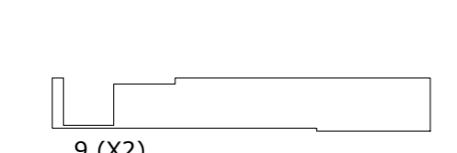


9 (X2)

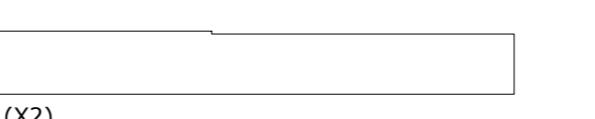


10 (X2)

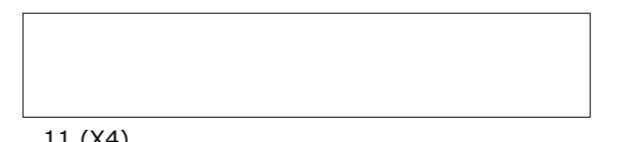


11 (X4)

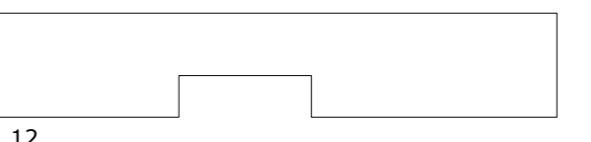

12

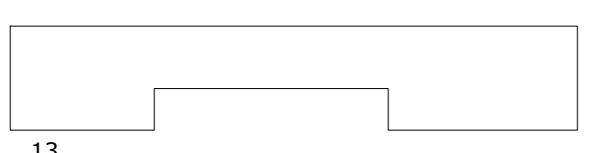


13

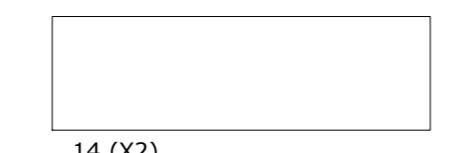


14 (X2)




15

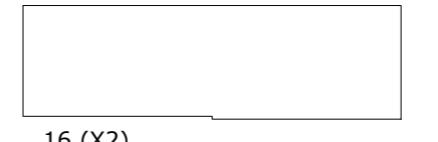


16 (X2)

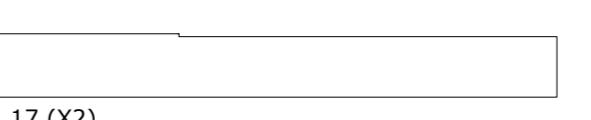


17 (X2)

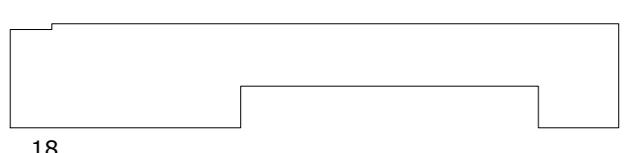


18

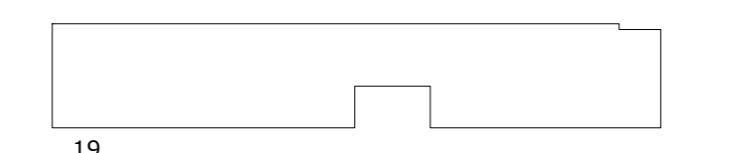


19

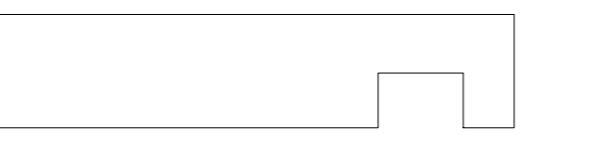


20

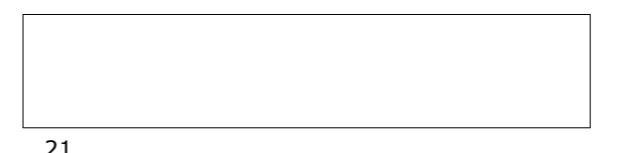

21

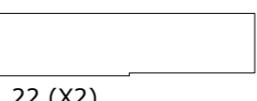


22 (X2)

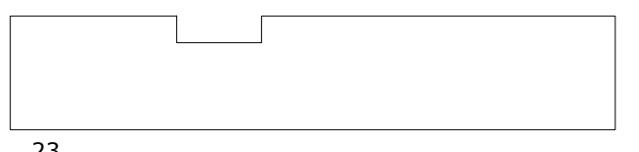


23




24 (X2)

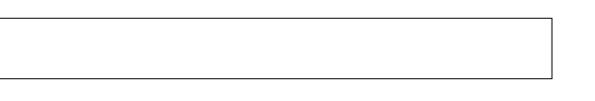




25


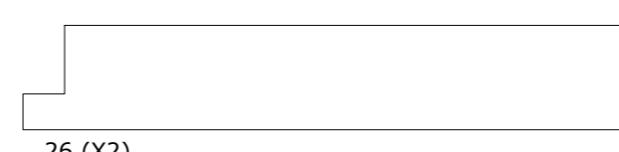




26 (X2)

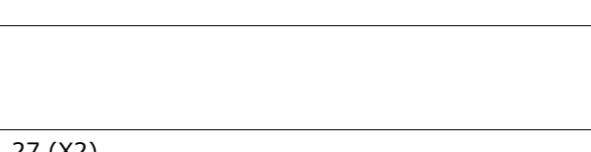

27 (X2)

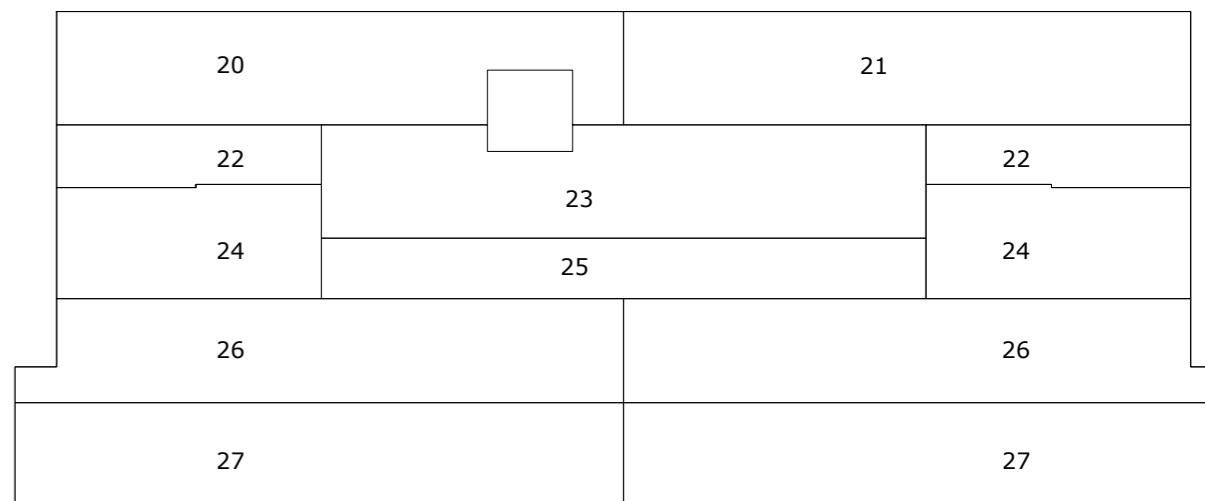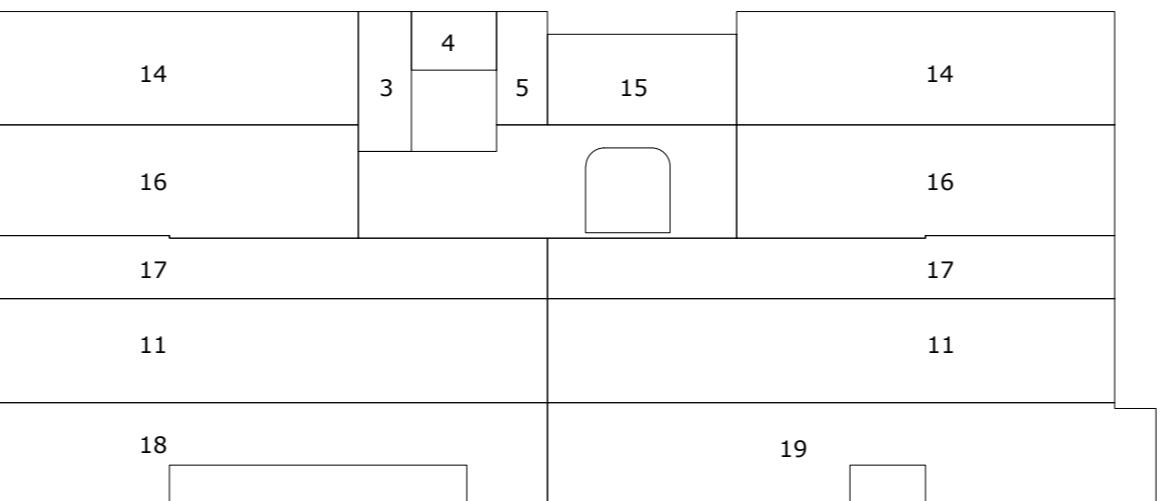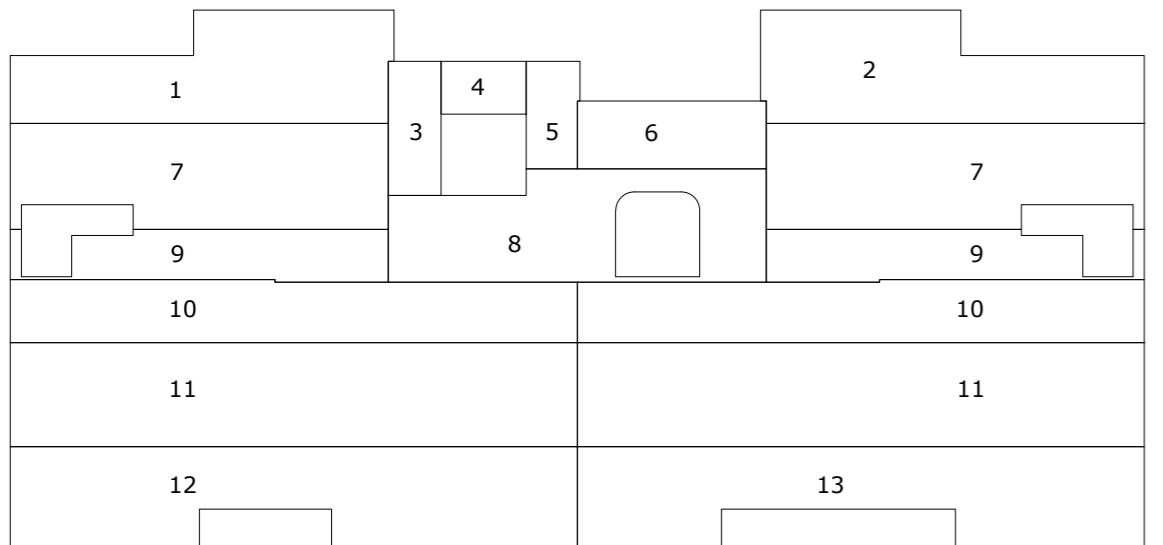


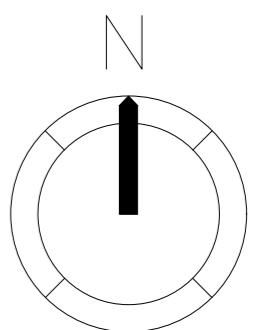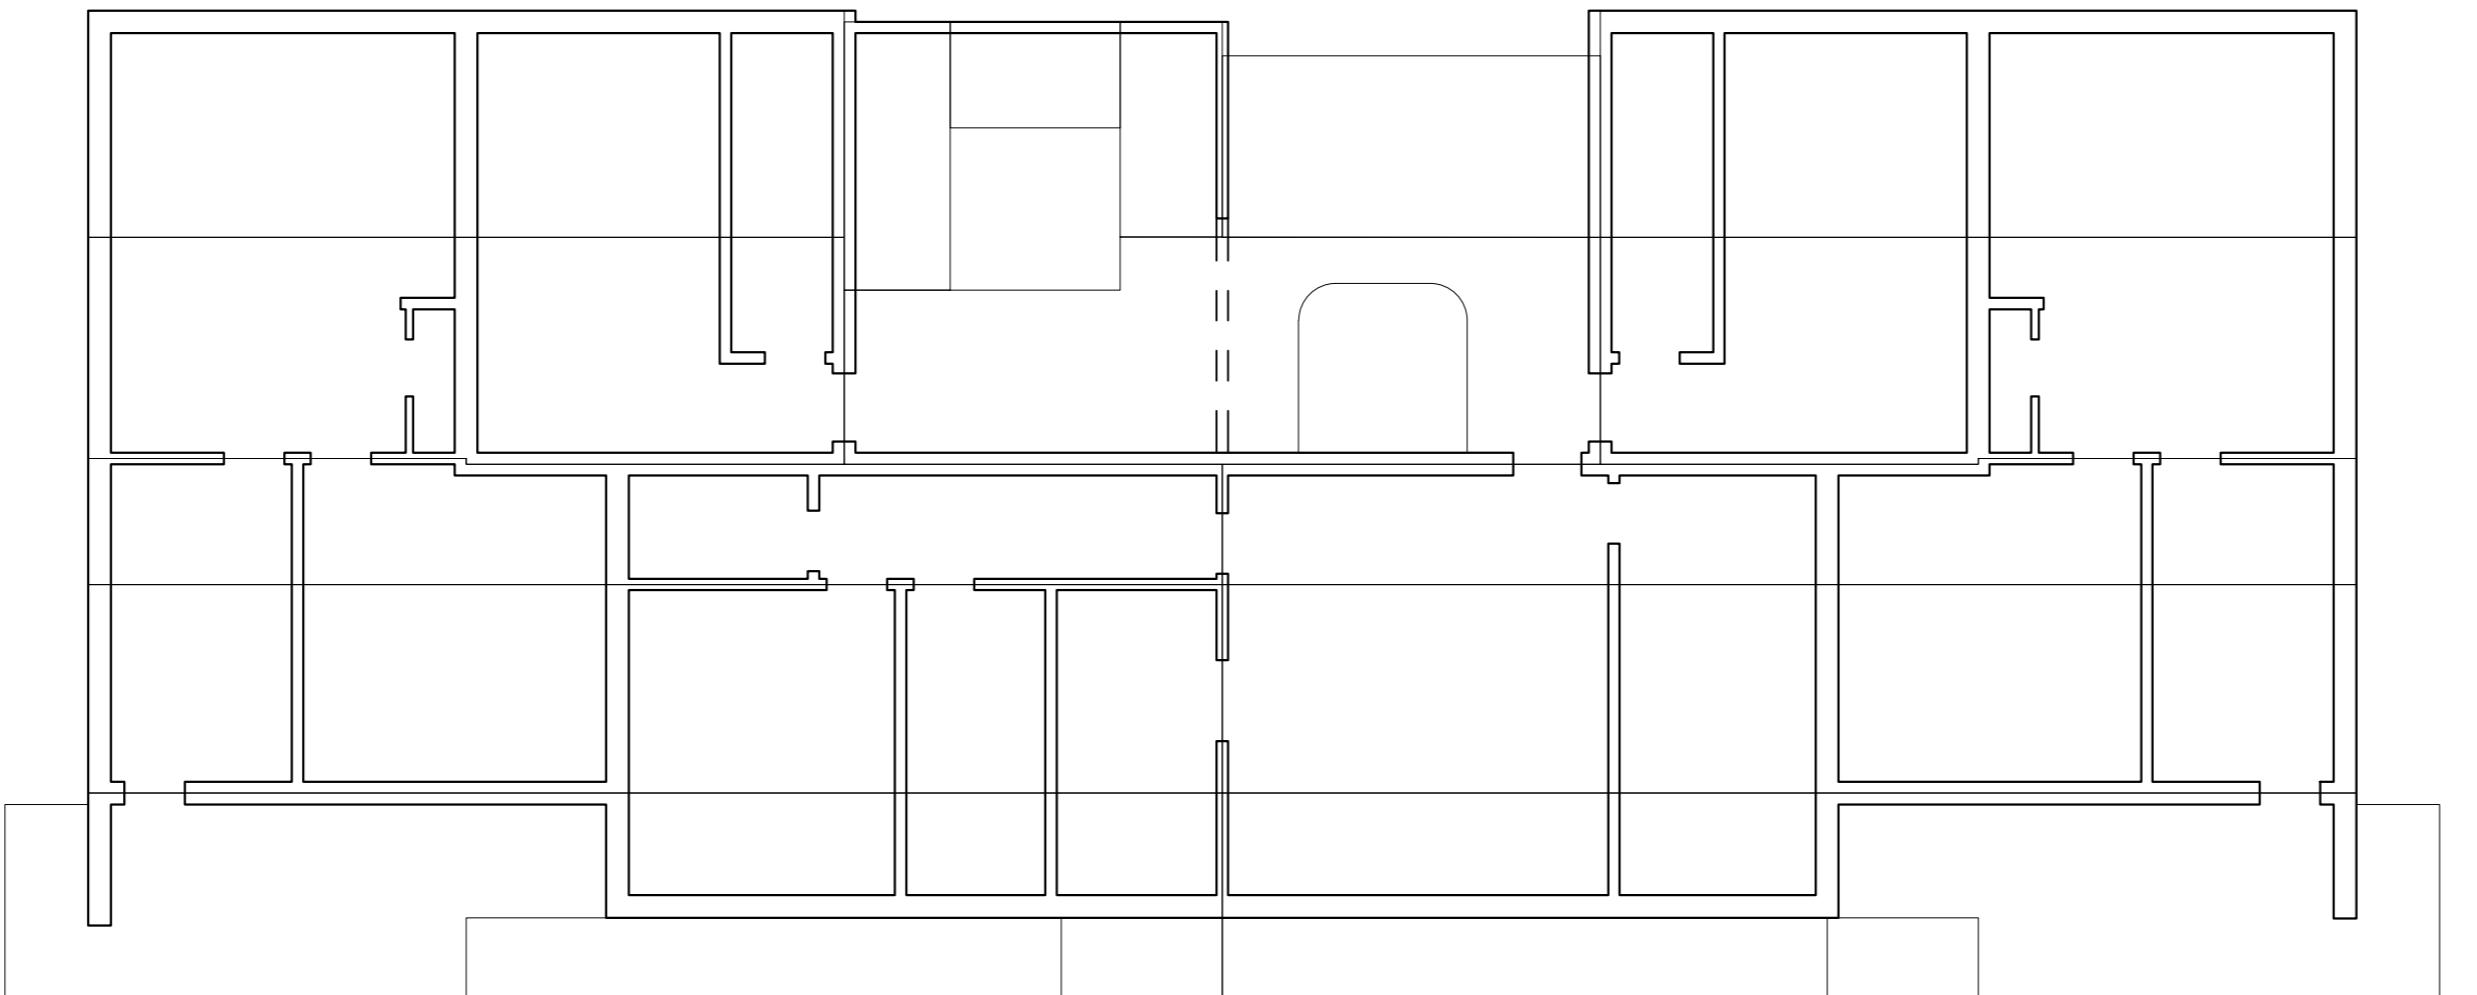

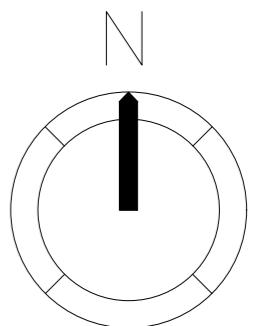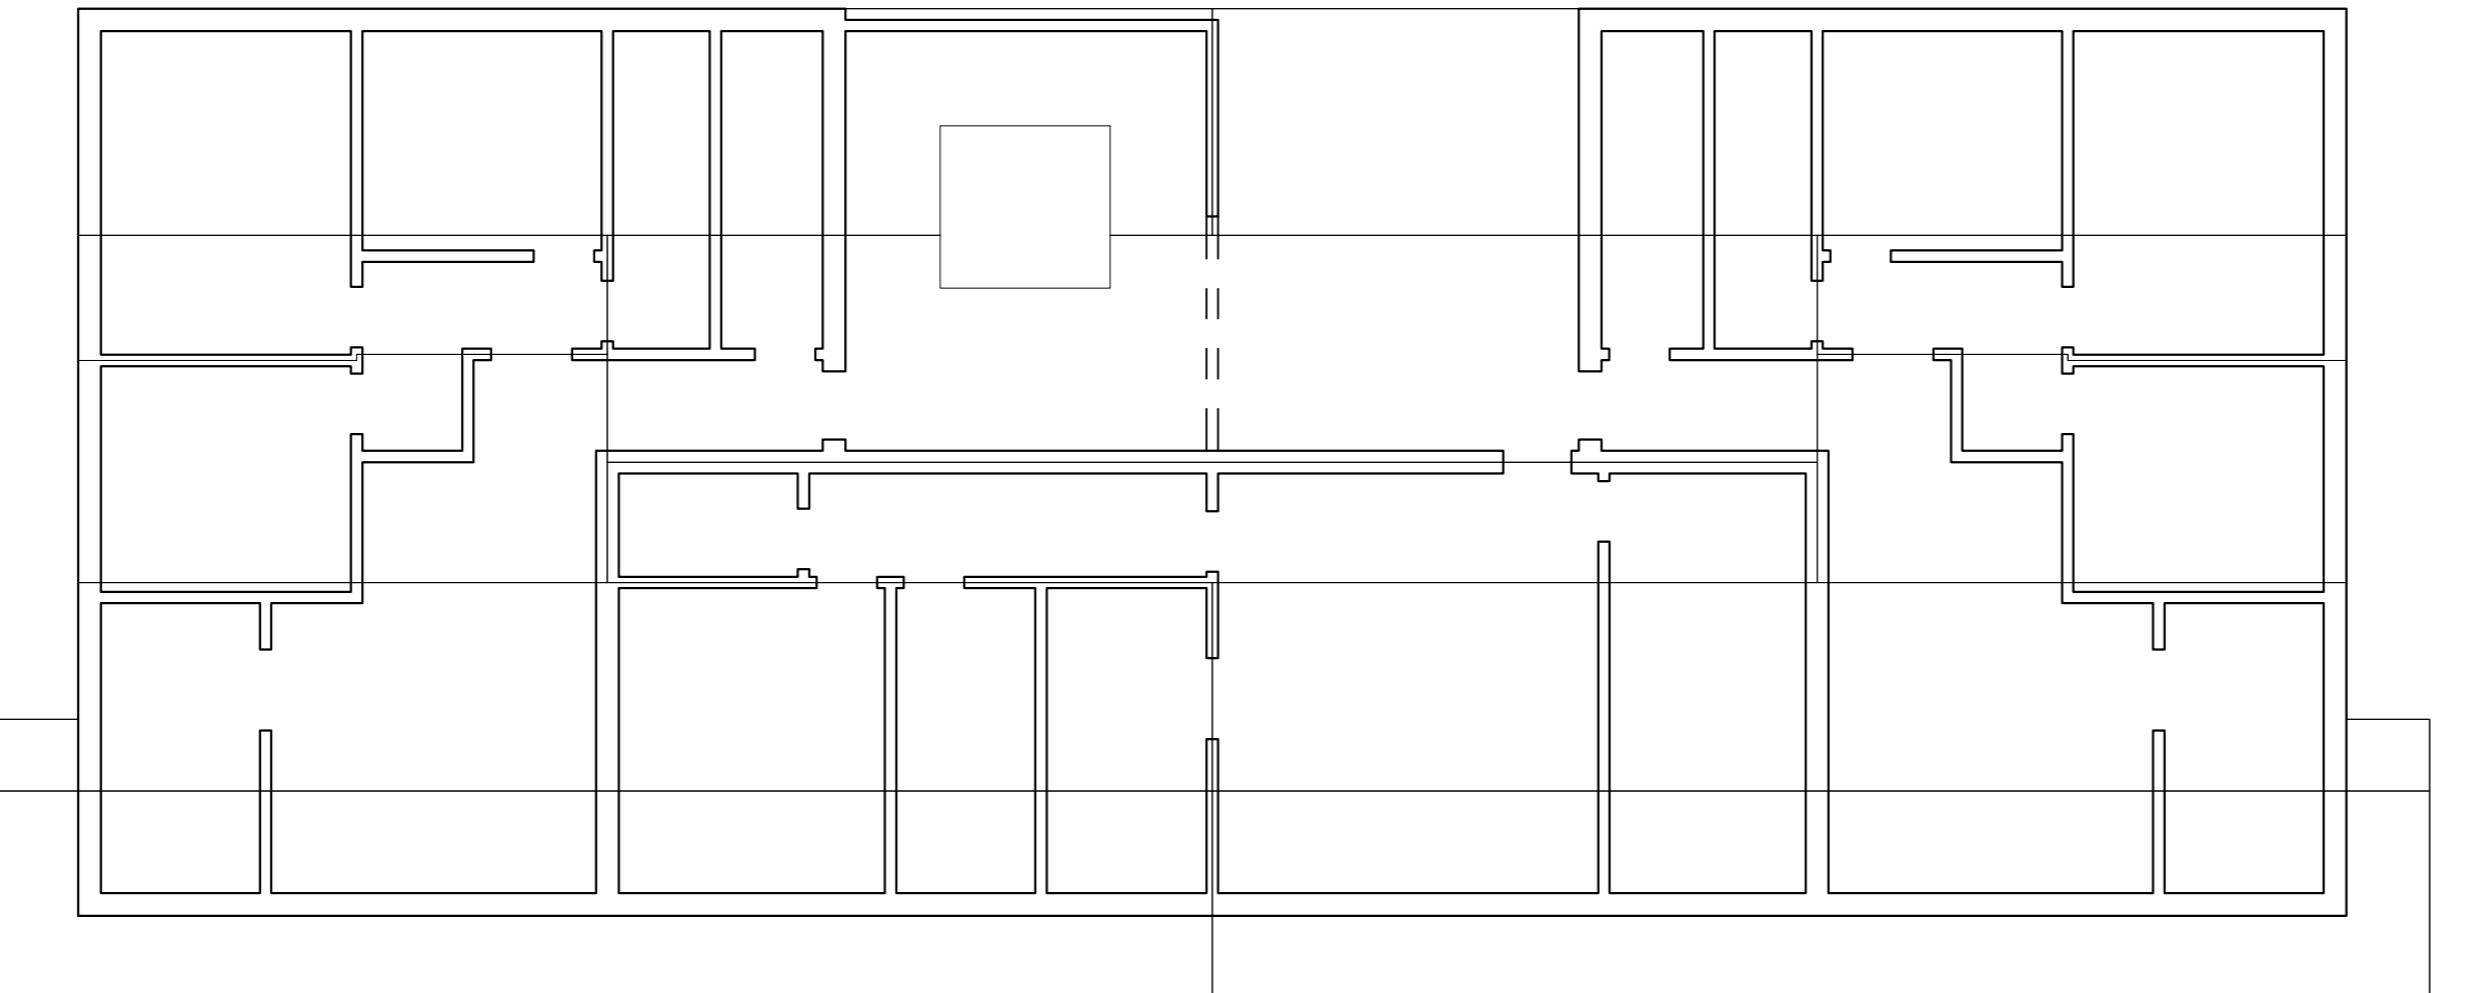

**CARPENTERIA PAVIMENTO
TERRAZZO
TAVOLA 22**

Scala 1:100

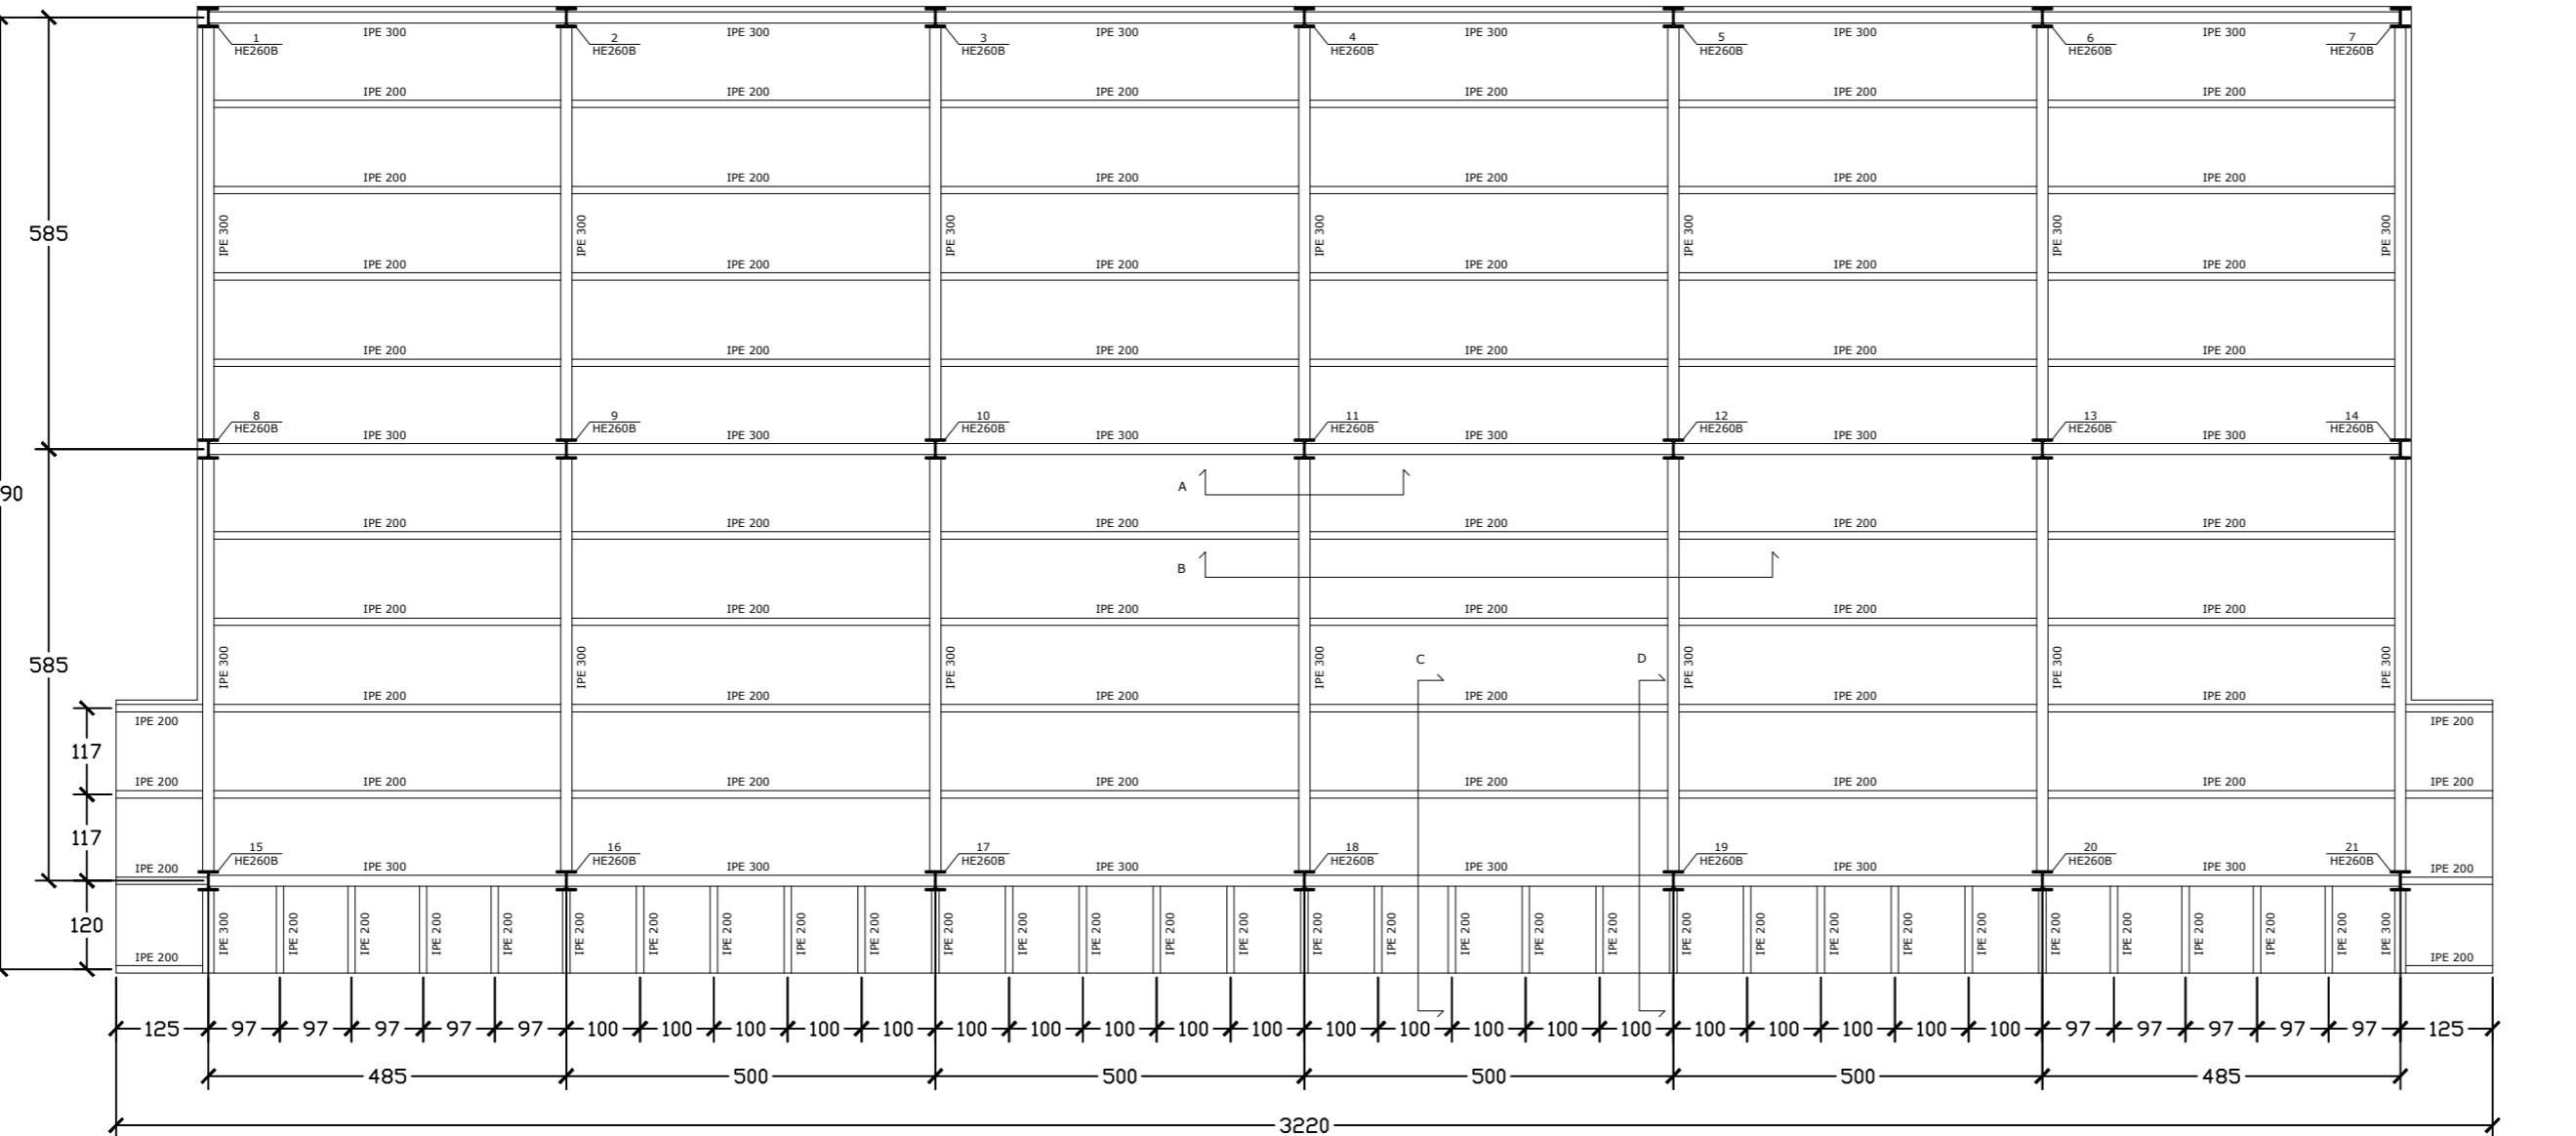



Università degli Studi di Catania

Dipartimento di Ingegneria Civile e Architettura
Corso di Laurea in Ingegneria Edile e Architettura


ARCHITETTURA TECNICA II E LABORATORIO
PROGETTUALE a.a. 2019-2020

Docenti: Vincenzo Sapienza, Gaetano Sciuto
Gruppo: Andrea Longhitano, Frenacesco Lomeo,
Giovanni Terranova

Progetto di un edificio a destinazione
residenziale e commerciale

DETTAGLIO CARPENTERIA
1 di 4
TAVOLA 22a

Scala 1:20

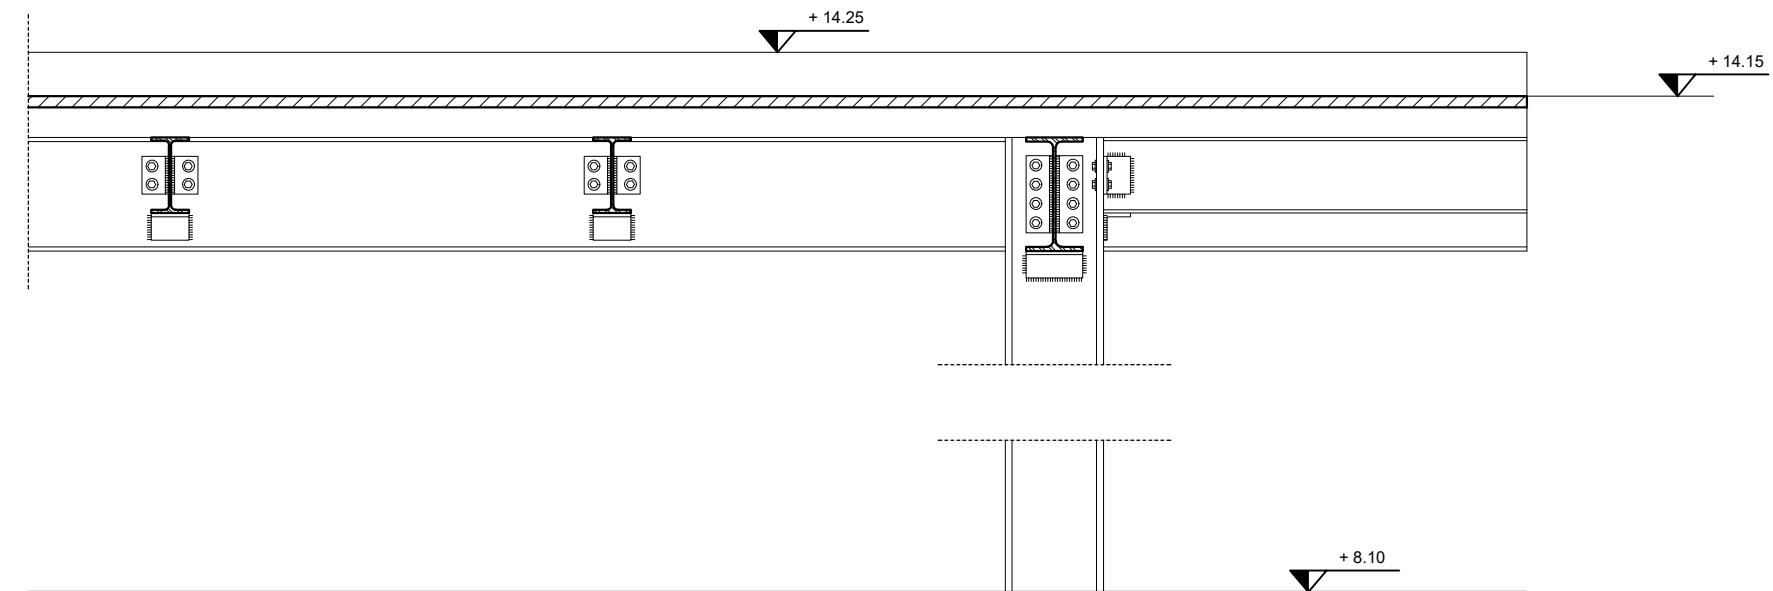



Università degli Studi di Catania

Dipartimento di Ingegneria Civile e Architettura
Corso di Laurea in Ingegneria Edile e Architettura


ARCHITETTURA TECNICA II E LABORATORIO
PROGETTUALE a.a. 2019-2020

Docenti: Vincenzo Sapienza, Gaetano Sciuto
Gruppo: Andrea Longhitano, Frenacesco Lomeo,
Giovanni Terranova

Progetto di un edificio a destinazione
residenziale e commerciale

DETTAGLIO CARPENTERIA
2 di 4
TAVOLA 22b

Scala 1:20

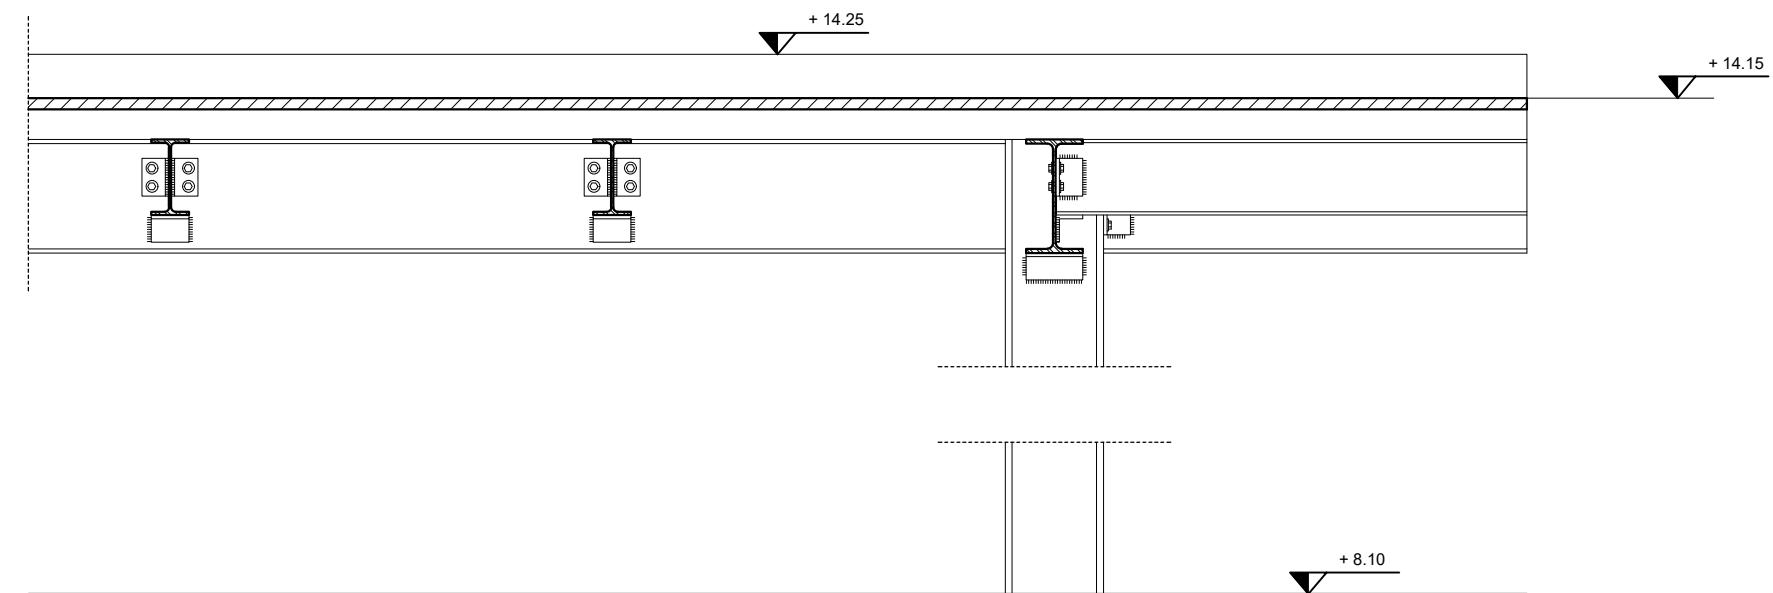



Università degli Studi di Catania

Dipartimento di Ingegneria Civile e Architettura
Corso di Laurea in Ingegneria Edile e Architettura


ARCHITETTURA TECNICA II E LABORATORIO
PROGETTUALE a.a. 2019-2020

Docenti: Vincenzo Sapienza, Gaetano Sciuto
Gruppo: Andrea Longhitano, Frenacesco Lomeo,
Giovanni Terranova

Progetto di un edificio a destinazione
residenziale e commerciale

DETTAGLIO CARPENTERIA
3 di 4
TAVOLA 22c

Scala 1:20

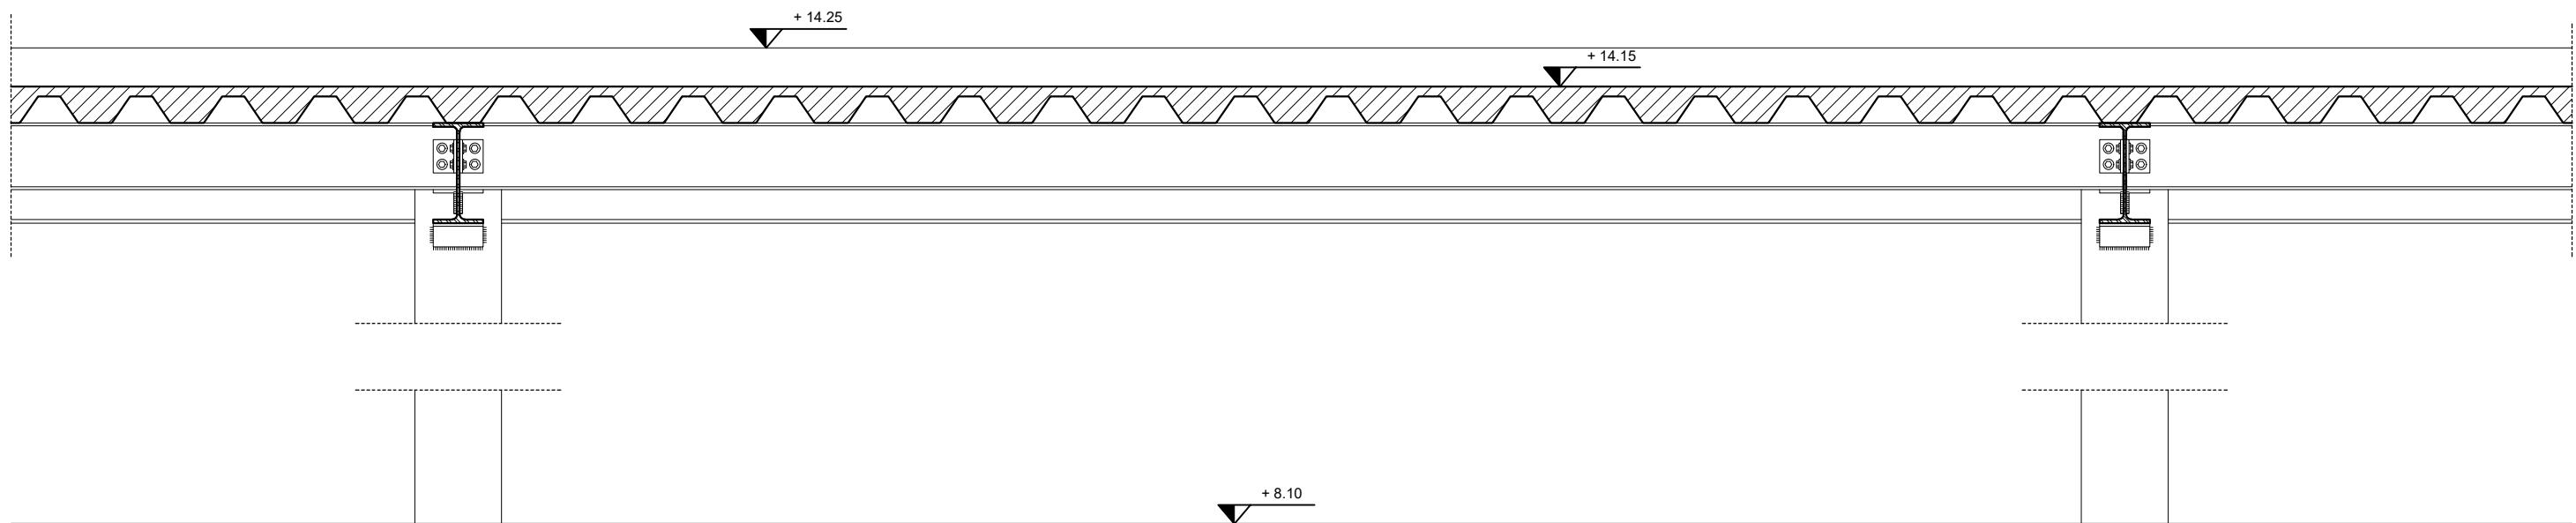



Università degli Studi di Catania

Dipartimento di Ingegneria Civile e Architettura
Corso di Laurea in Ingegneria Edile e Architettura


ARCHITETTURA TECNICA II E LABORATORIO
PROGETUALE a.a. 2019-2020


Docenti: Vincenzo Sapienza, Gaetano Sciuto
Gruppo: Andrea Longhitano, Frenacesco Lomeo,
Giovanni Terranova

Progetto di un edificio a destinazione
residenziale e commerciale

DETTAGLIO CARPENTERIA
4 di 4
TAVOLA 22d

Scala 1:20

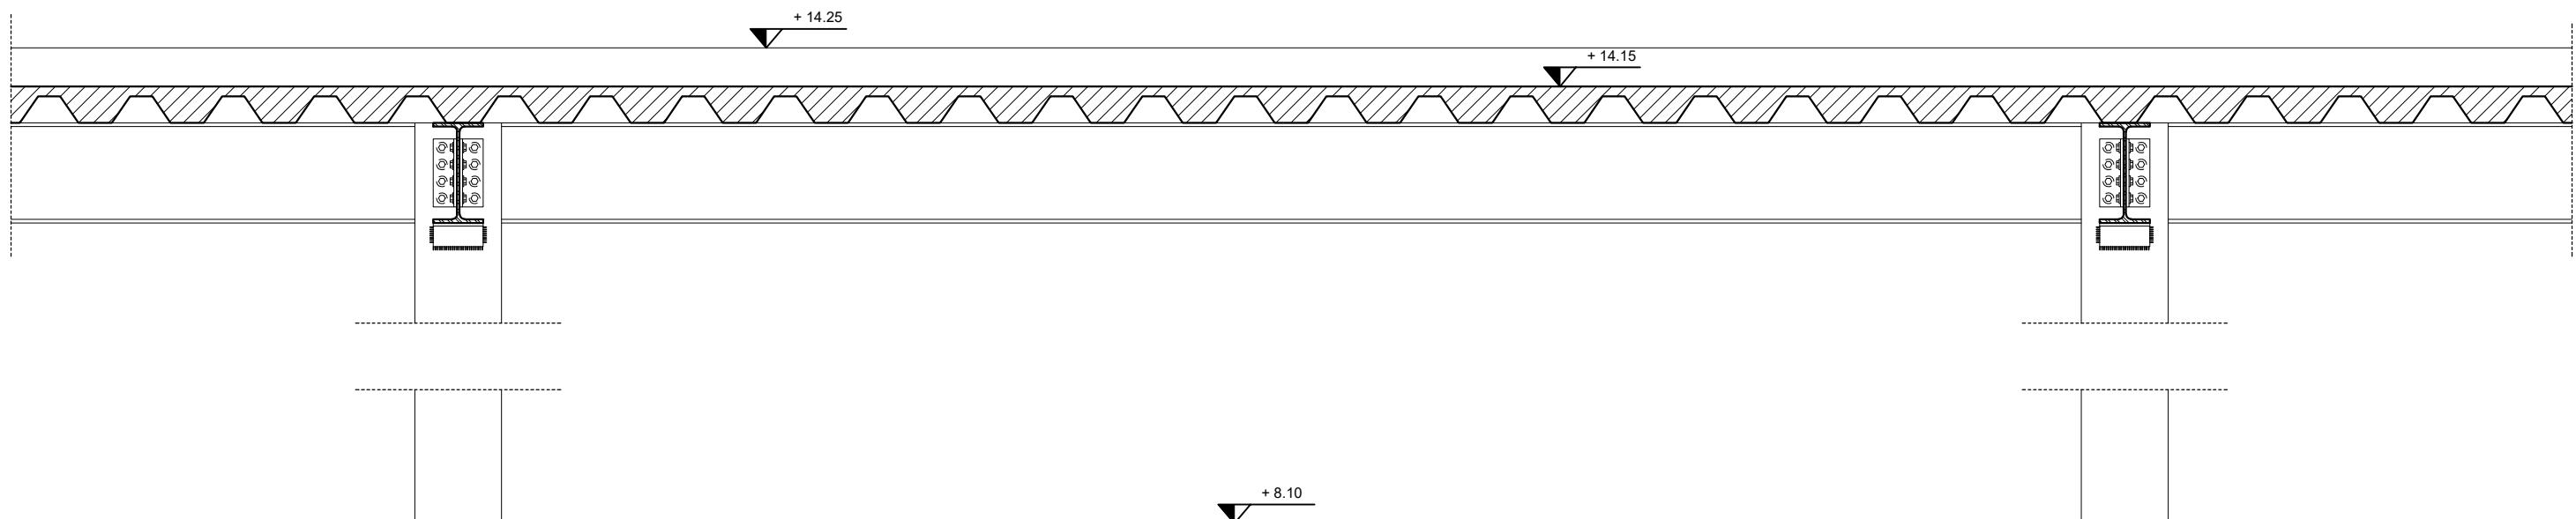


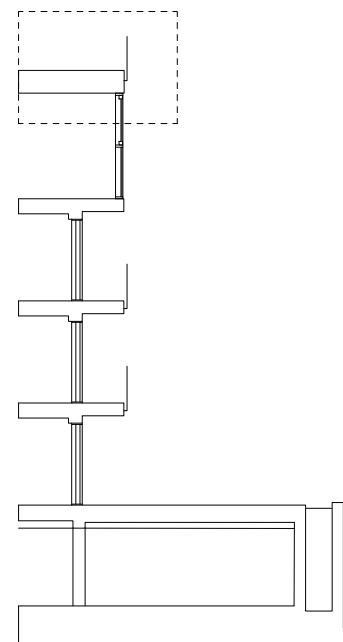ARCHITETTURA TECNICA II E LABORATORIO
PROGETTUALE a.a. 2019-2020Docenti: Vincenzo Sapienza, Gaetano Sciuto
Gruppo: Andrea Longhitano, Frenacesco Lomeo,
Giovanni TerranovaProgetto di un edificio a destinazione
residenziale e commerciale

DETTAGLIO 1 di 10

TAVOLA 23

Scala 1:10

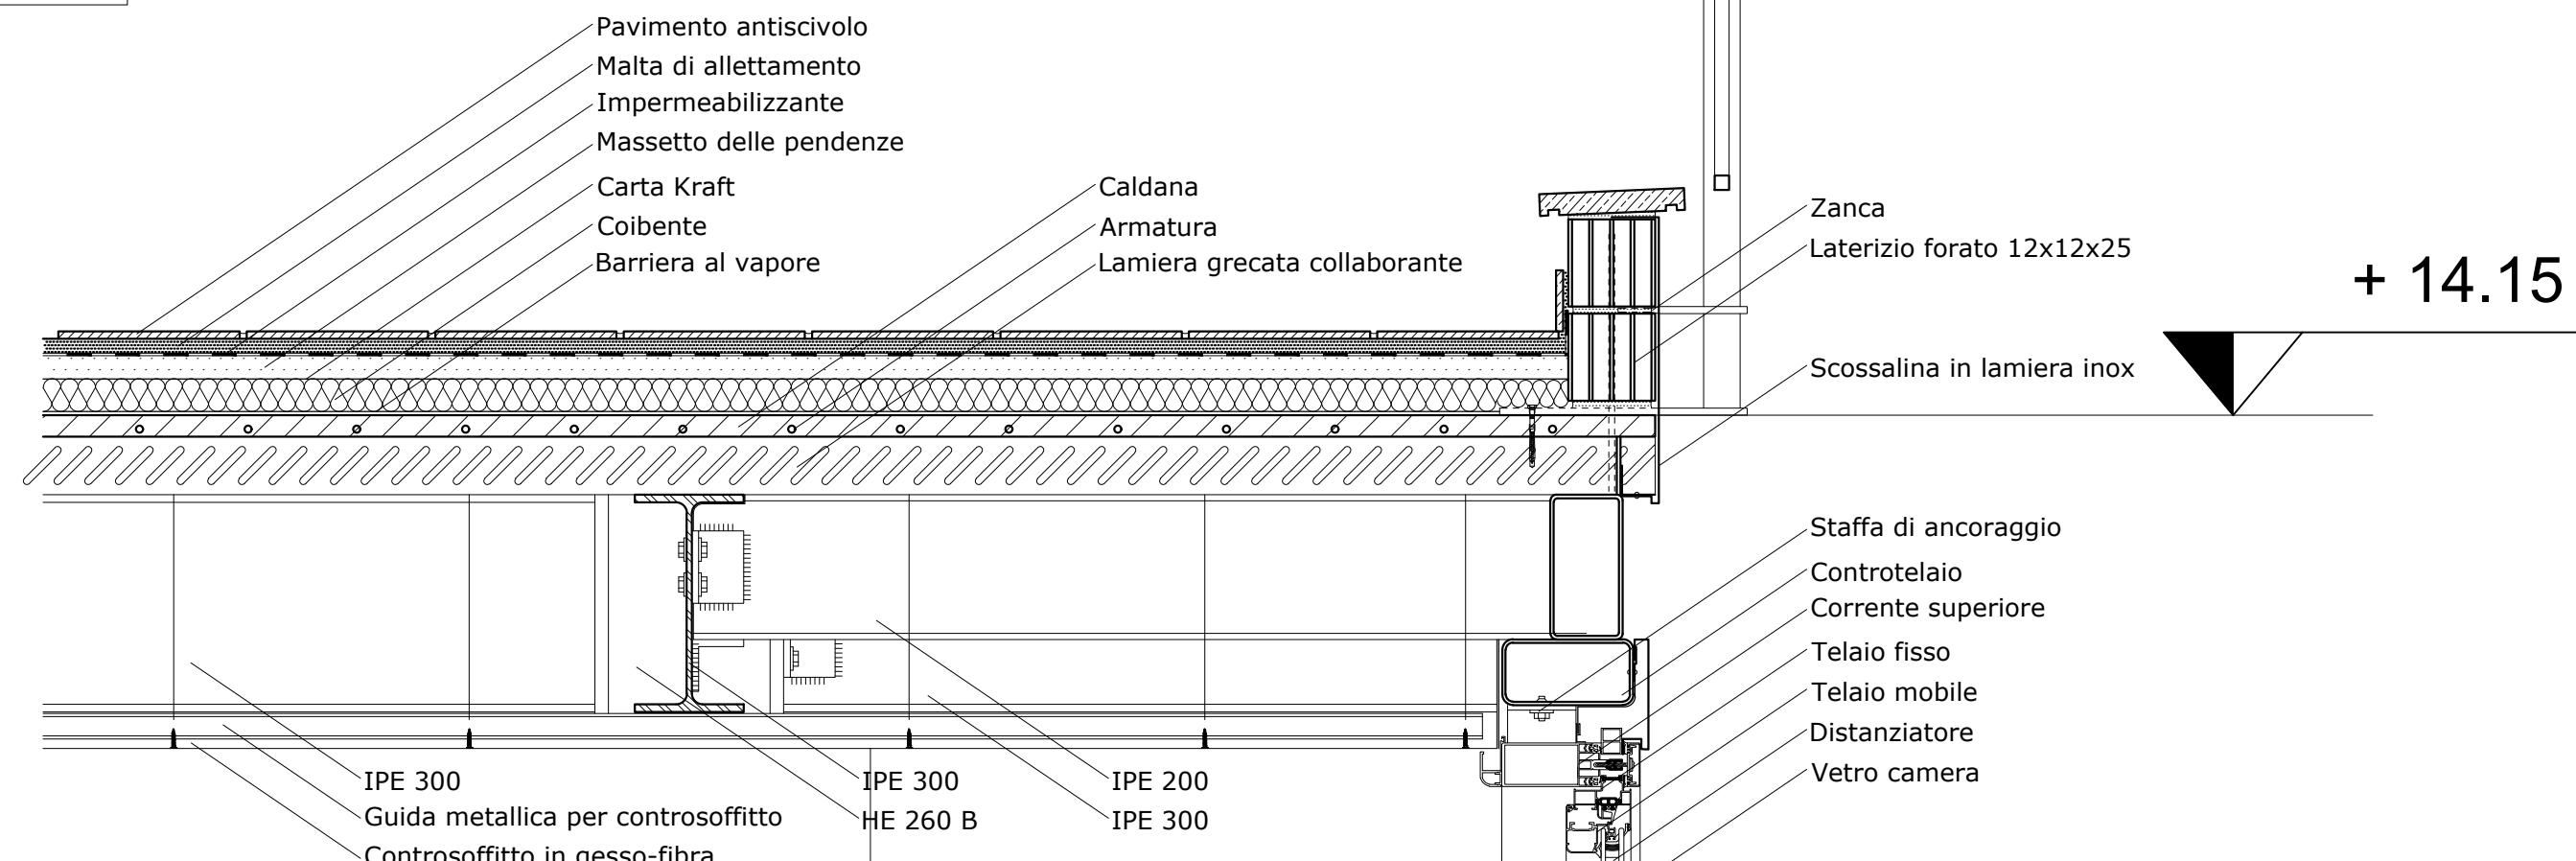



Università degli Studi di Catania

Dipartimento di Ingegneria Civile e Architettura
Corso di Laurea in Ingegneria Edile e Architettura

ARCHITETTURA TECNICA II E LABORATORIO
PROGETTUALE a.a. 2019-2020


Docenti: Vincenzo Sapienza, Gaetano Sciuto
Gruppo: Andrea Longhitano, Frenacesco Lomeo,
Giovanni Terranova


Progetto di un edificio a destinazione
residenziale e commerciale


DETTAGLIO 2 di 10


TAVOLA 24

Scala 1:10

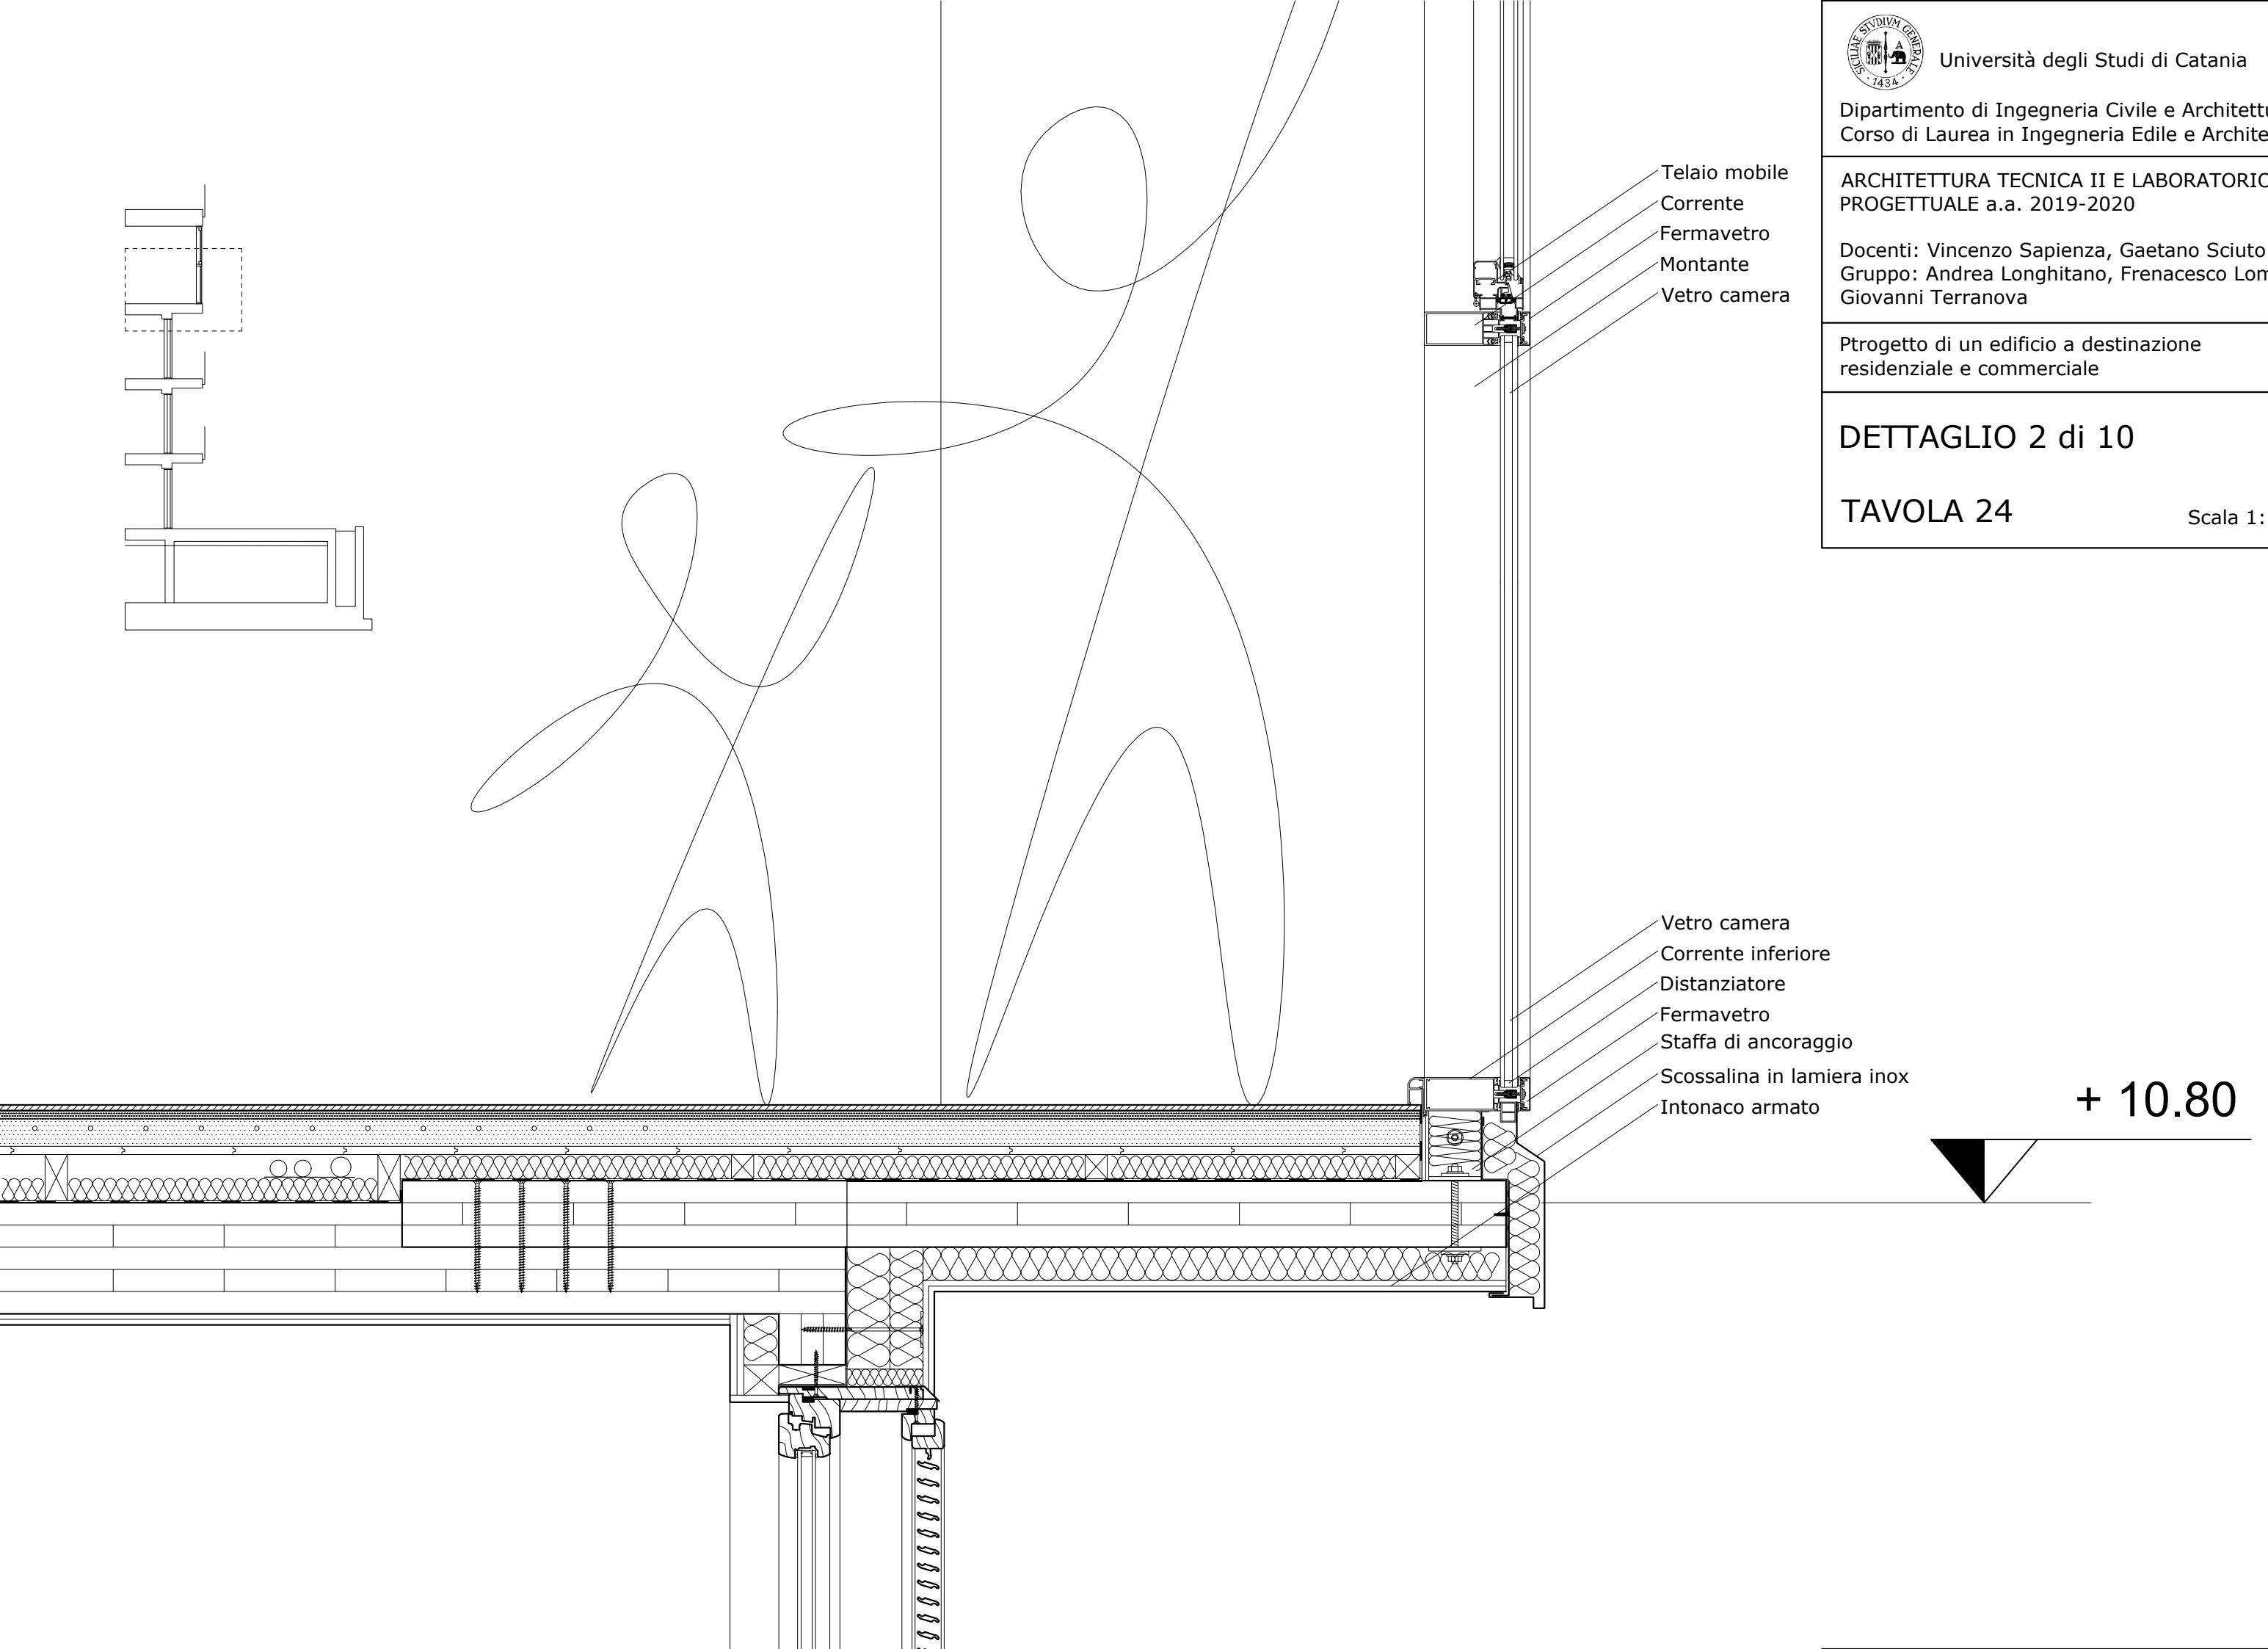

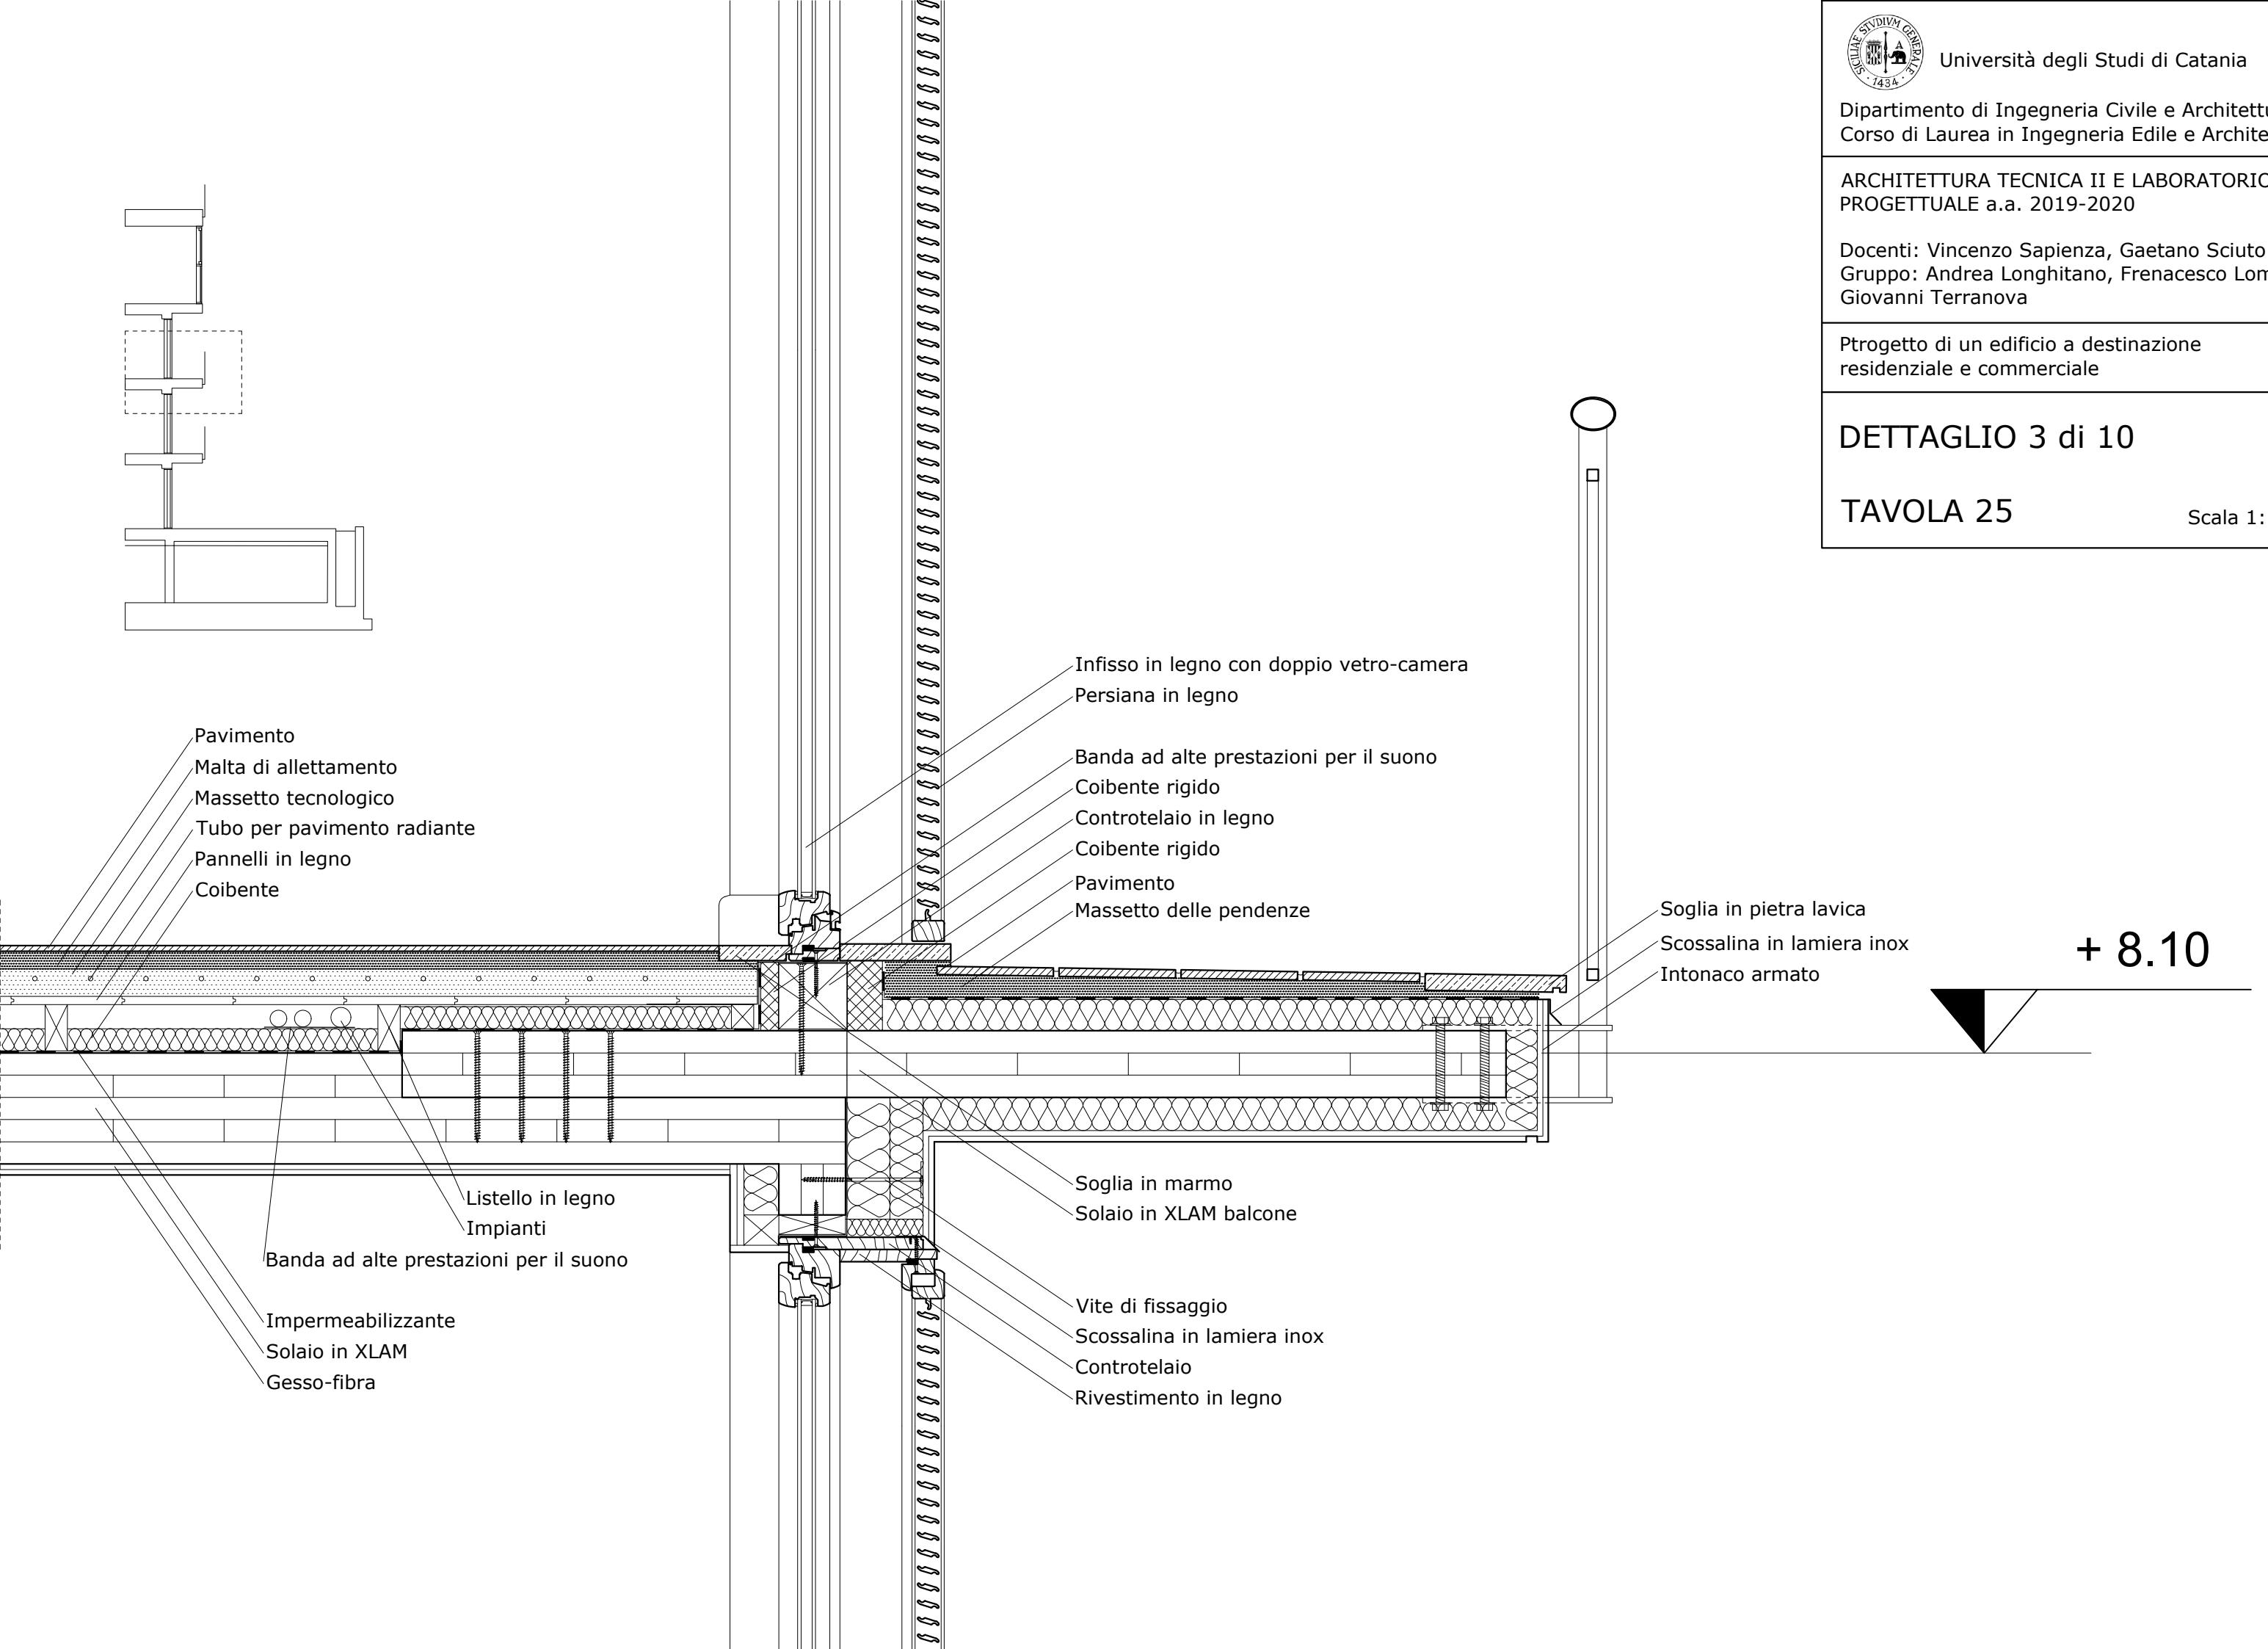

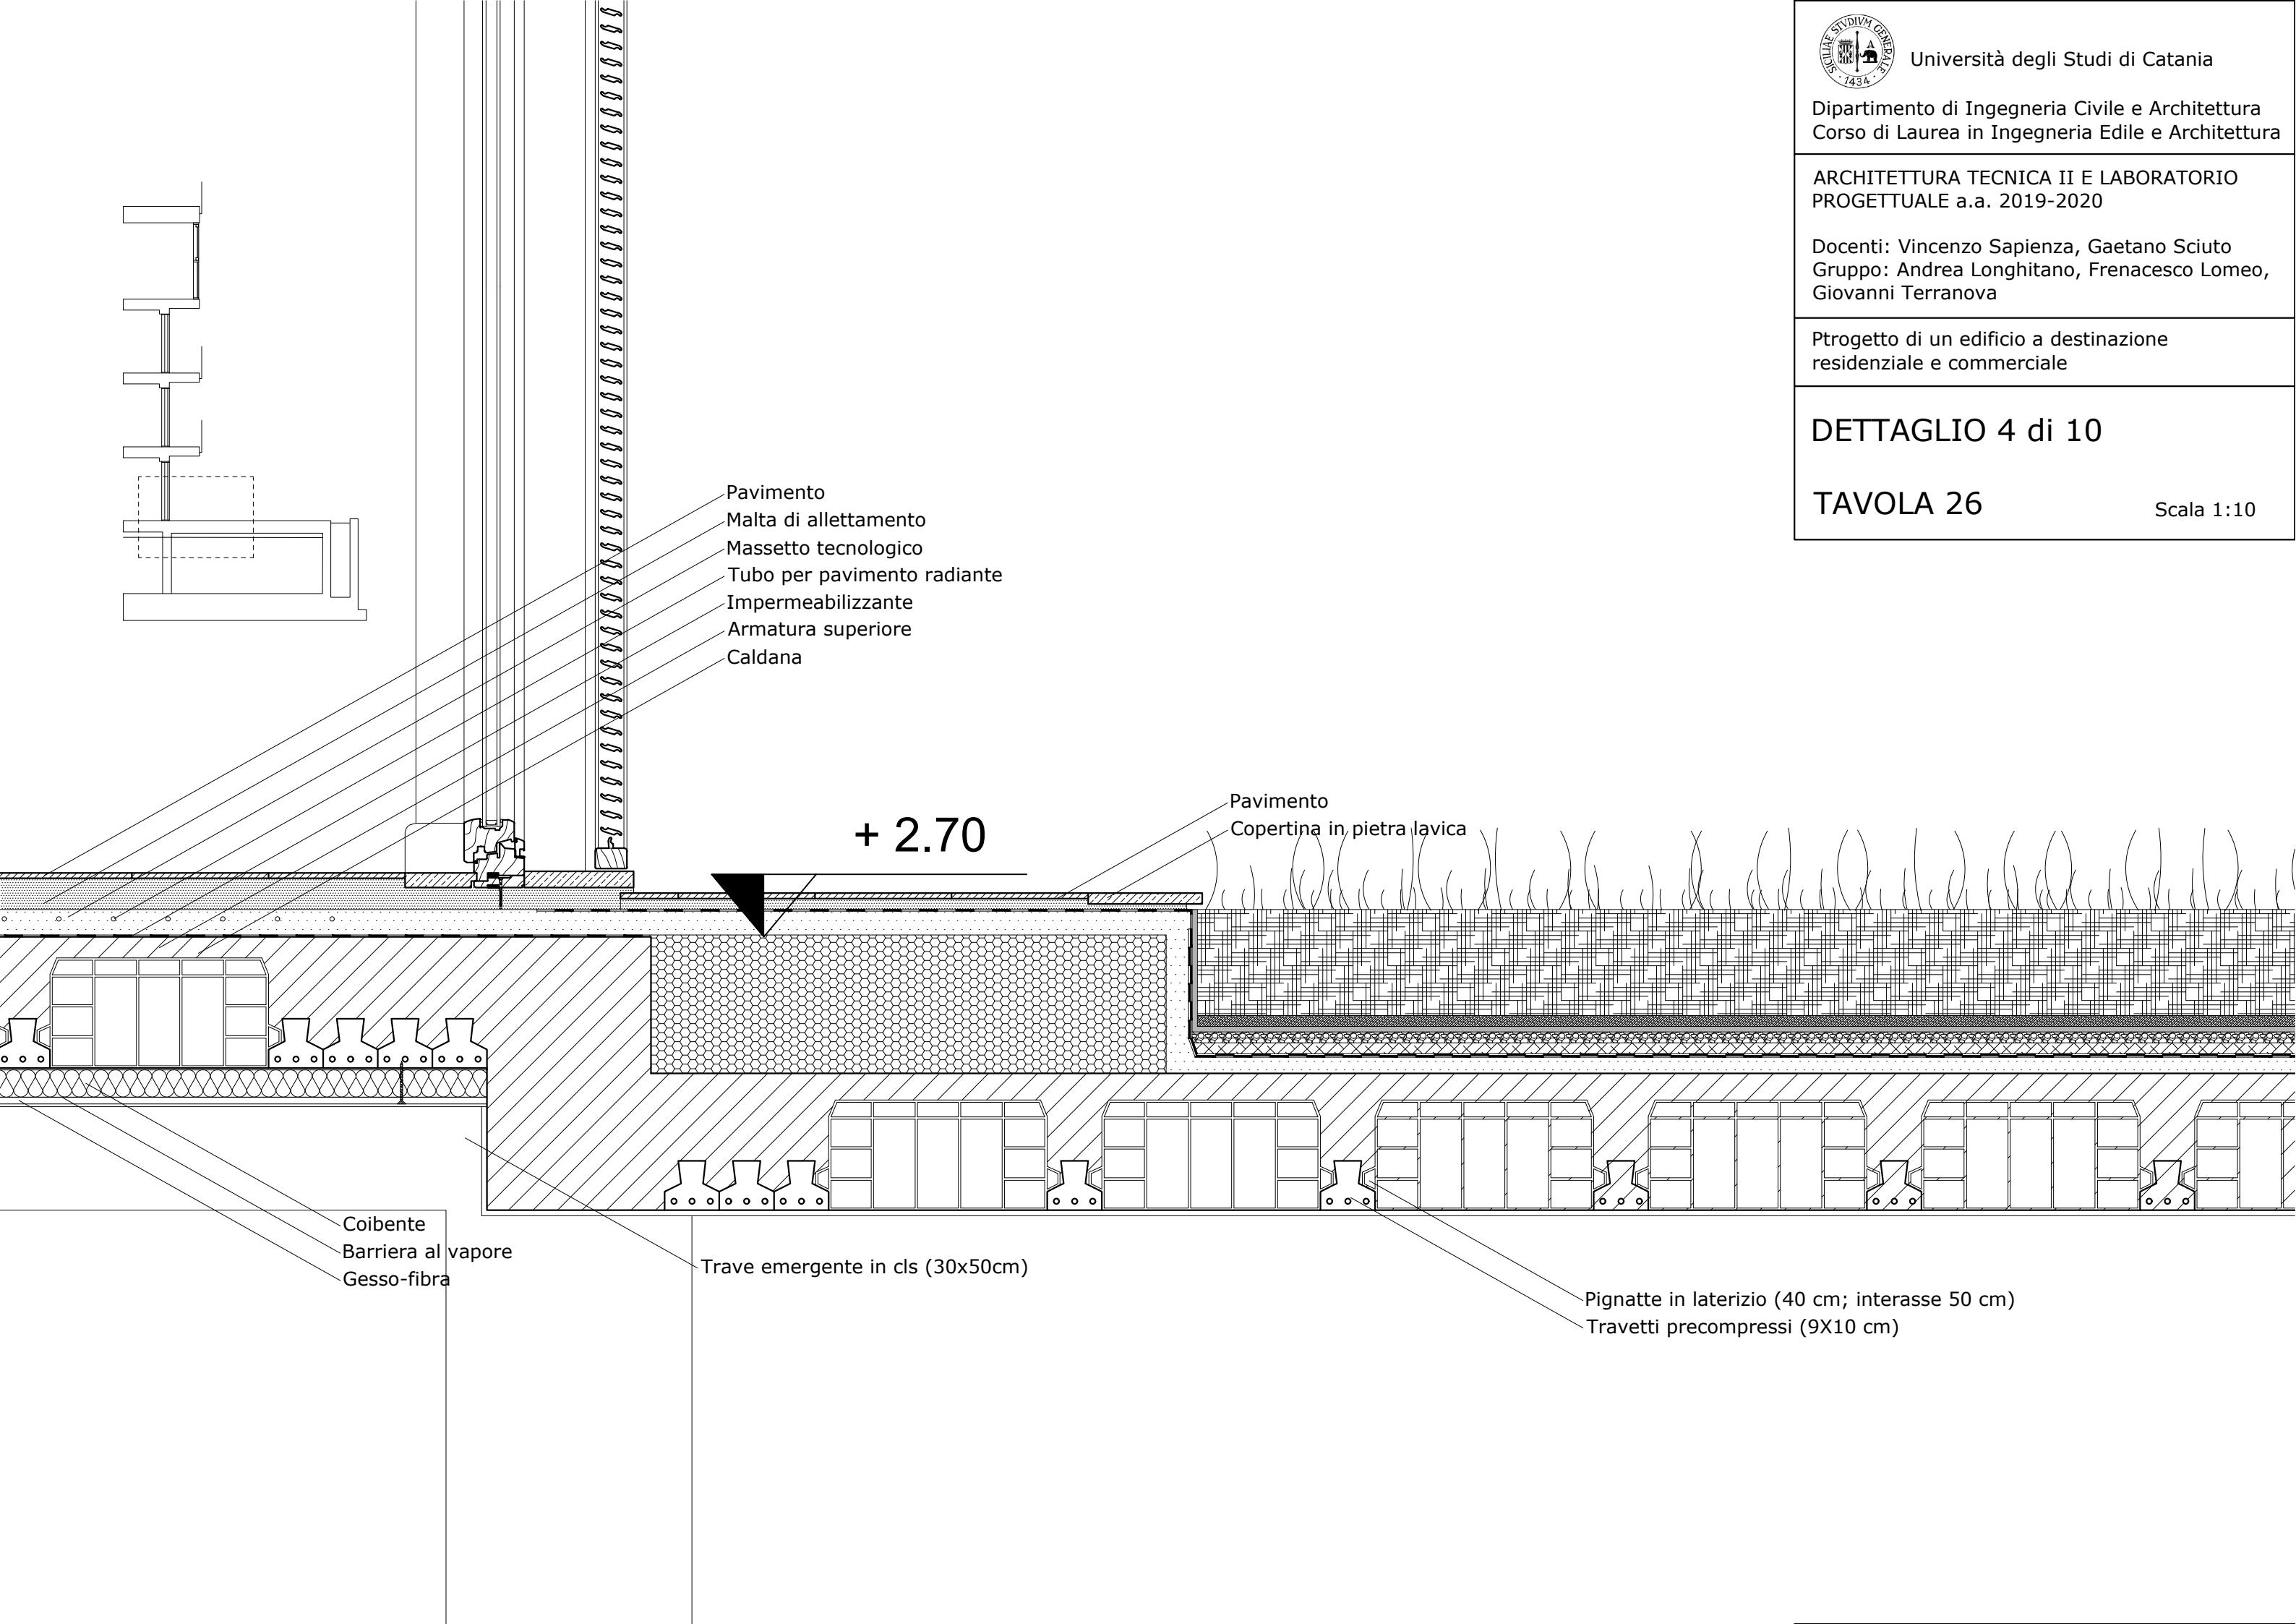

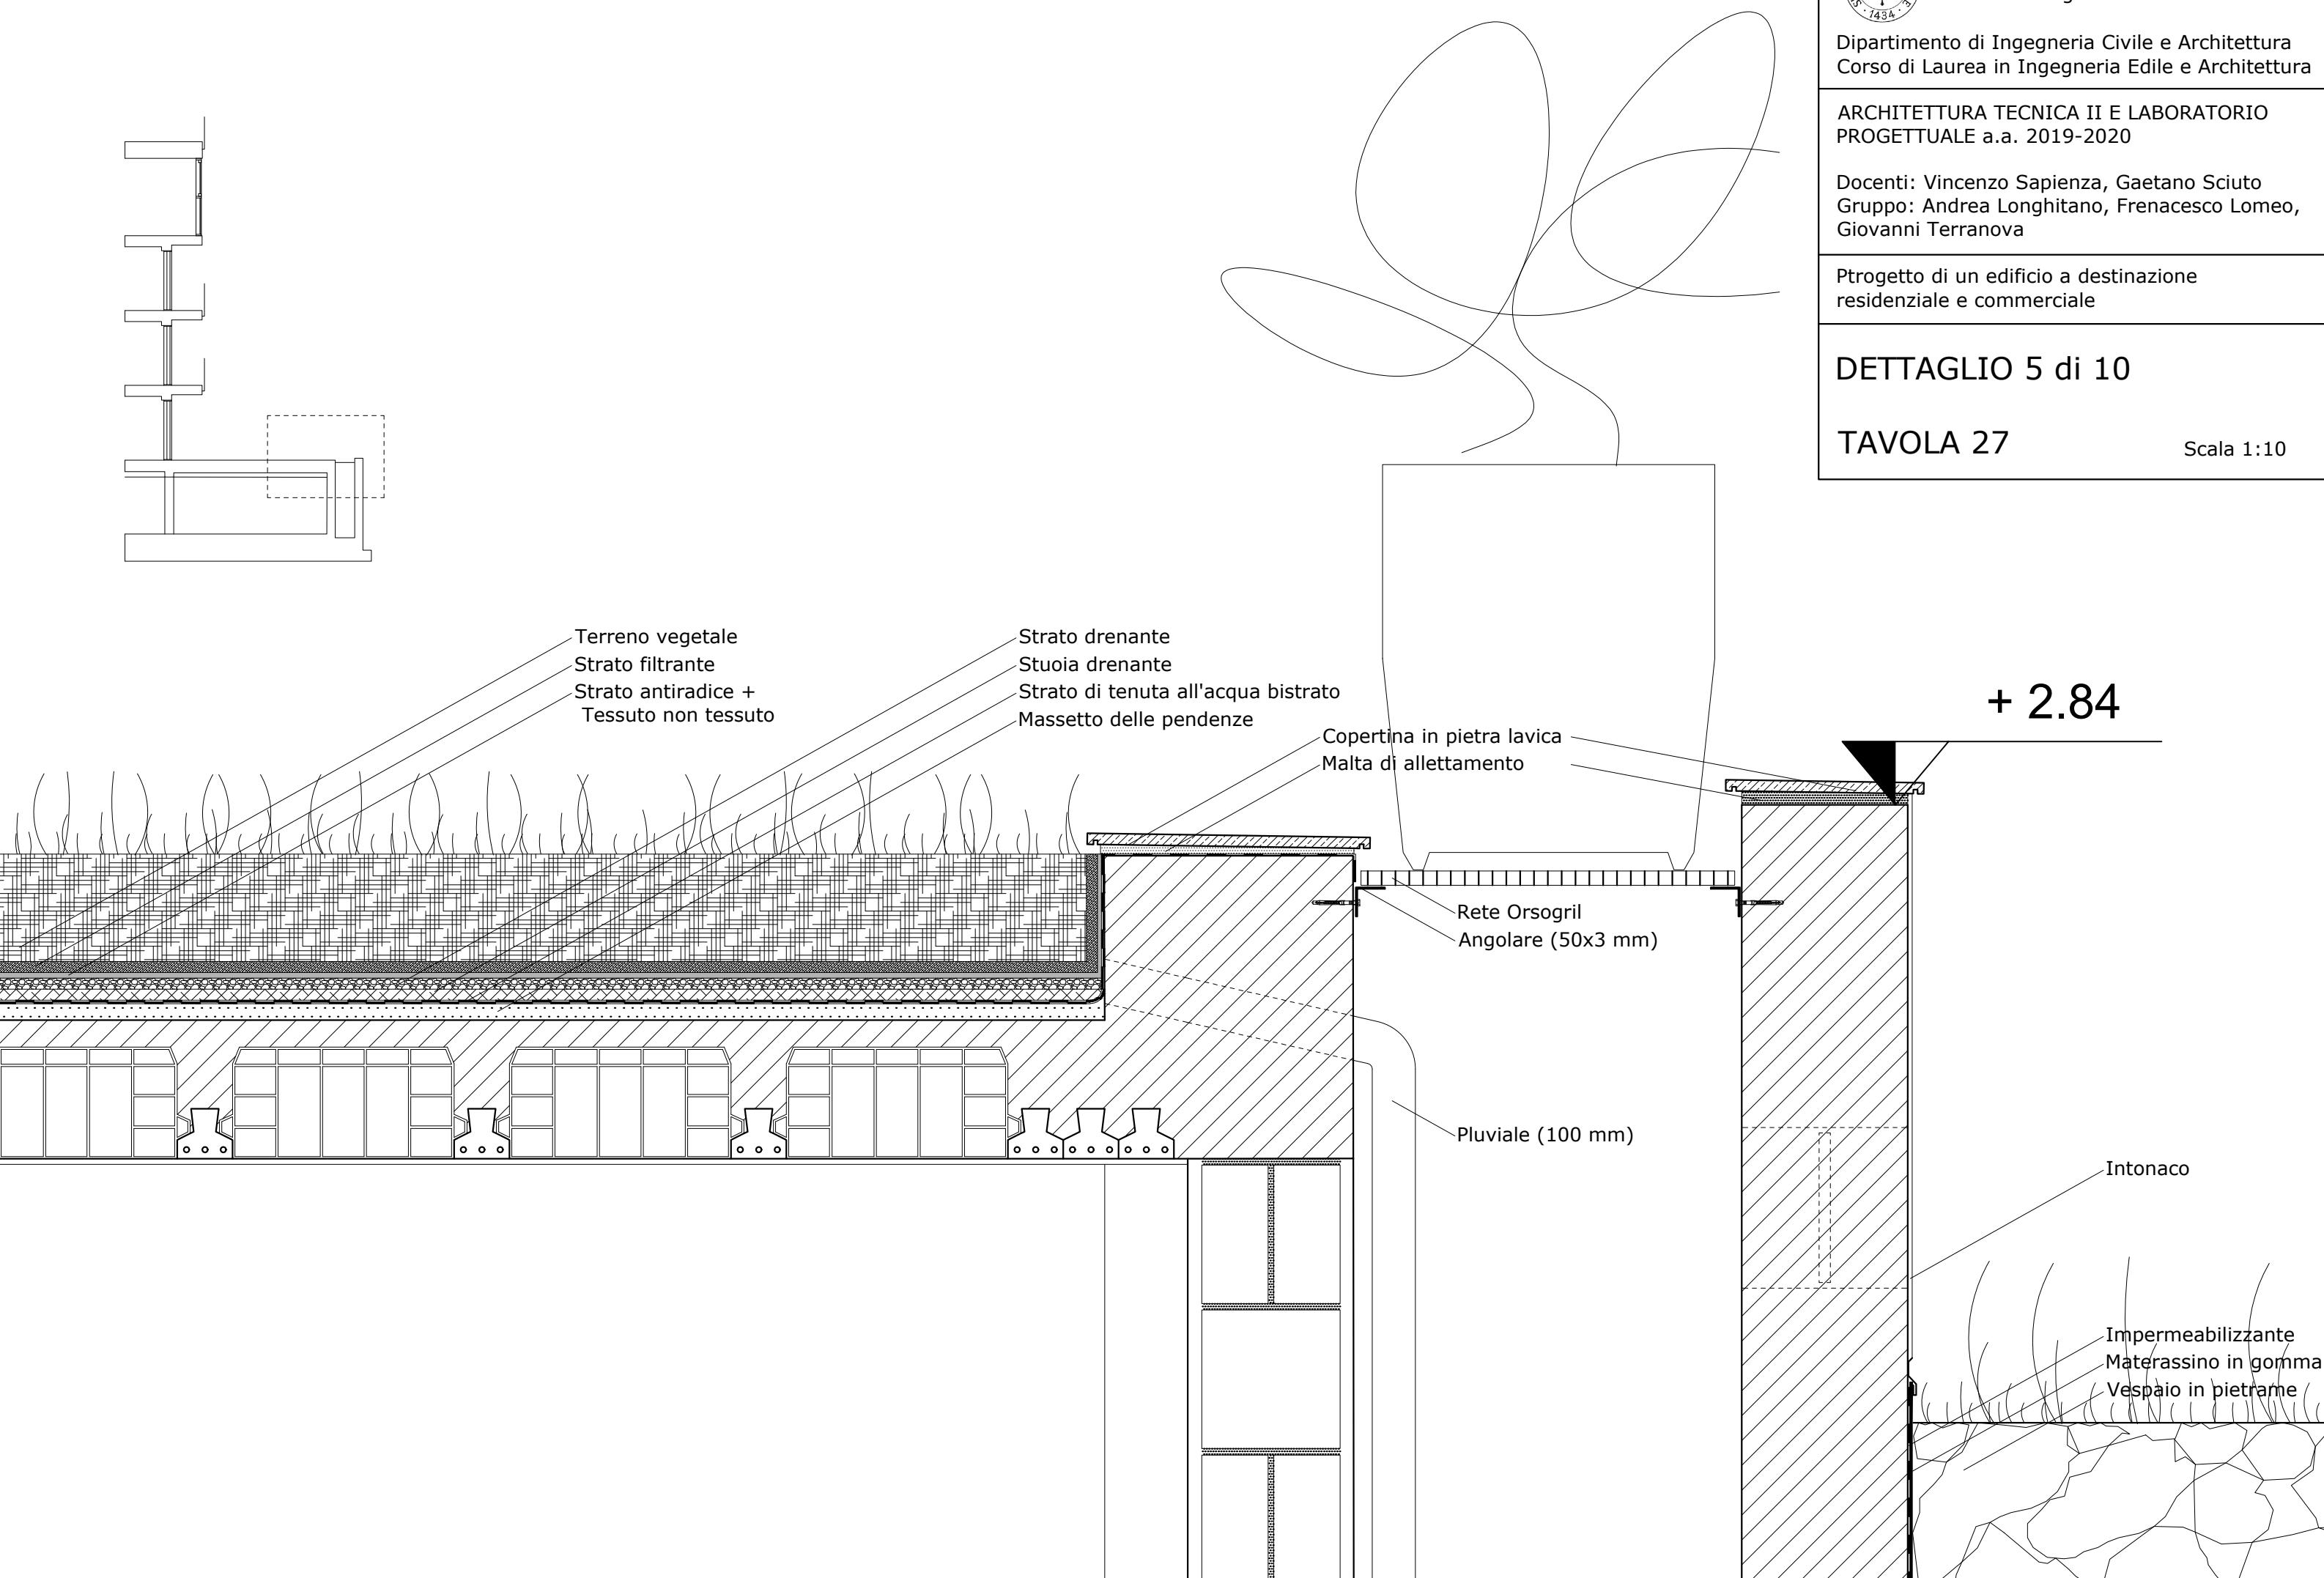



Università degli Studi di Catania

Dipartimento di Ingegneria Civile e Architettura
Corso di Laurea in Ingegneria Edile e Architettura

ARCHITETTURA TECNICA II E LABORATORIO
PROGETTUALE a.a. 2019-2020


Docenti: Vincenzo Sapienza, Gaetano Sciuto
Gruppo: Andrea Longhitano, Frenacesco Lomeo,
Giovanni Terranova

Progetto di un edificio a destinazione
residenziale e commerciale

DETTAGLIO 6 di 10

TAVOLA 28


Scala 1:10

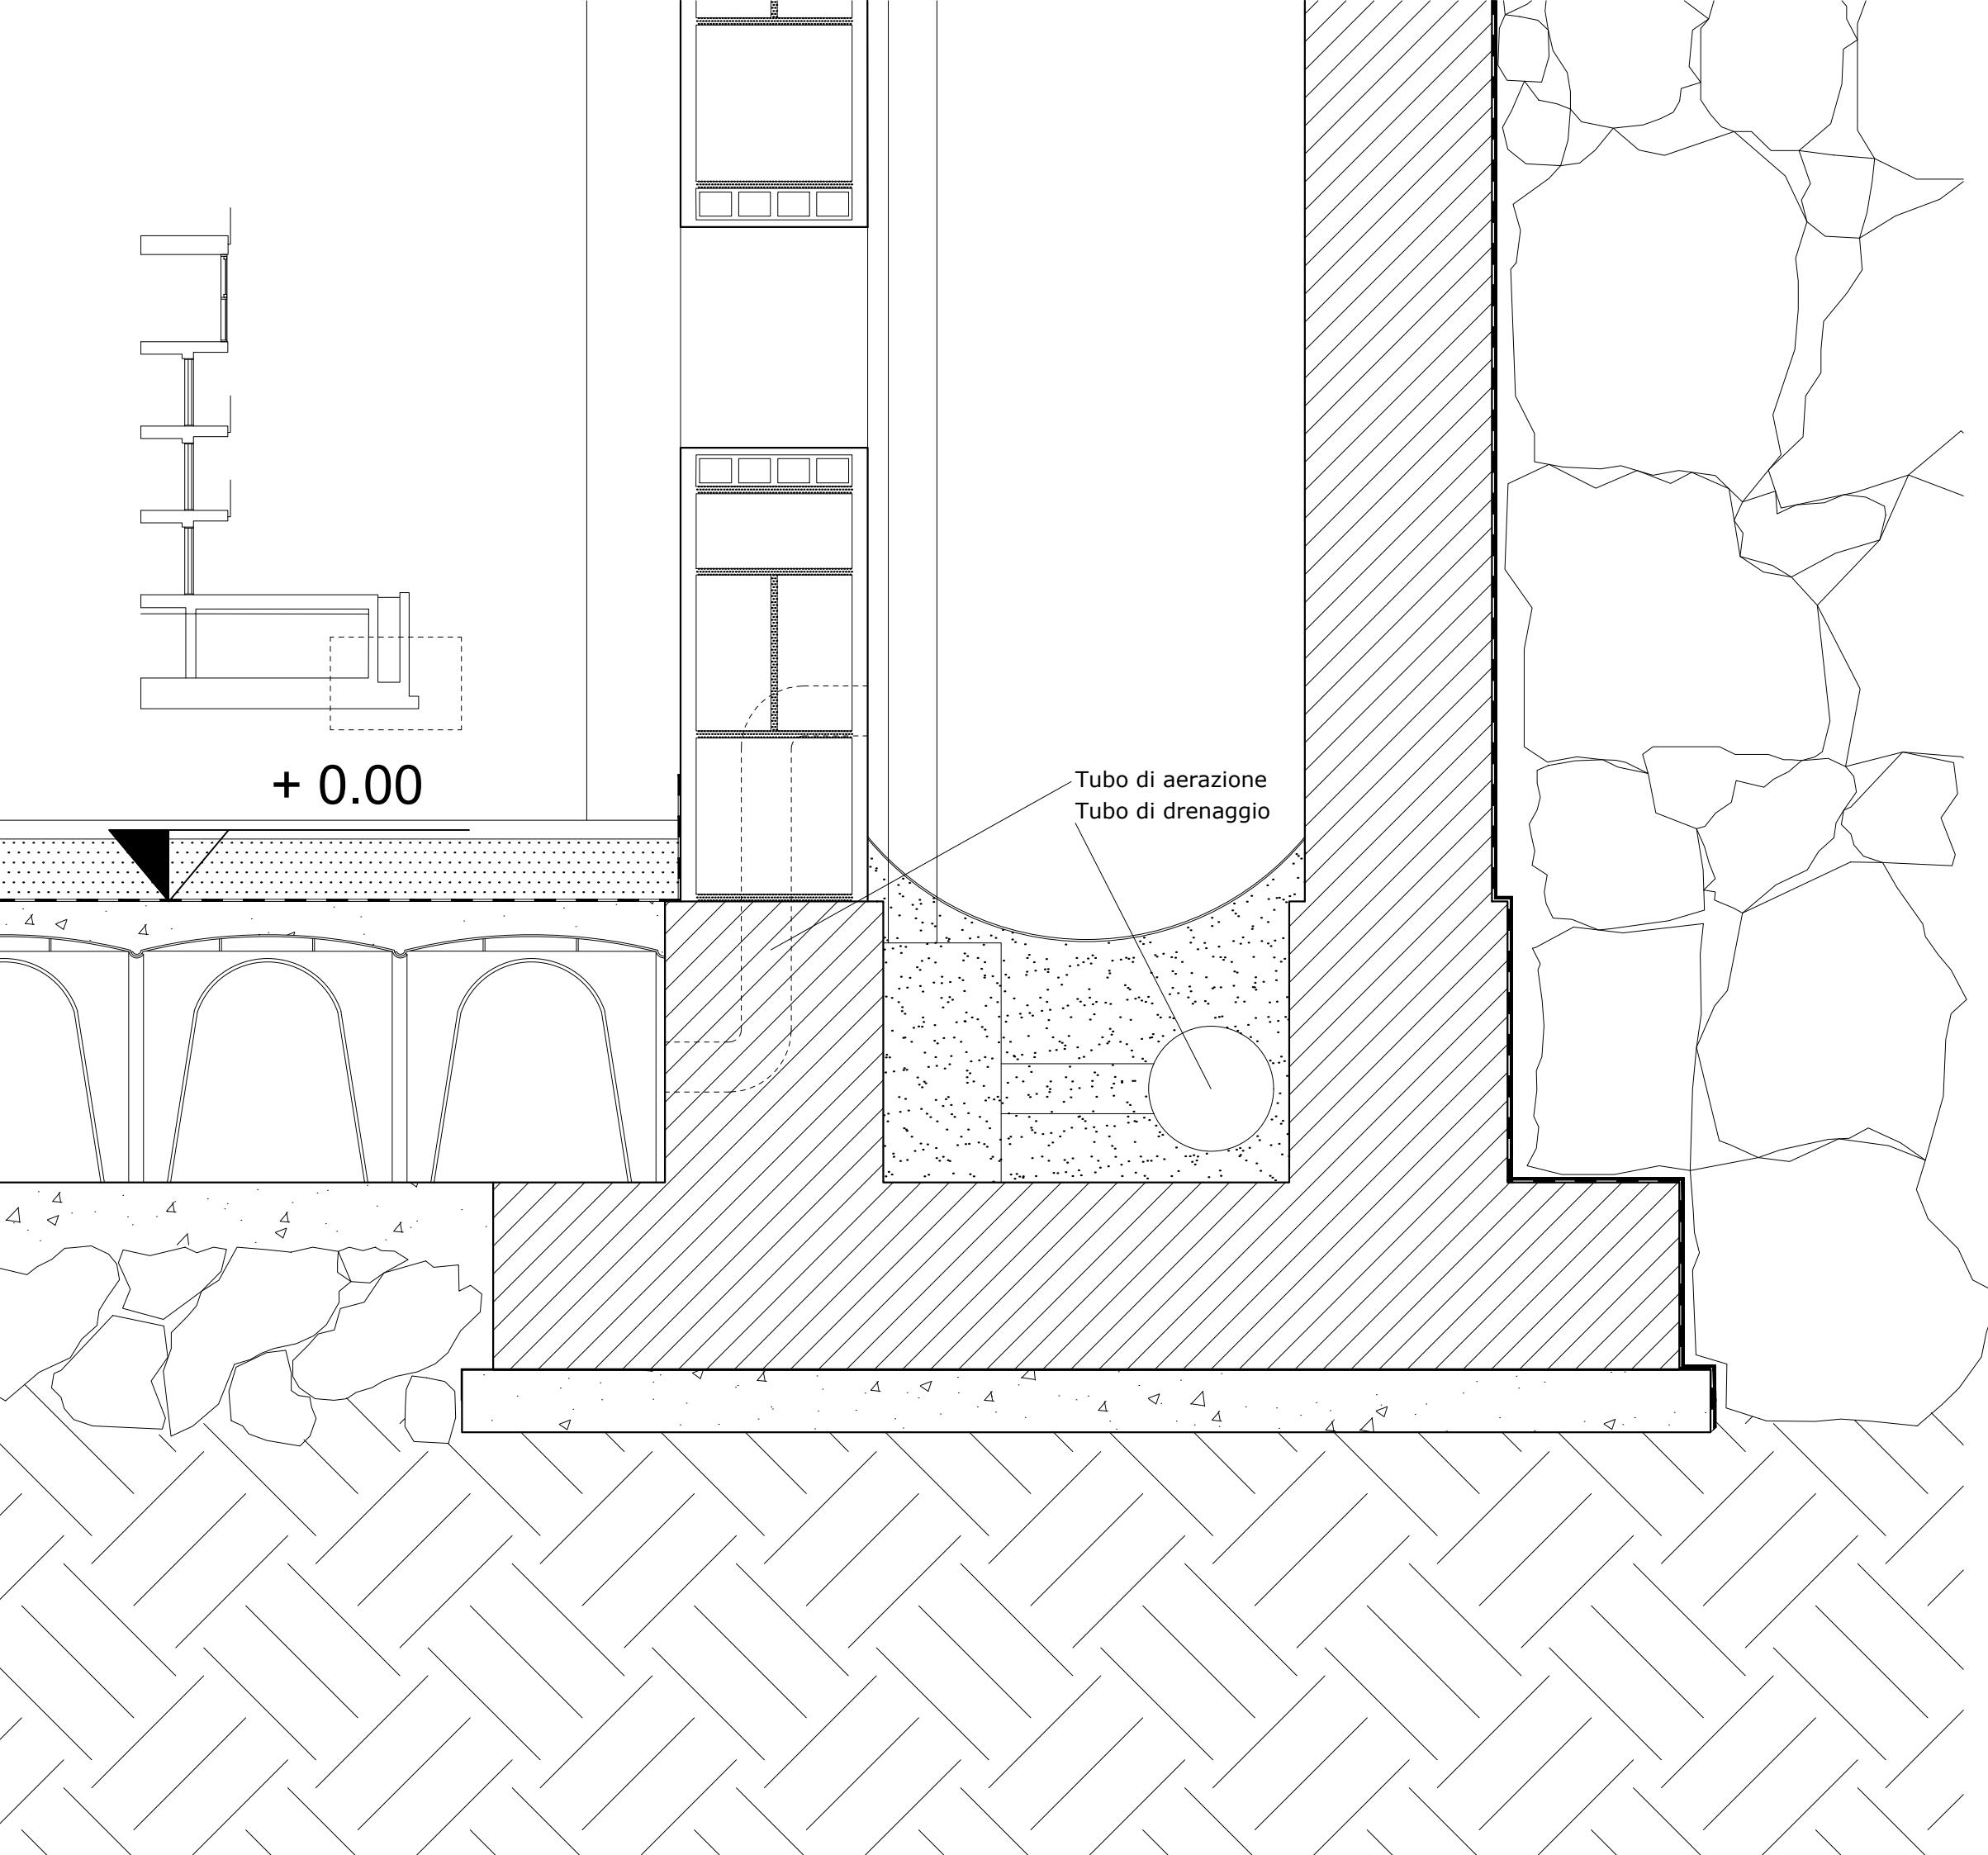


DETTAGLIO 7 di 10


TAVOLA 29

Scala 1:10

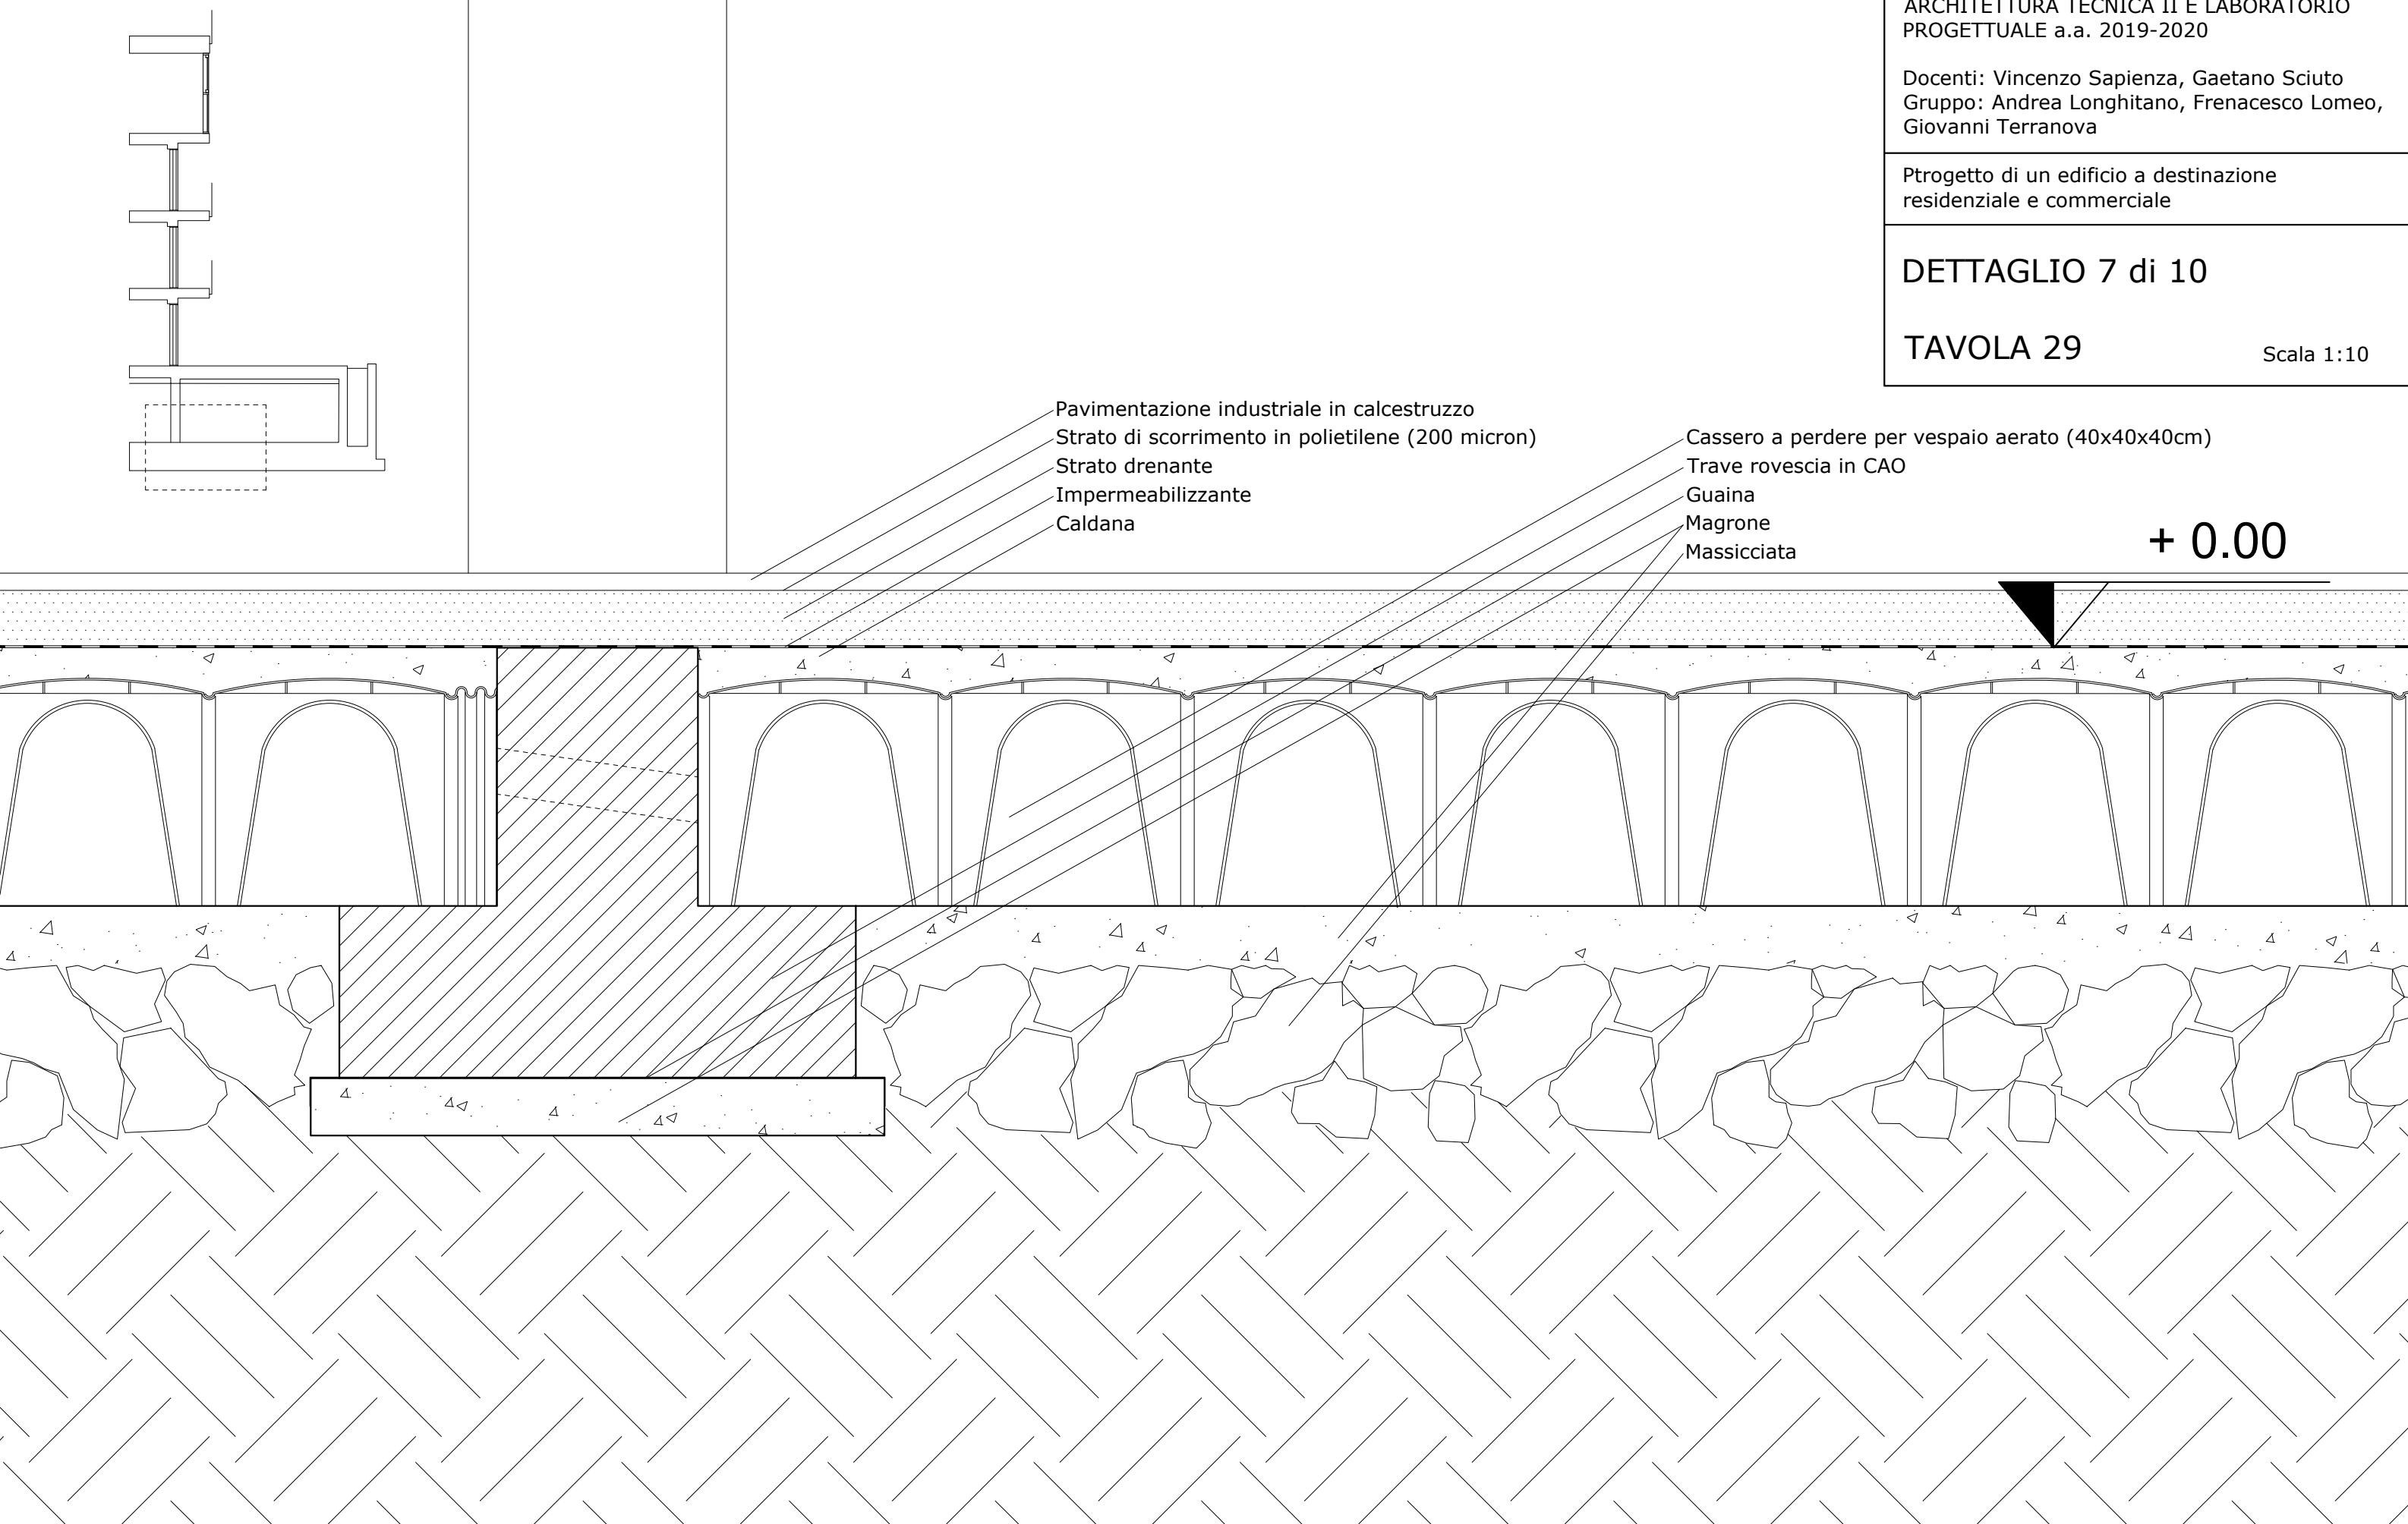

+ 8.10

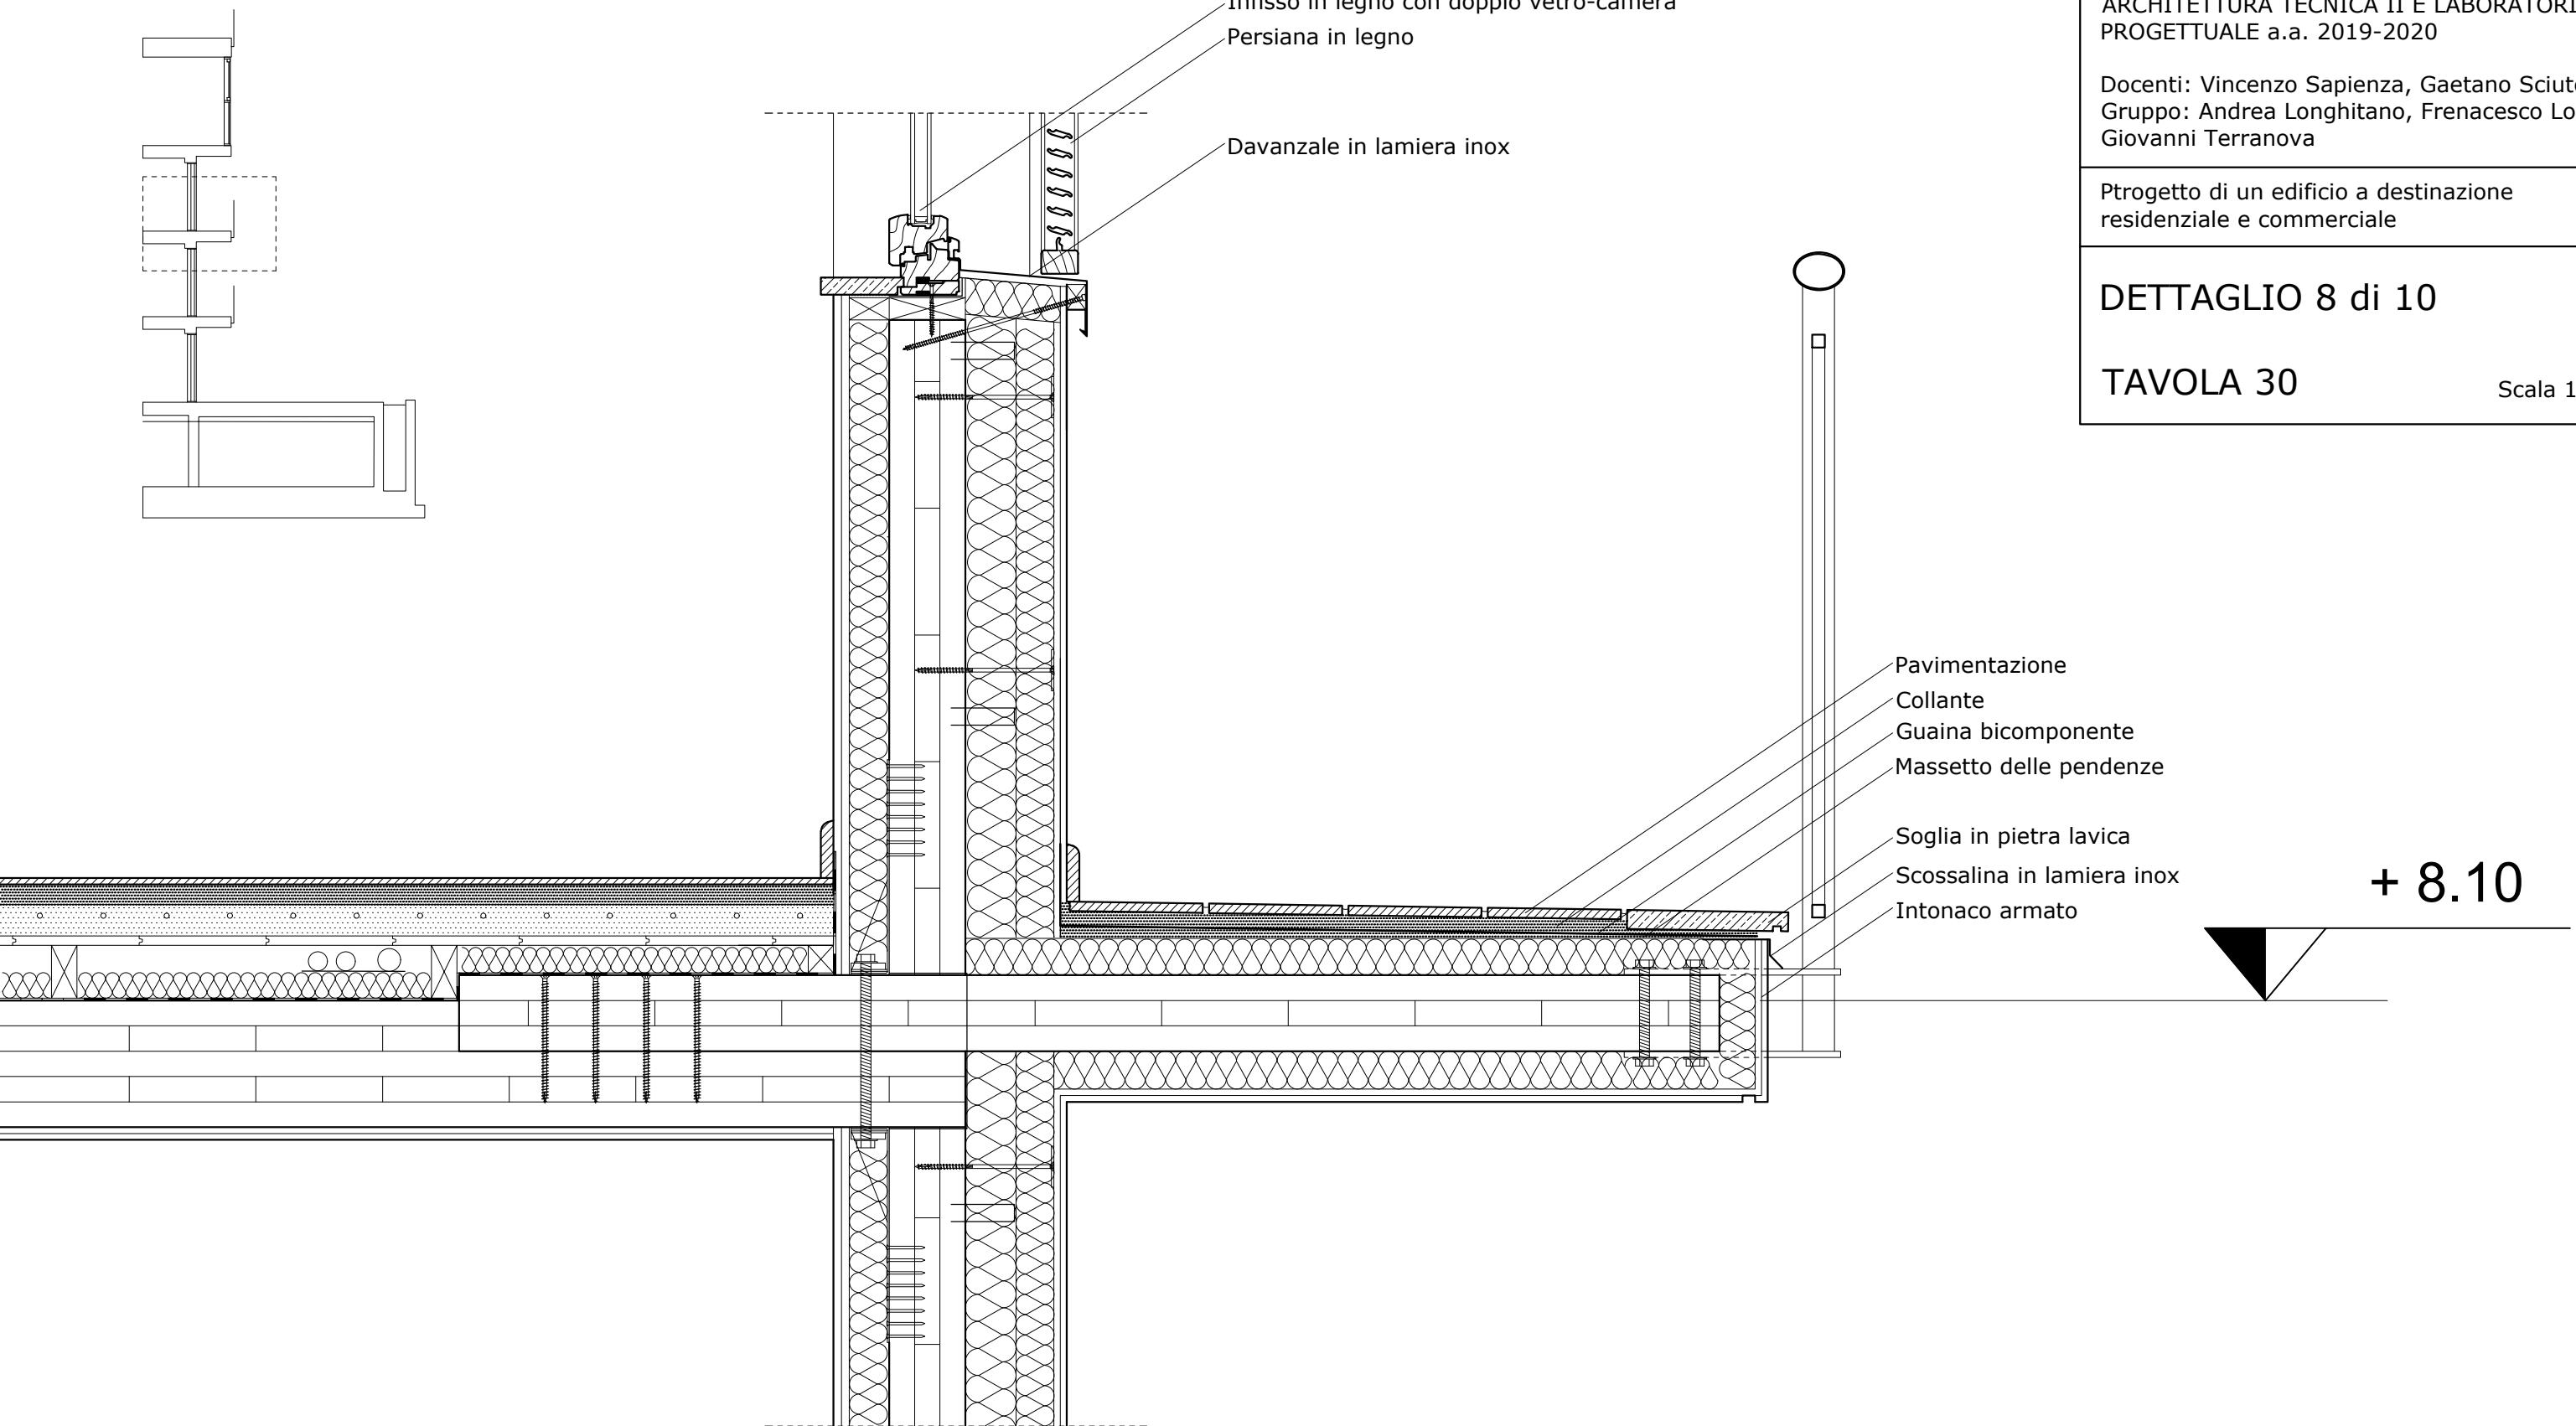




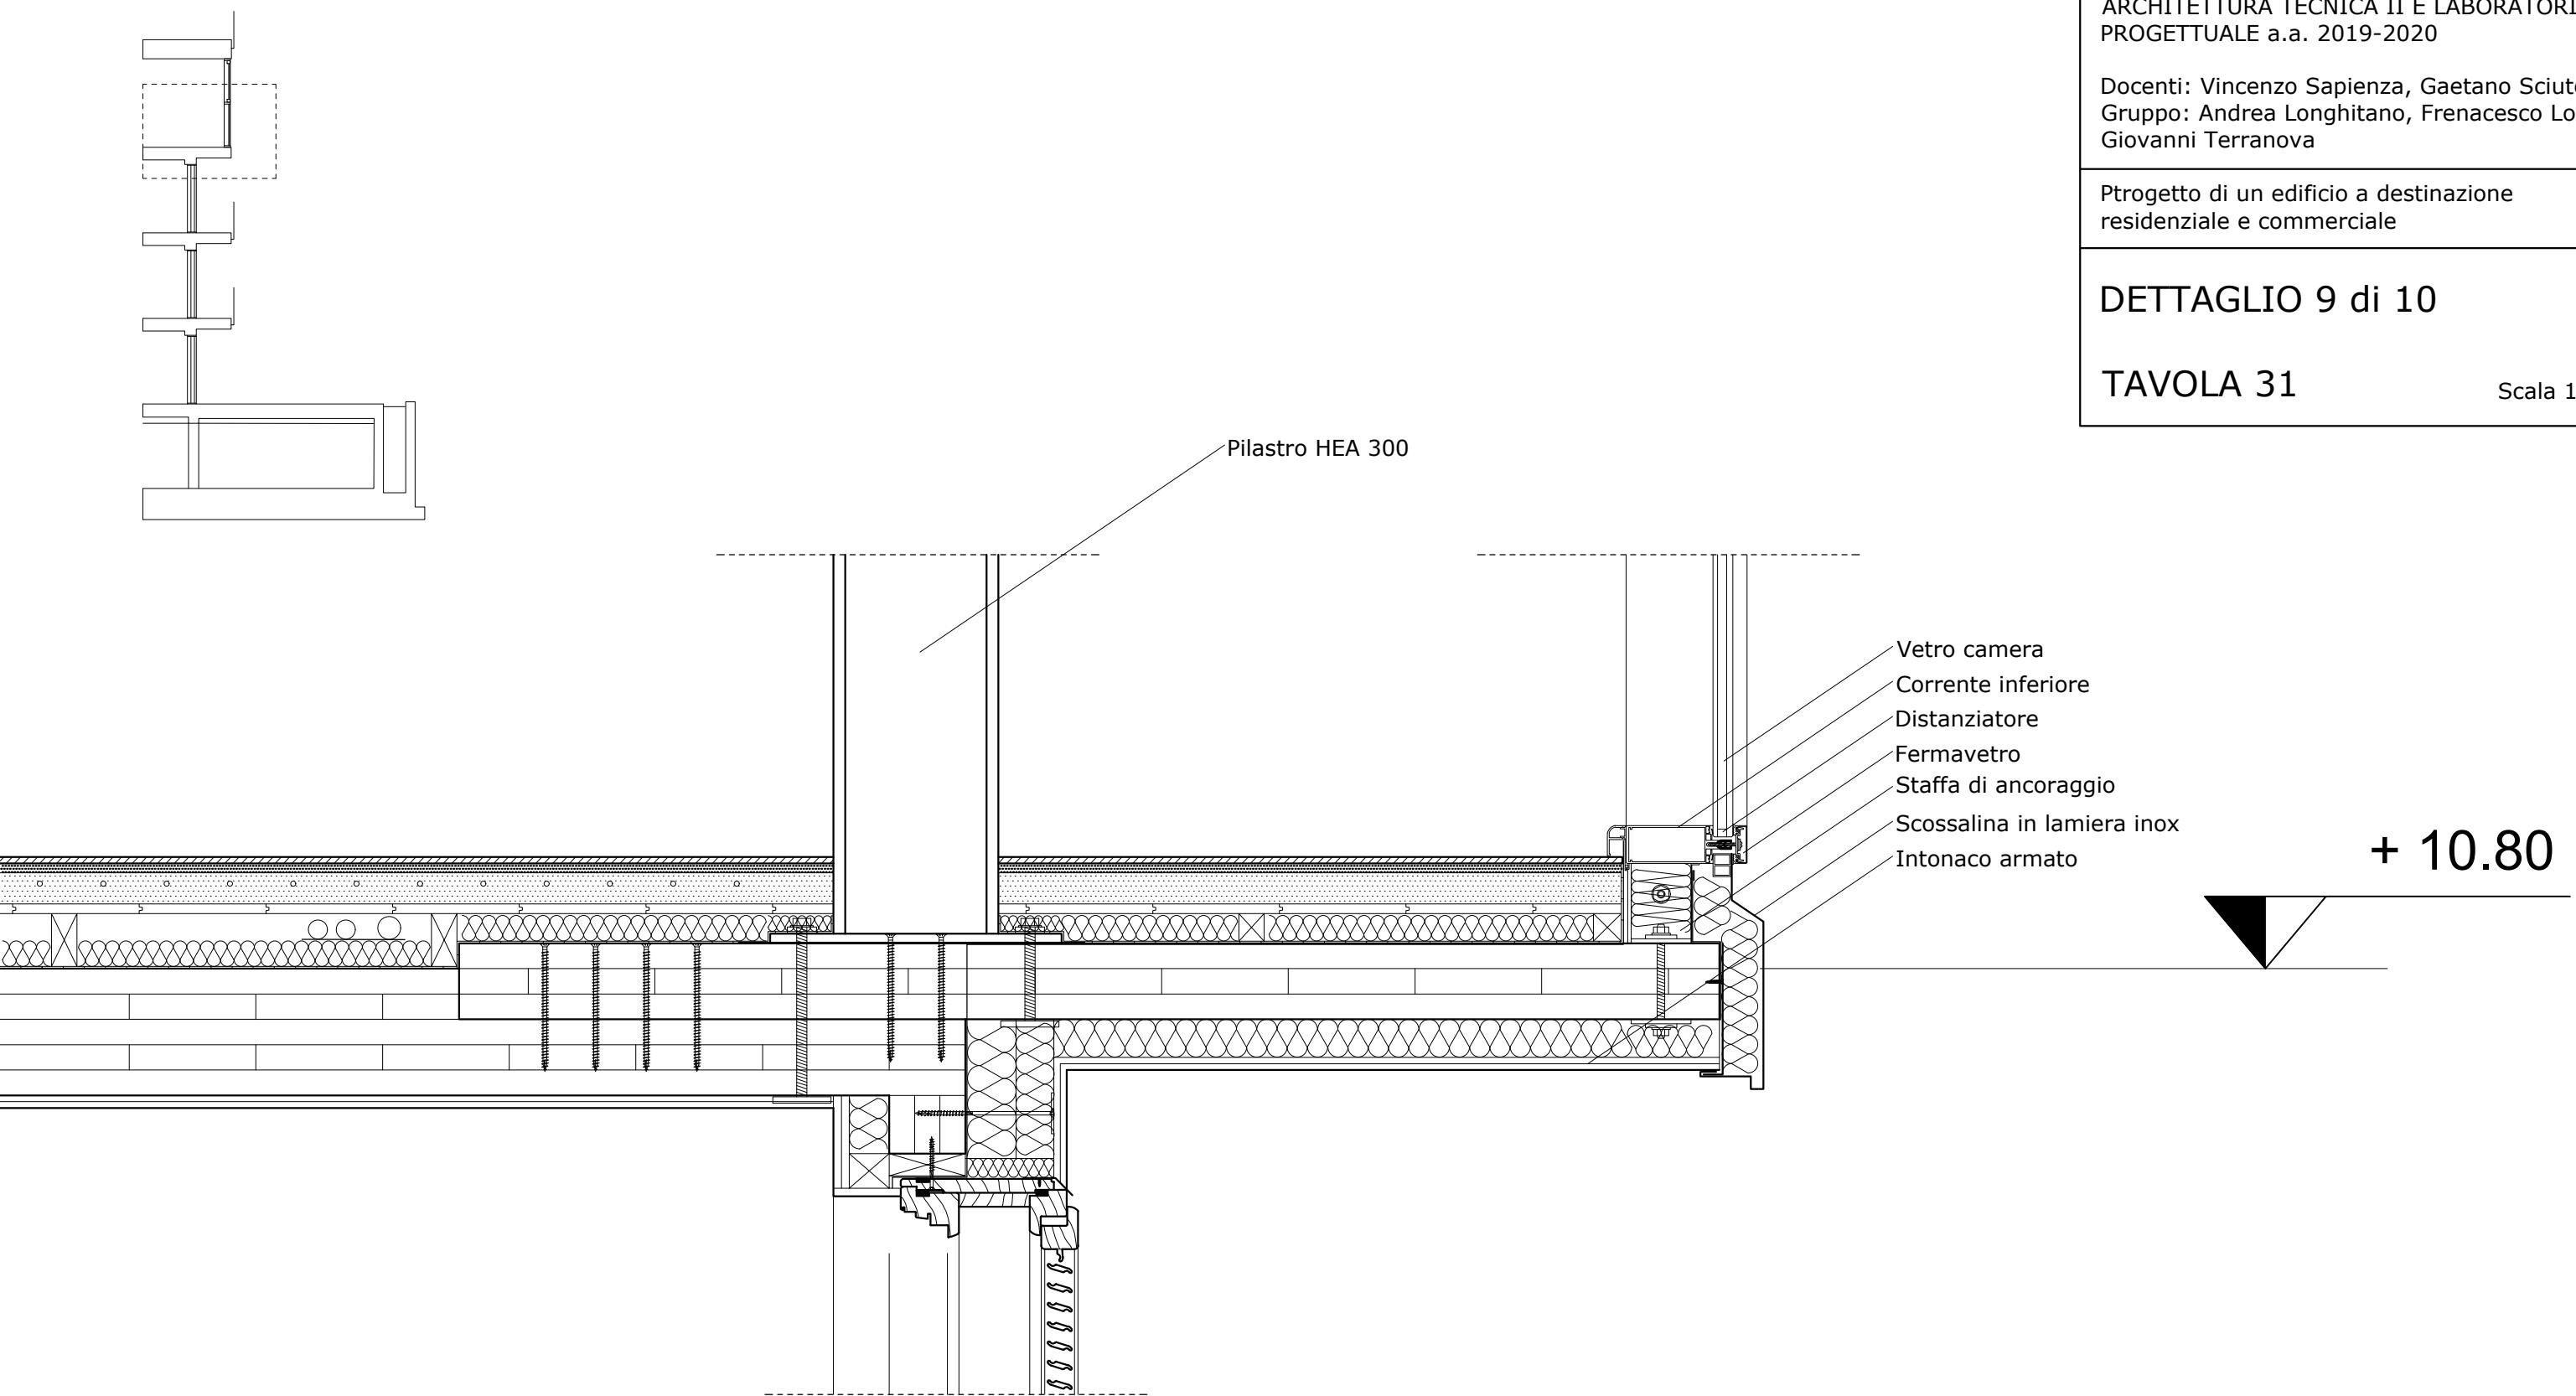


DETTAGLIO 10 di 10



TAVOLA 32

Scala 1:10

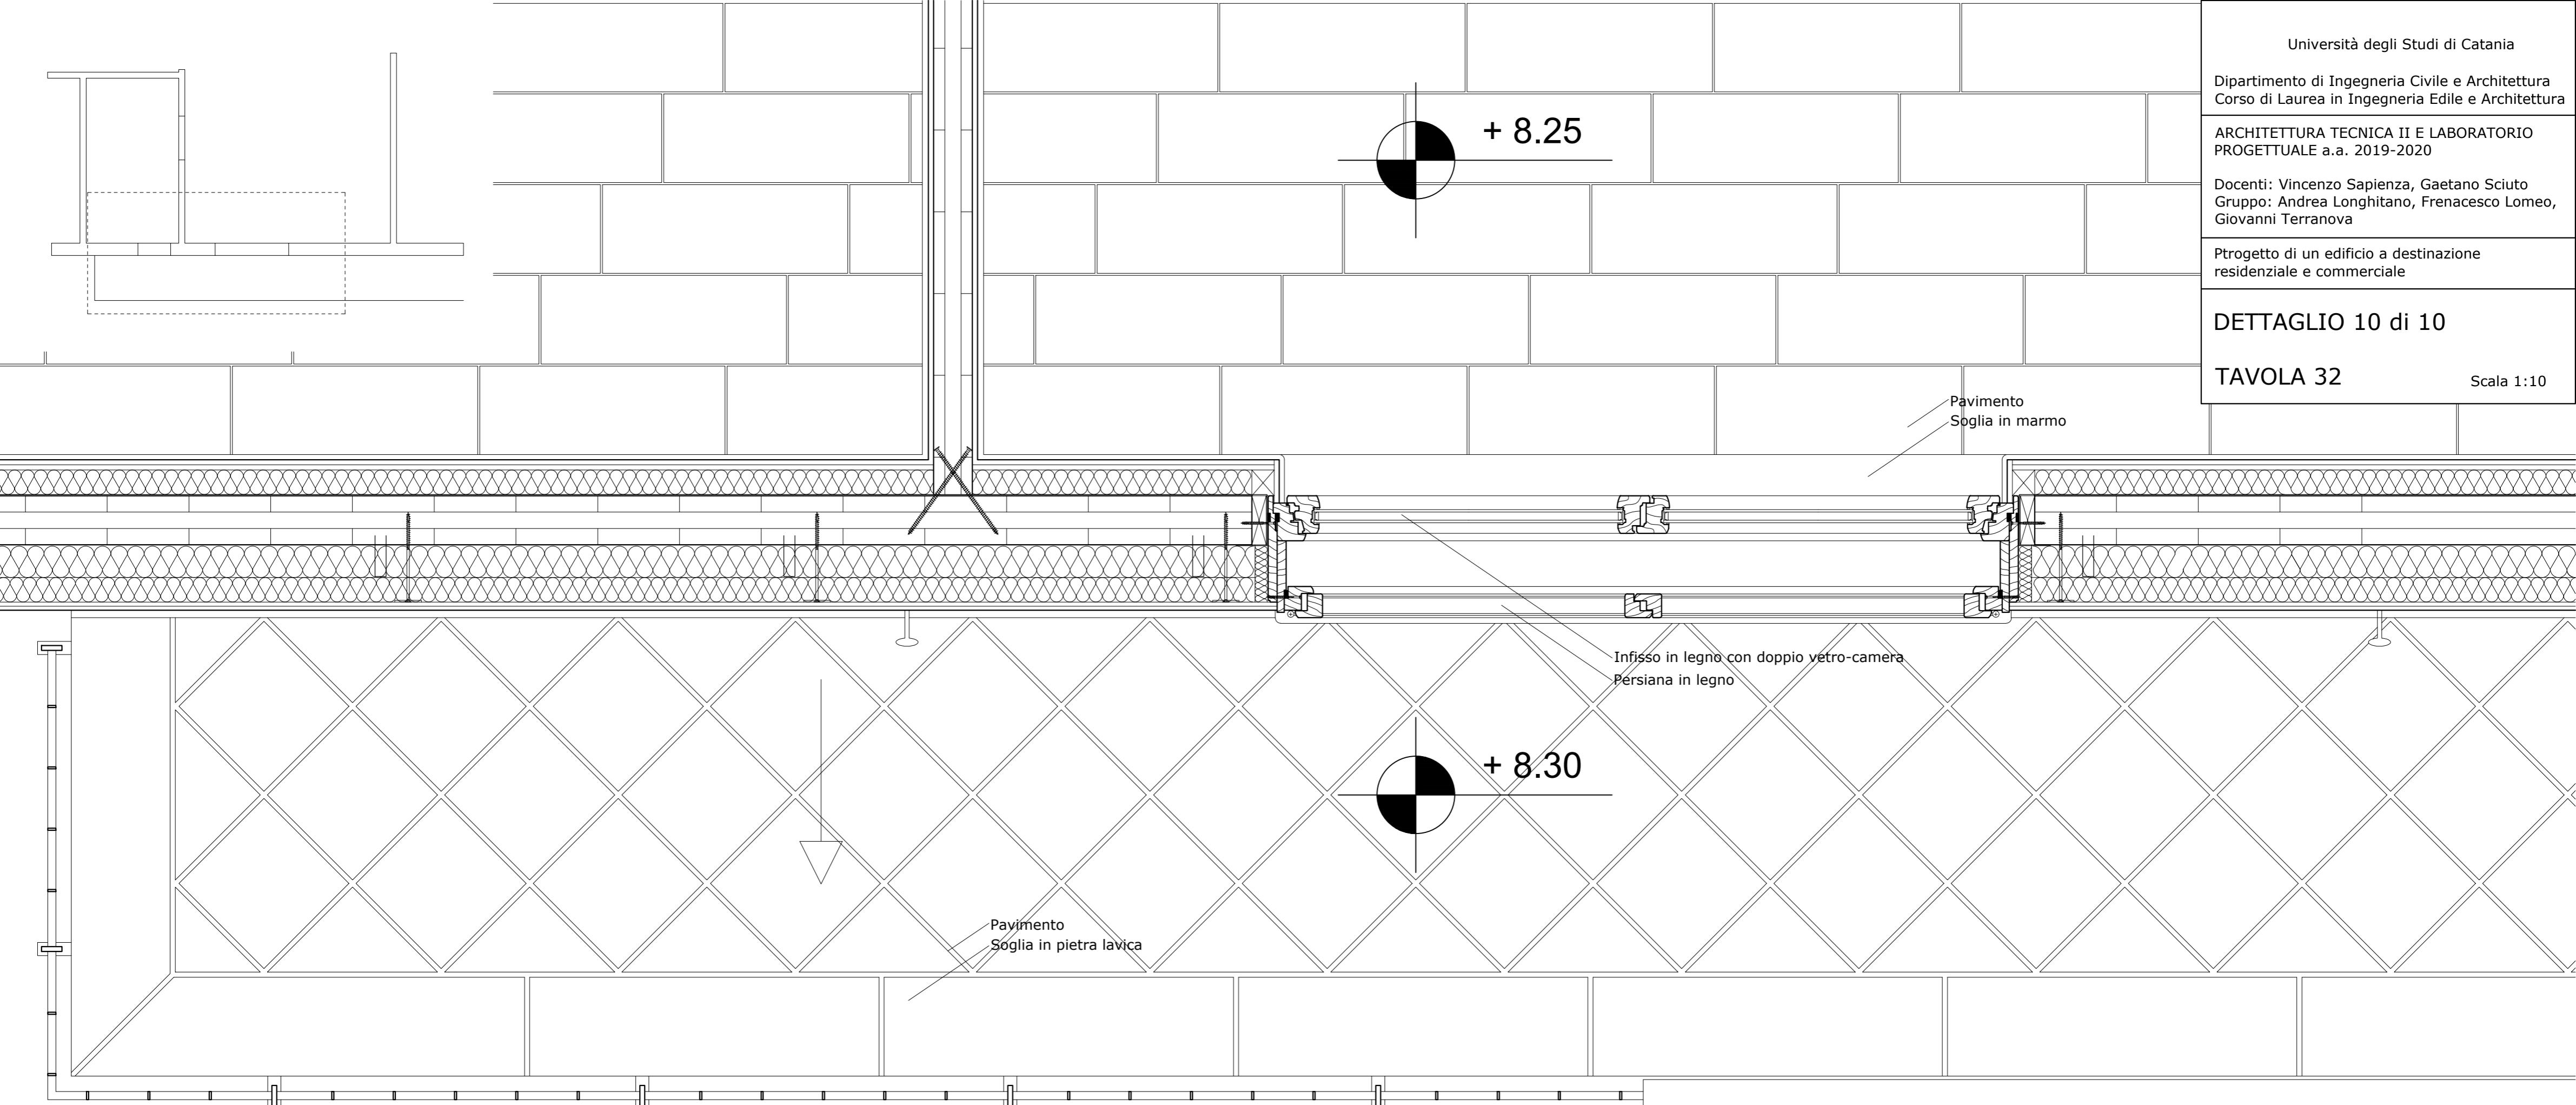

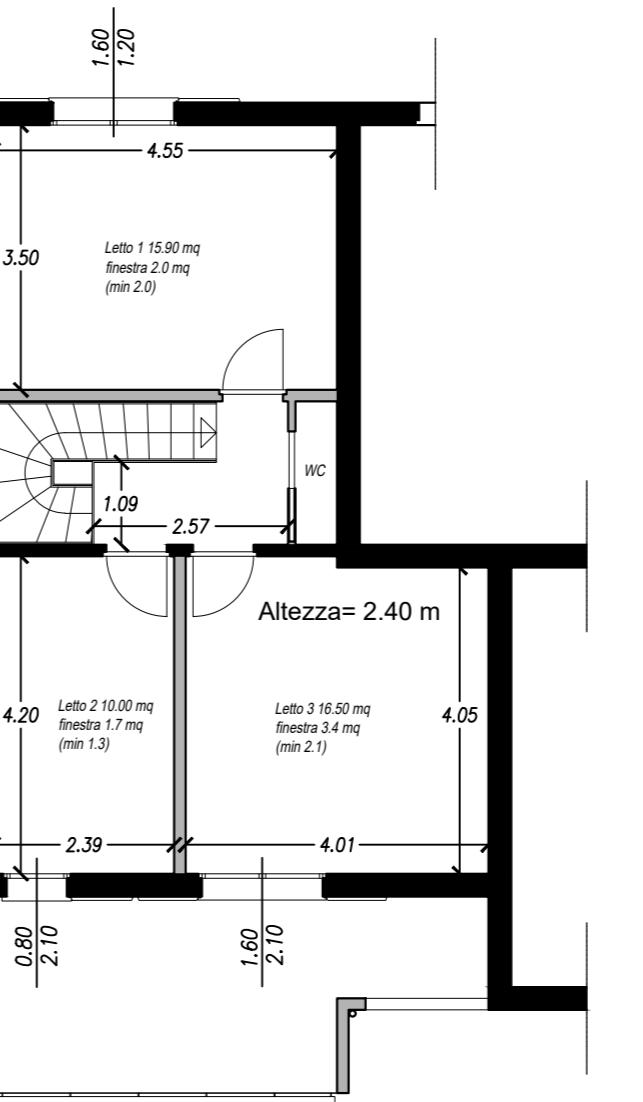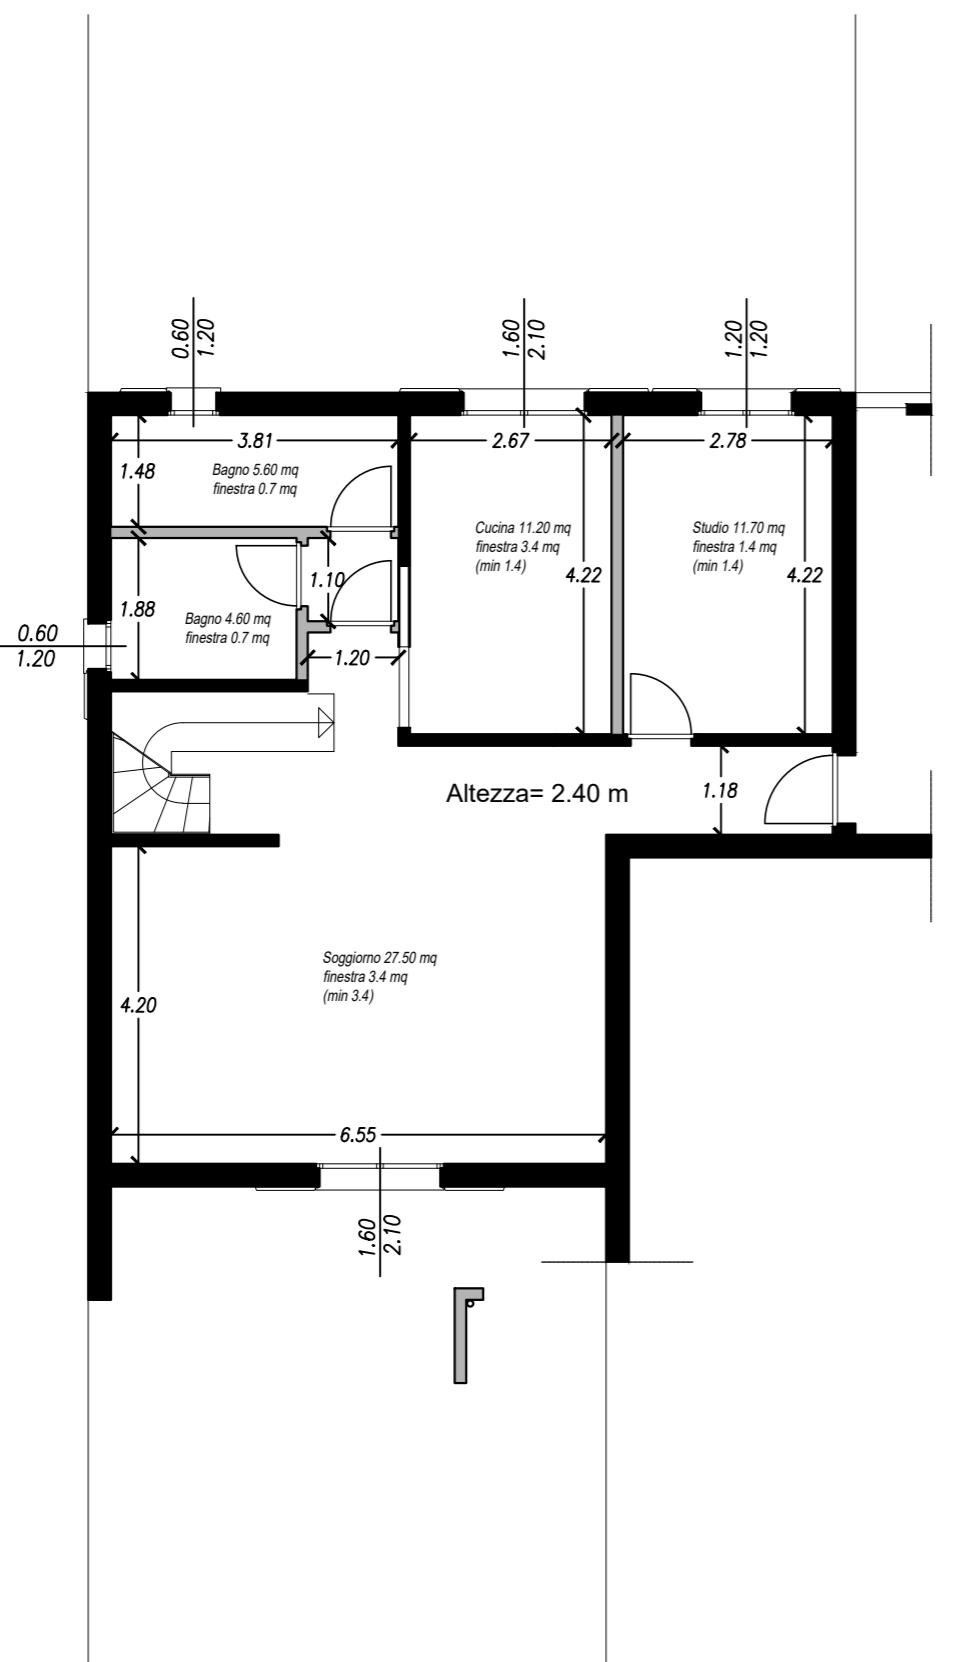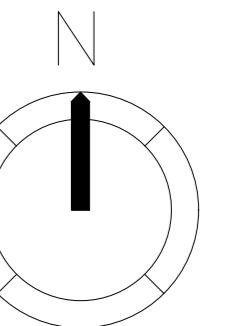

DUPLEX (134 mq)

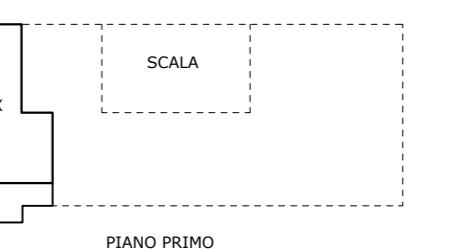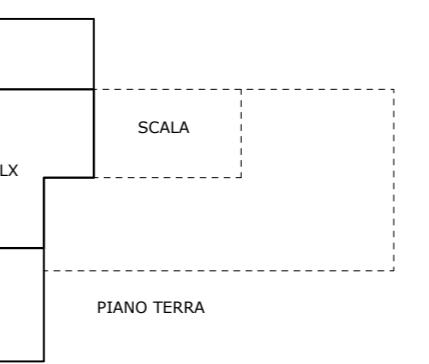



Università degli Studi di Catania

Dipartimento di Ingegneria Civile e Architettura
Corso di Laurea in Ingegneria Edile e Architettura

ARCHITETTURA TECNICA II E LABORATORIO
PROGETTUALE a.a. 2019-2020



Docenti: Vincenzo Sapienza, Gaetano Sciuto
Gruppo: Andrea Longhitano, Frenacesco Lomeo,
Giovanni Terranova

Progetto di un edificio a destinazione
residenziale e commerciale


RAPPORTI AEROILLUMINANTI
2 di 5
TAVOLA 34

Scala 1:100

SIMPLEX A

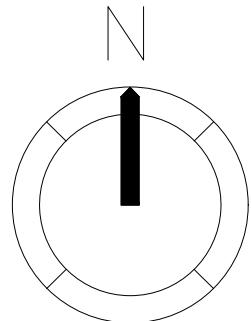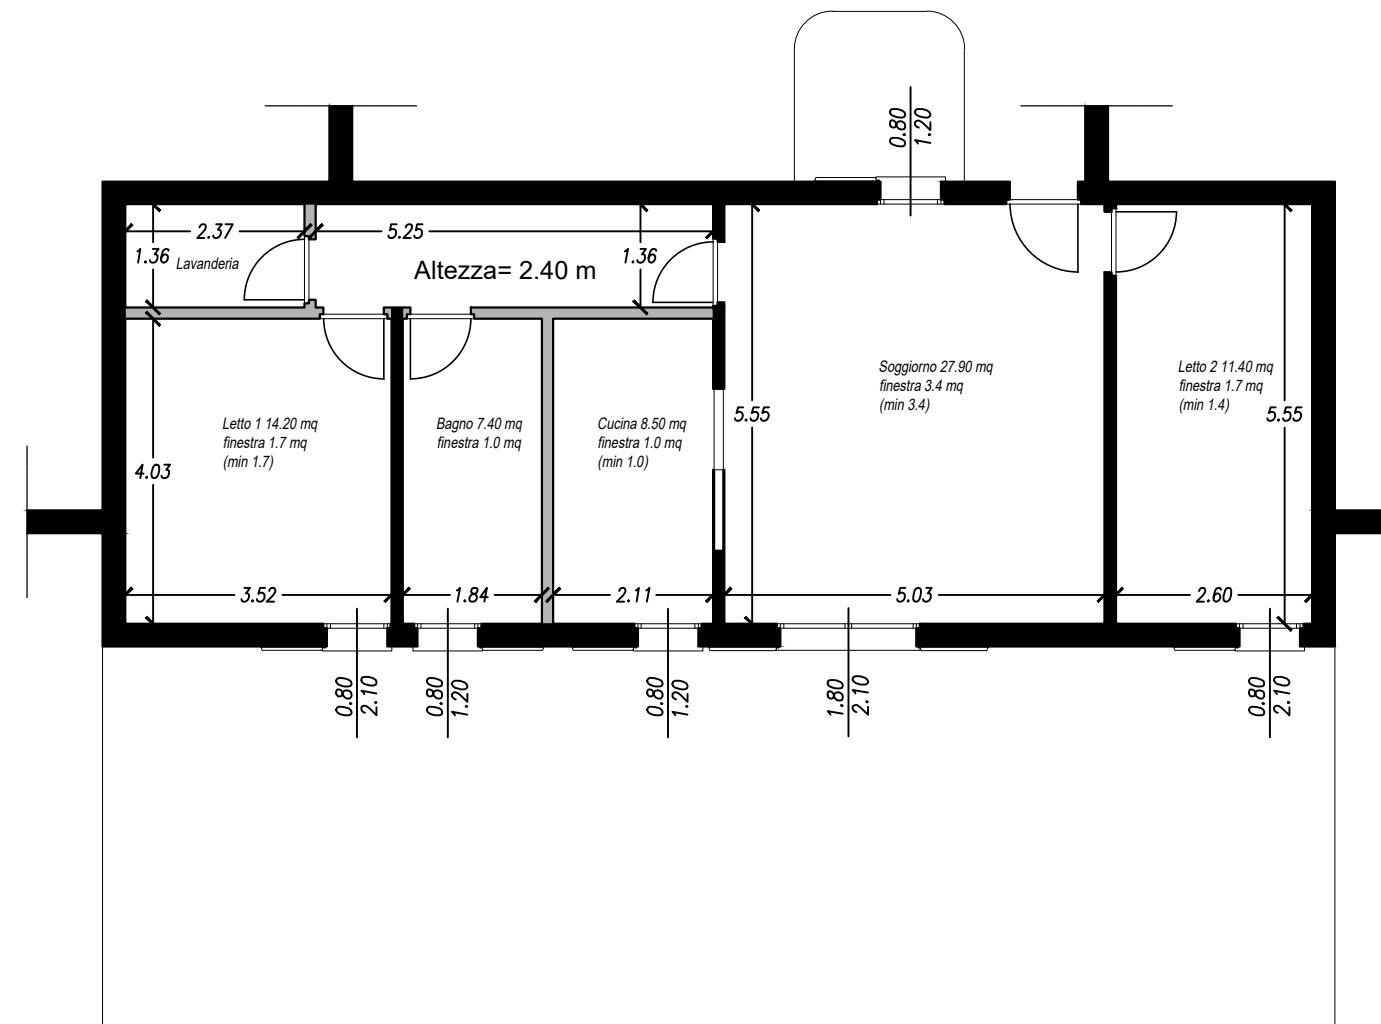

SIMPLEX A (87 mq)

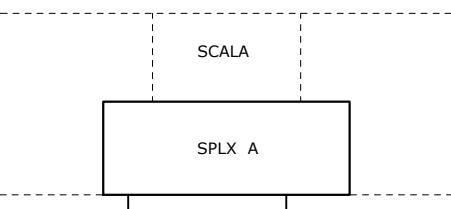



Università degli Studi di Catania

Dipartimento di Ingegneria Civile e Architettura
Corso di Laurea in Ingegneria Edile e Architettura

ARCHITETTURA TECNICA II E LABORATORIO
PROGETTUALE a.a. 2019-2020



Docenti: Vincenzo Sapienza, Gaetano Sciuto
Gruppo: Andrea Longhitano, Frenacesco Lomeo,
Giovanni Terranova

Progetto di un edificio a destinazione
residenziale e commerciale


RAPPORTI AEROILLUMINANTI
3 di 5
TAVOLA 35

Scala 1:100

SIMPLEX B

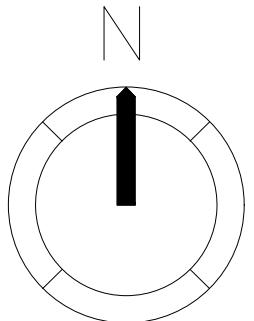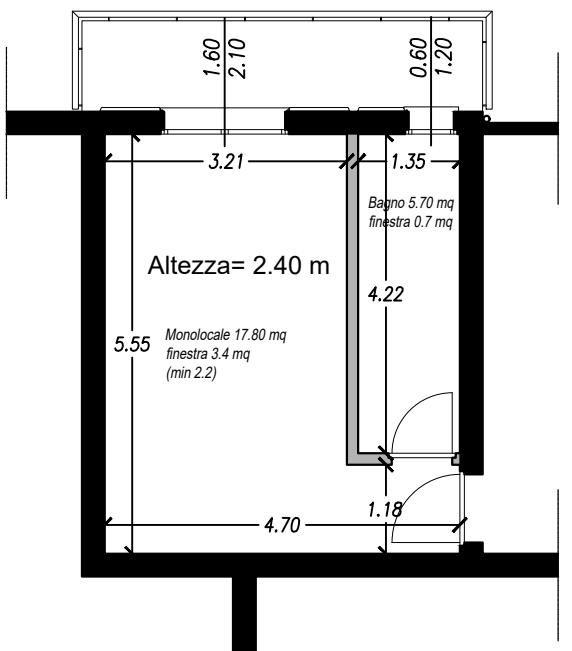

SIMPLEX B (26 mq)

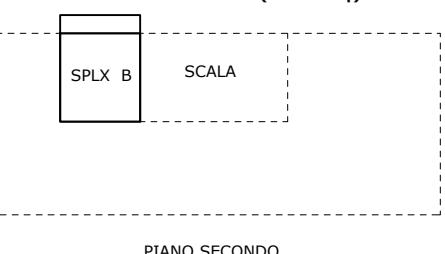



Università degli Studi di Catania

Dipartimento di Ingegneria Civile e Architettura
Corso di Laurea in Ingegneria Edile e Architettura

ARCHITETTURA TECNICA II E LABORATORIO
PROGETTUALE a.a. 2019-2020



Docenti: Vincenzo Sapienza, Gaetano Sciuto
Gruppo: Andrea Longhitano, Frenacesco Lomeo,
Giovanni Terranova

Progetto di un edificio a destinazione
residenziale e commerciale


RAPPORTI AEROILLUMINANTI
4 di 5
TAVOLA 36

Scala 1:100

SIMPLEX C

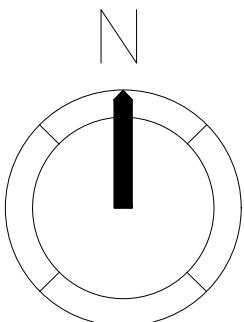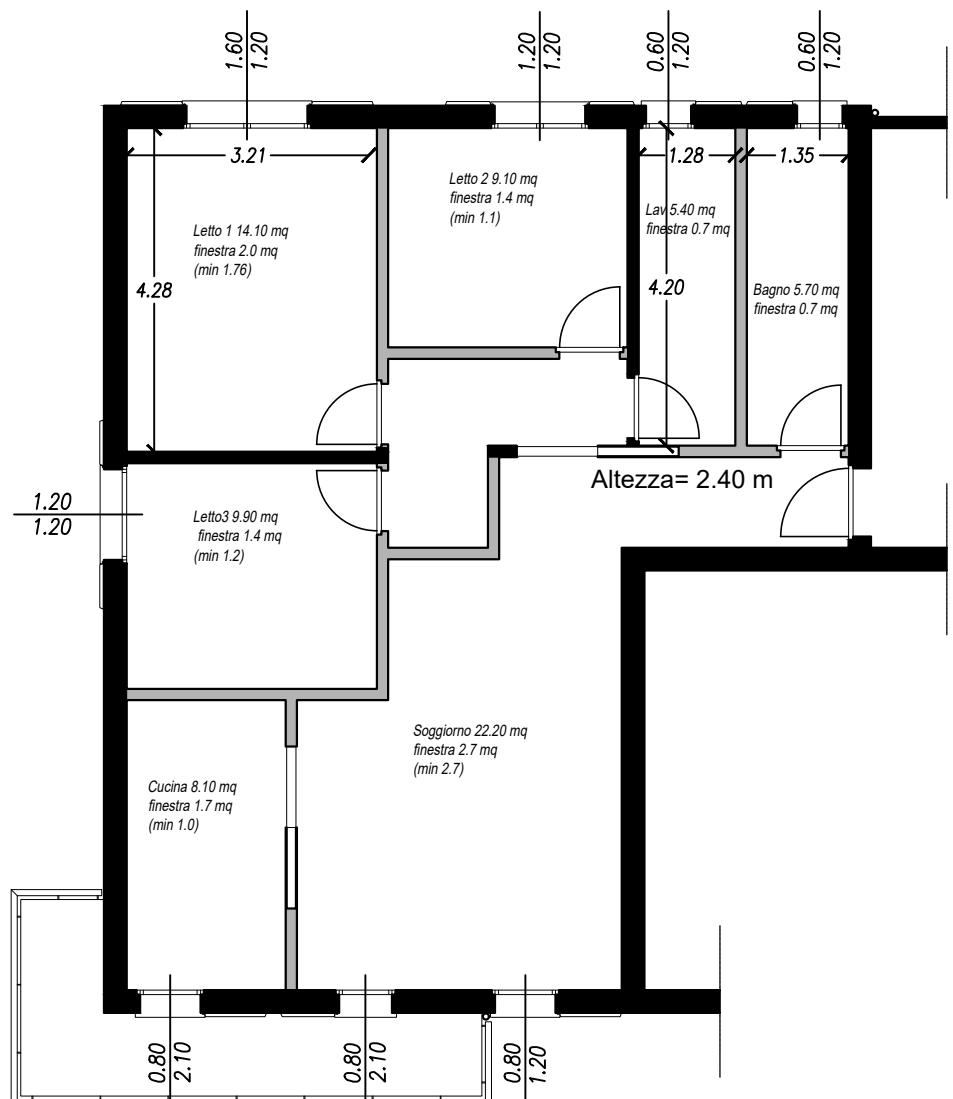

SIMPLEX C (91 mq)

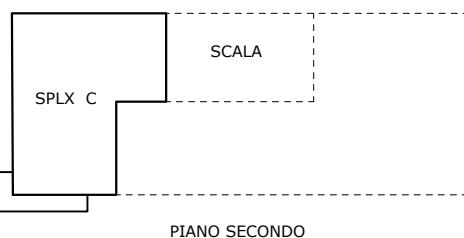



REPORT AEROILLUMINANTI

5

VOLA 37

Scala 1:100

COMMERCIALE

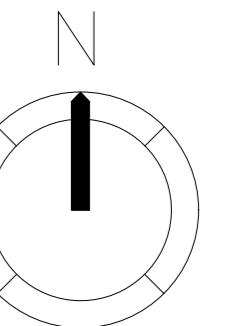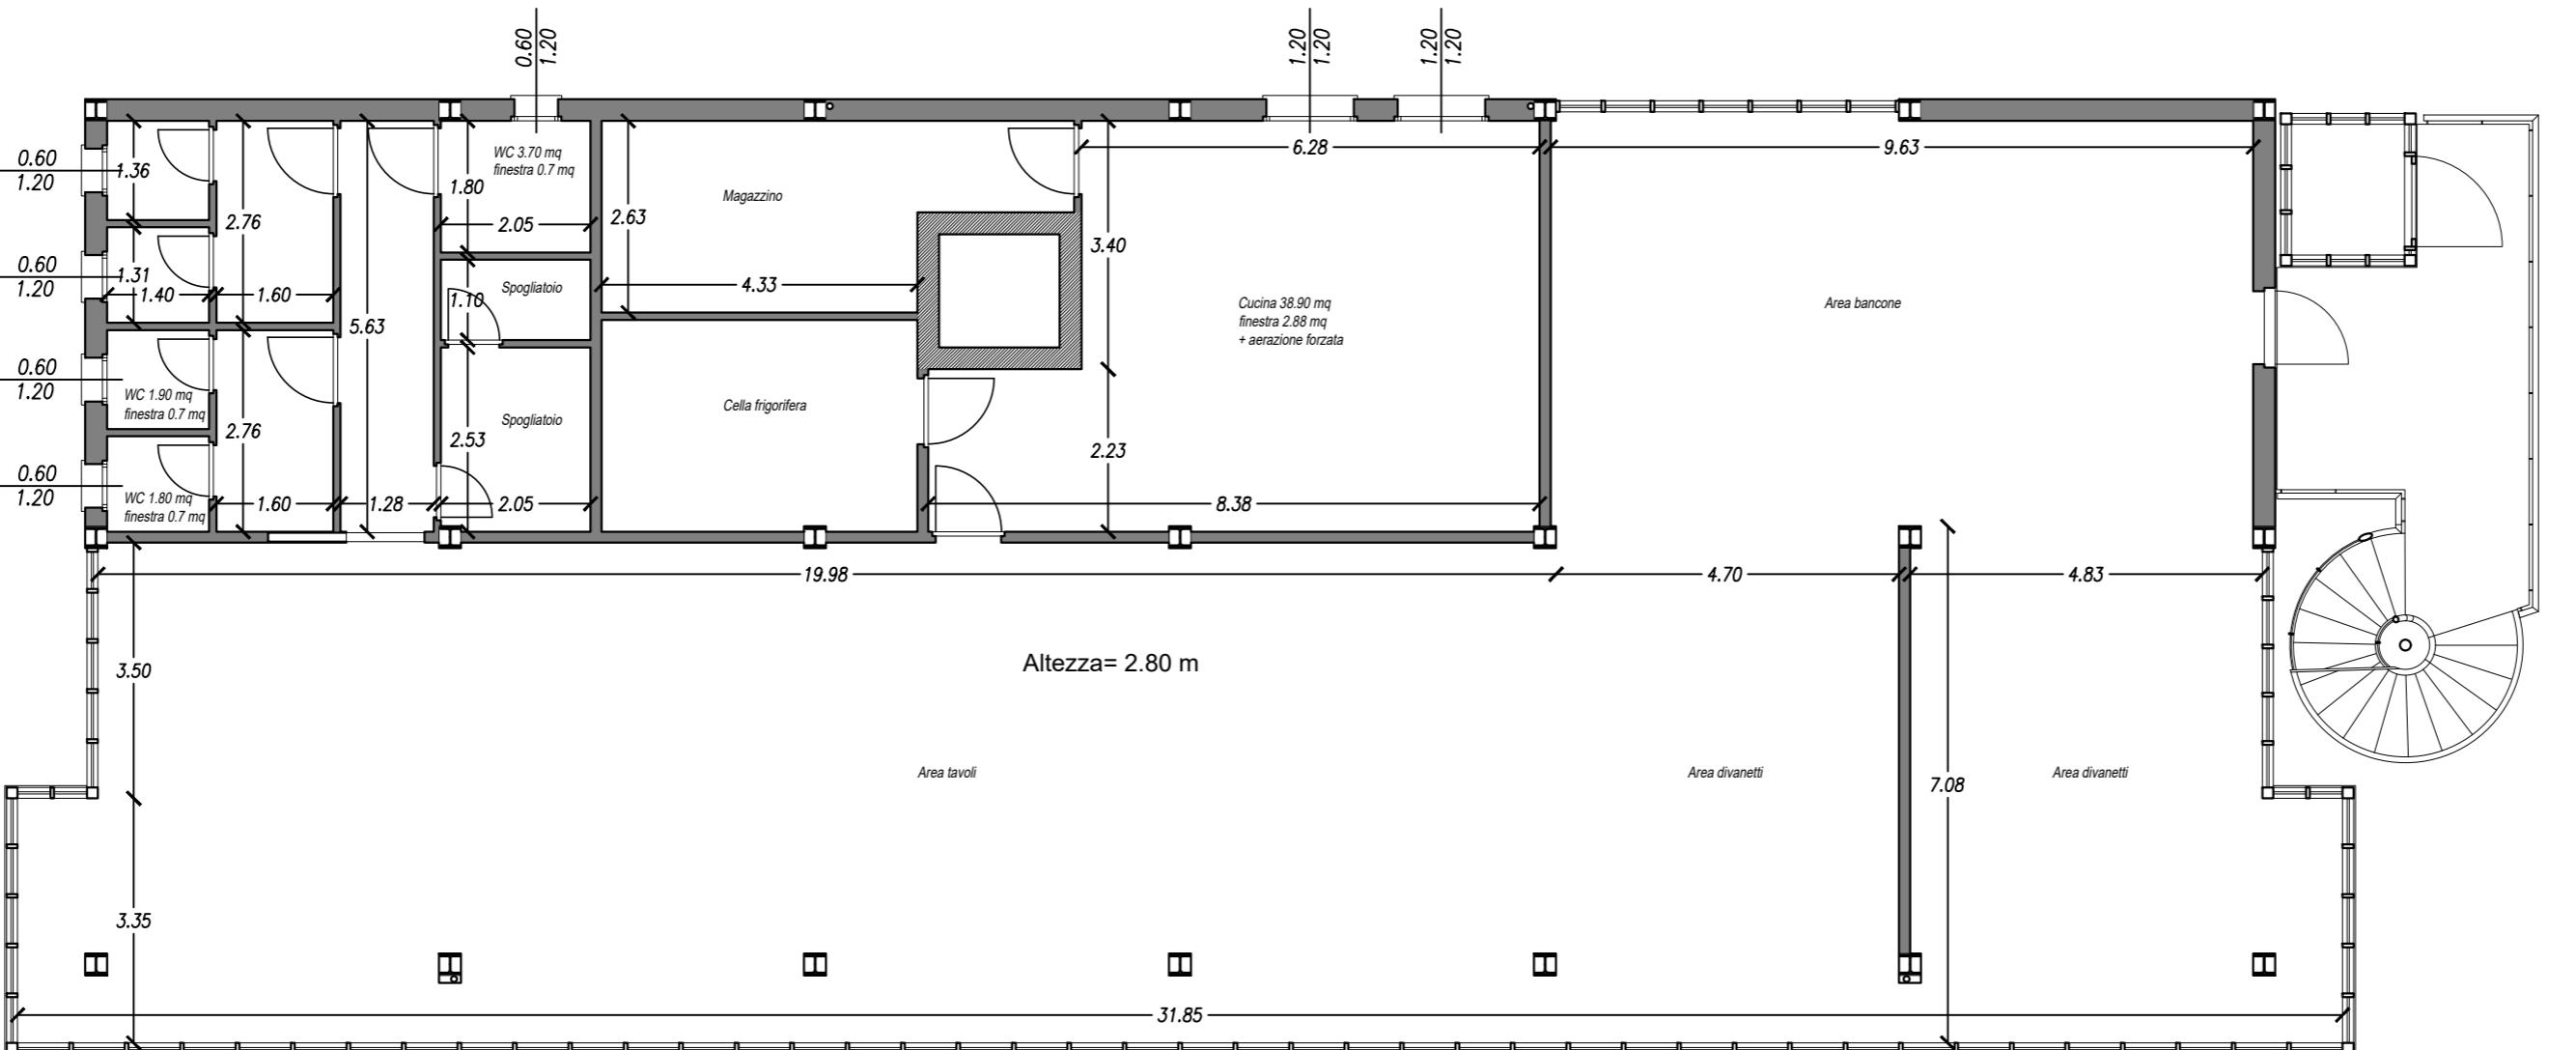

COMMERCIALE

